




# 房屋建筑面积分户平面图

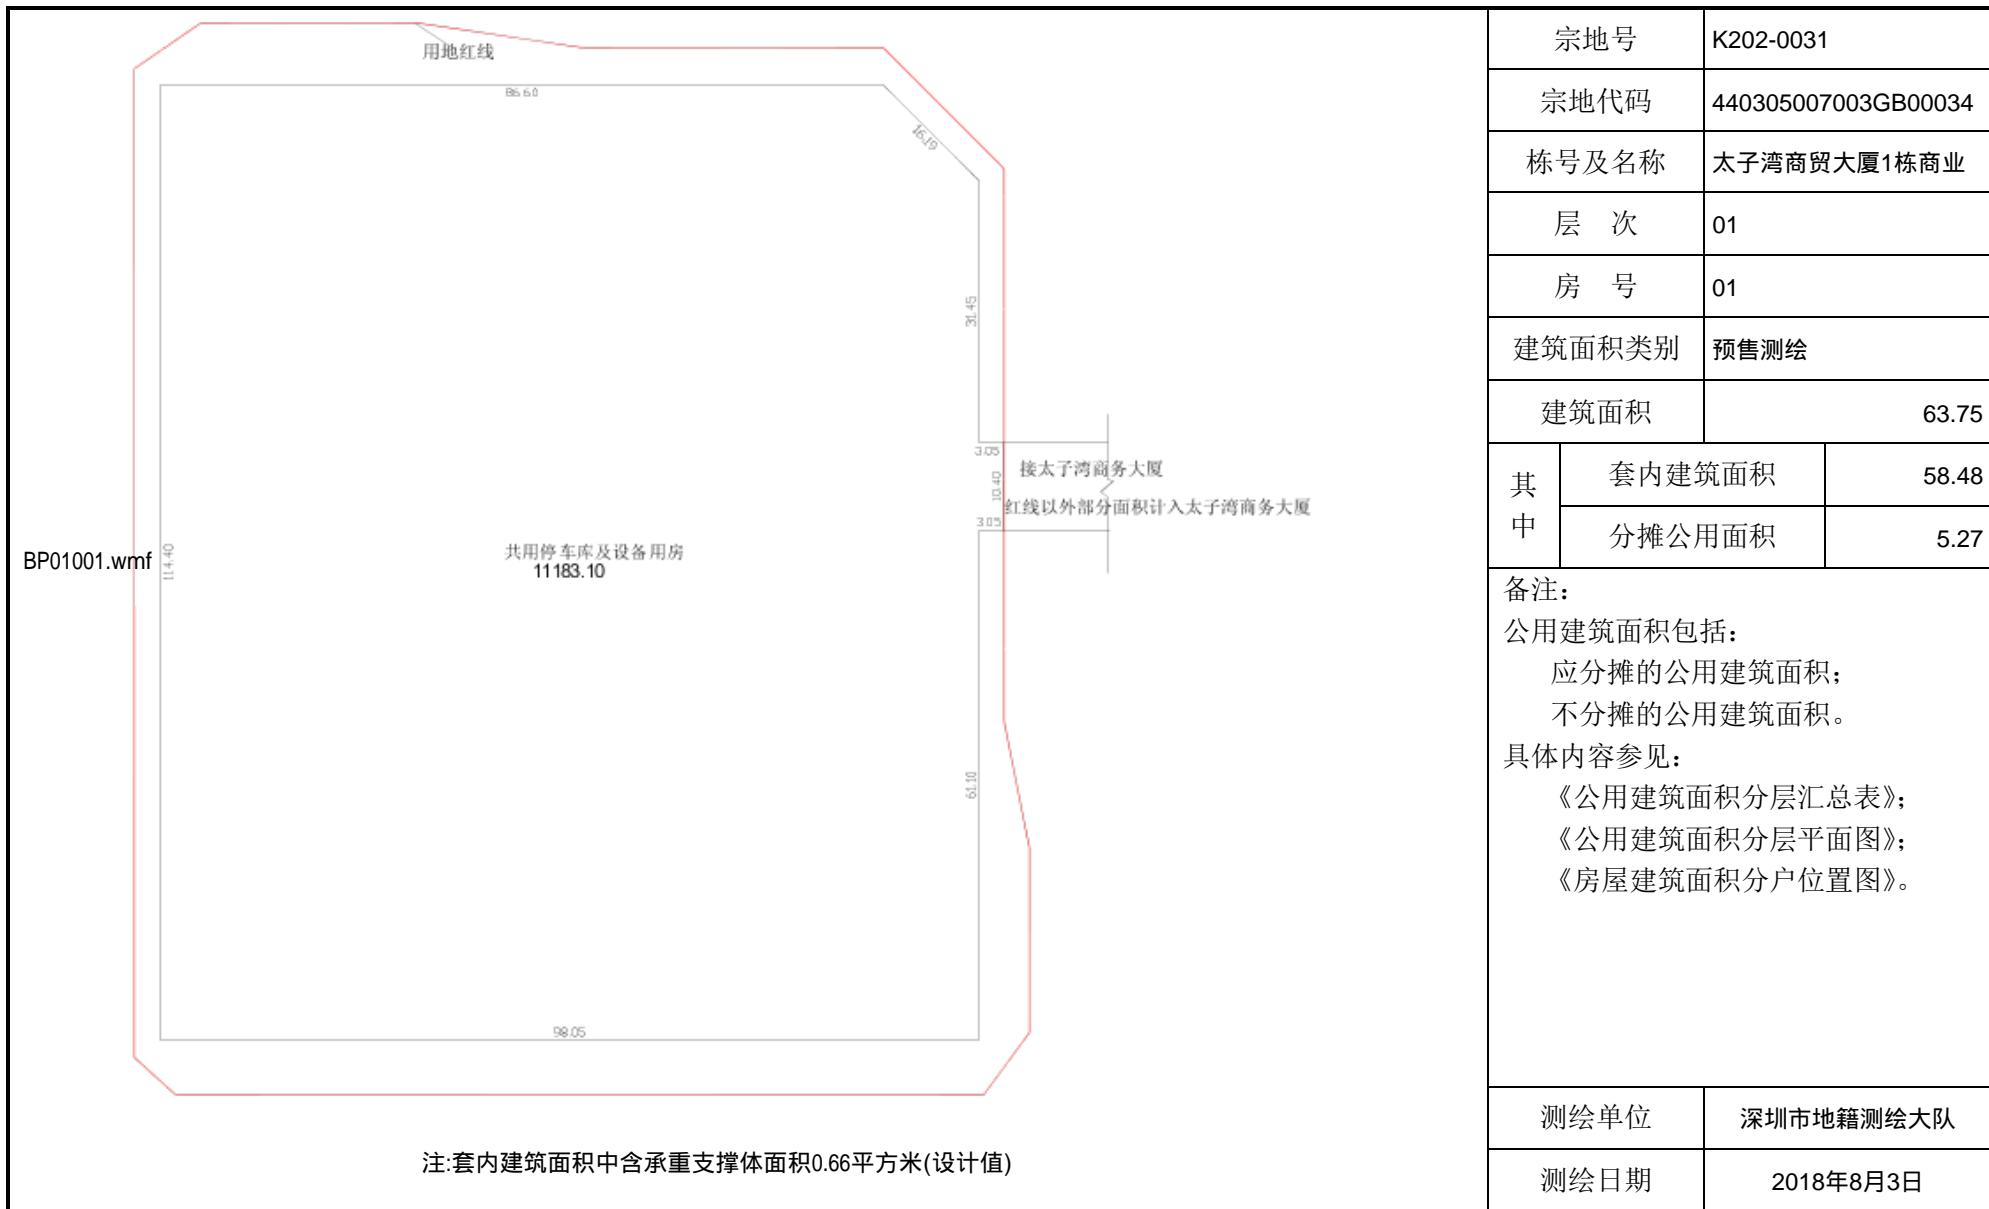


# 房屋建筑面积分户平面图

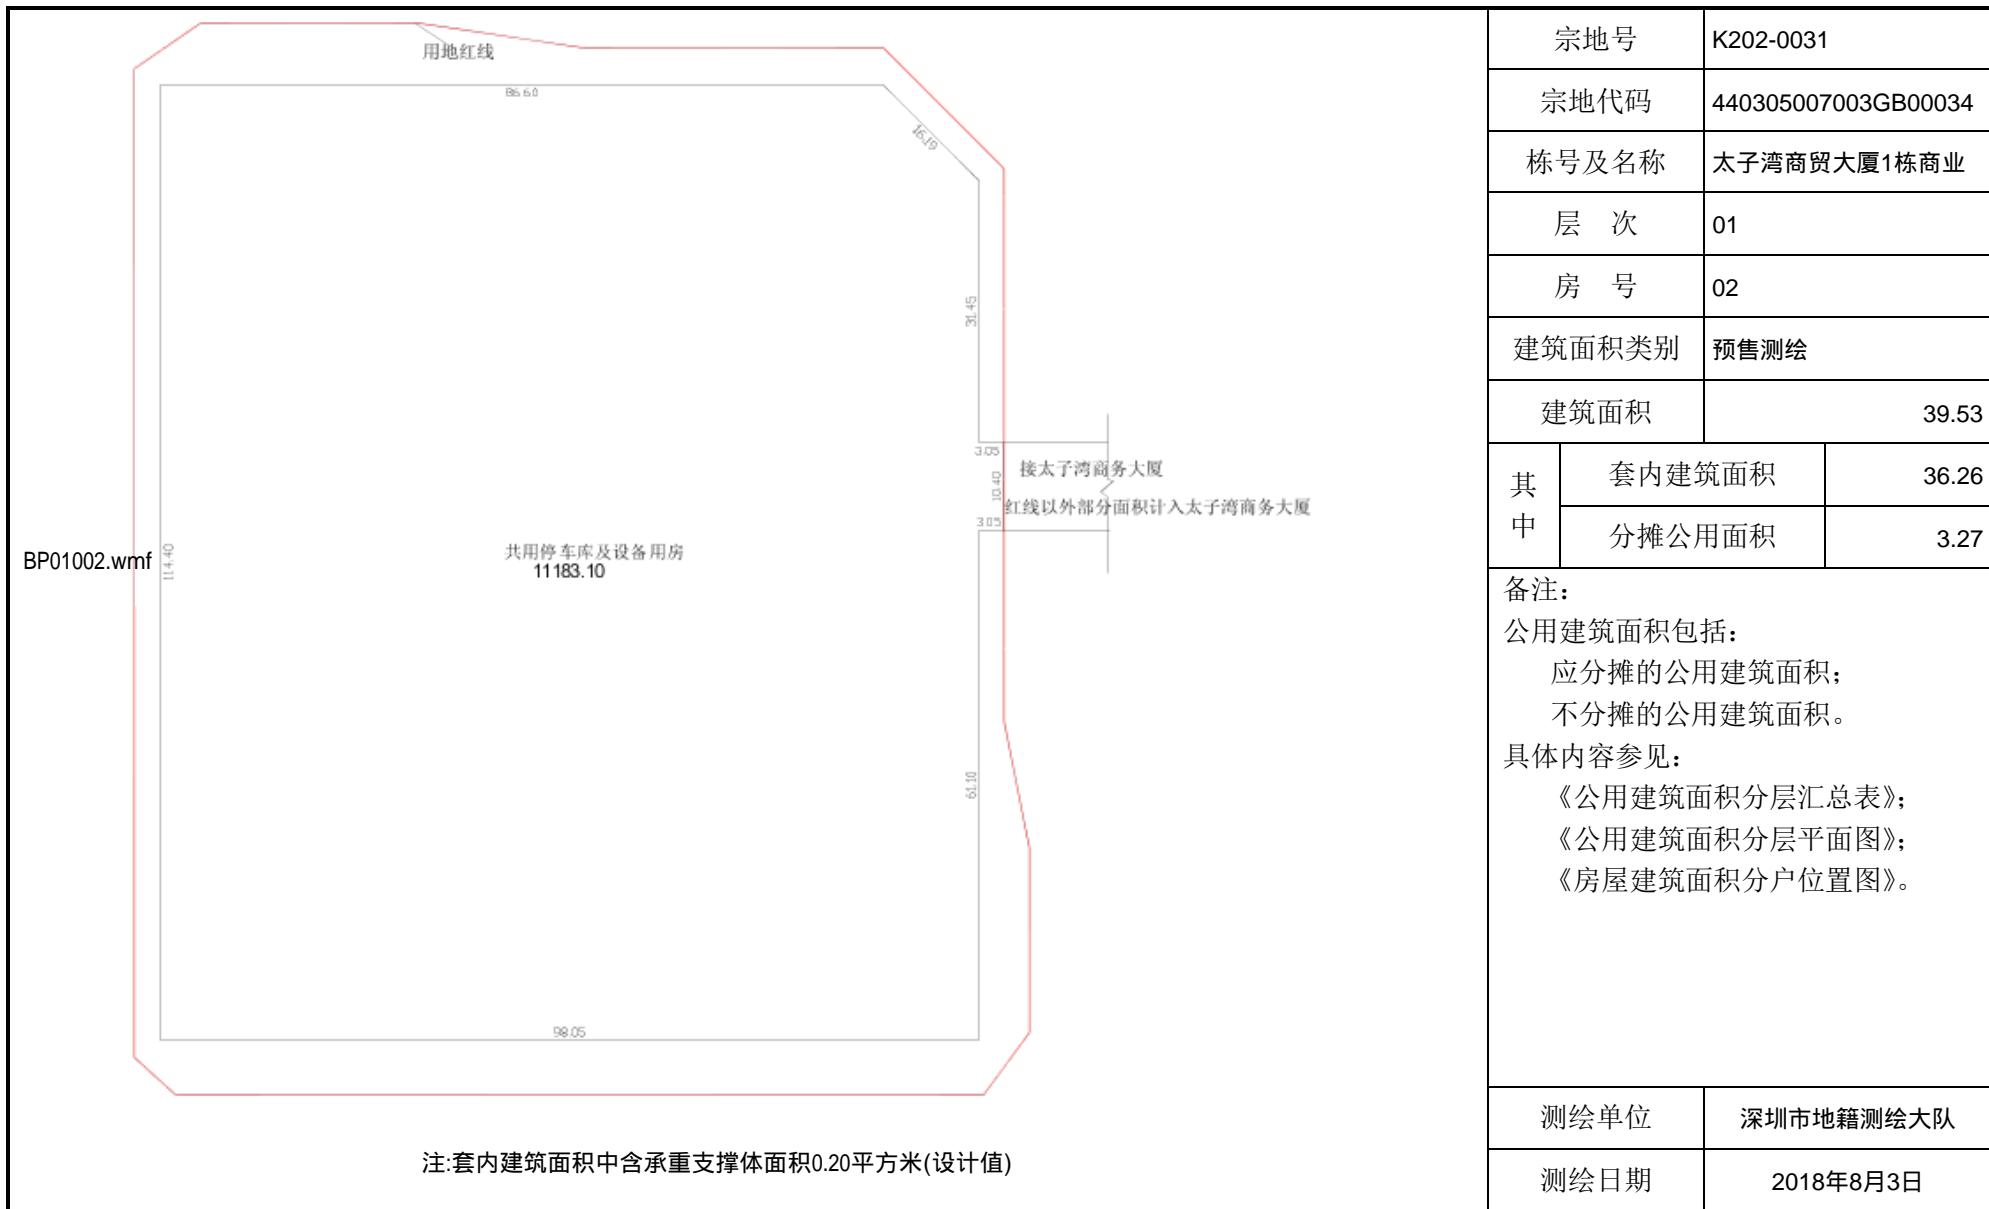


# 房屋建筑面积分户平面图

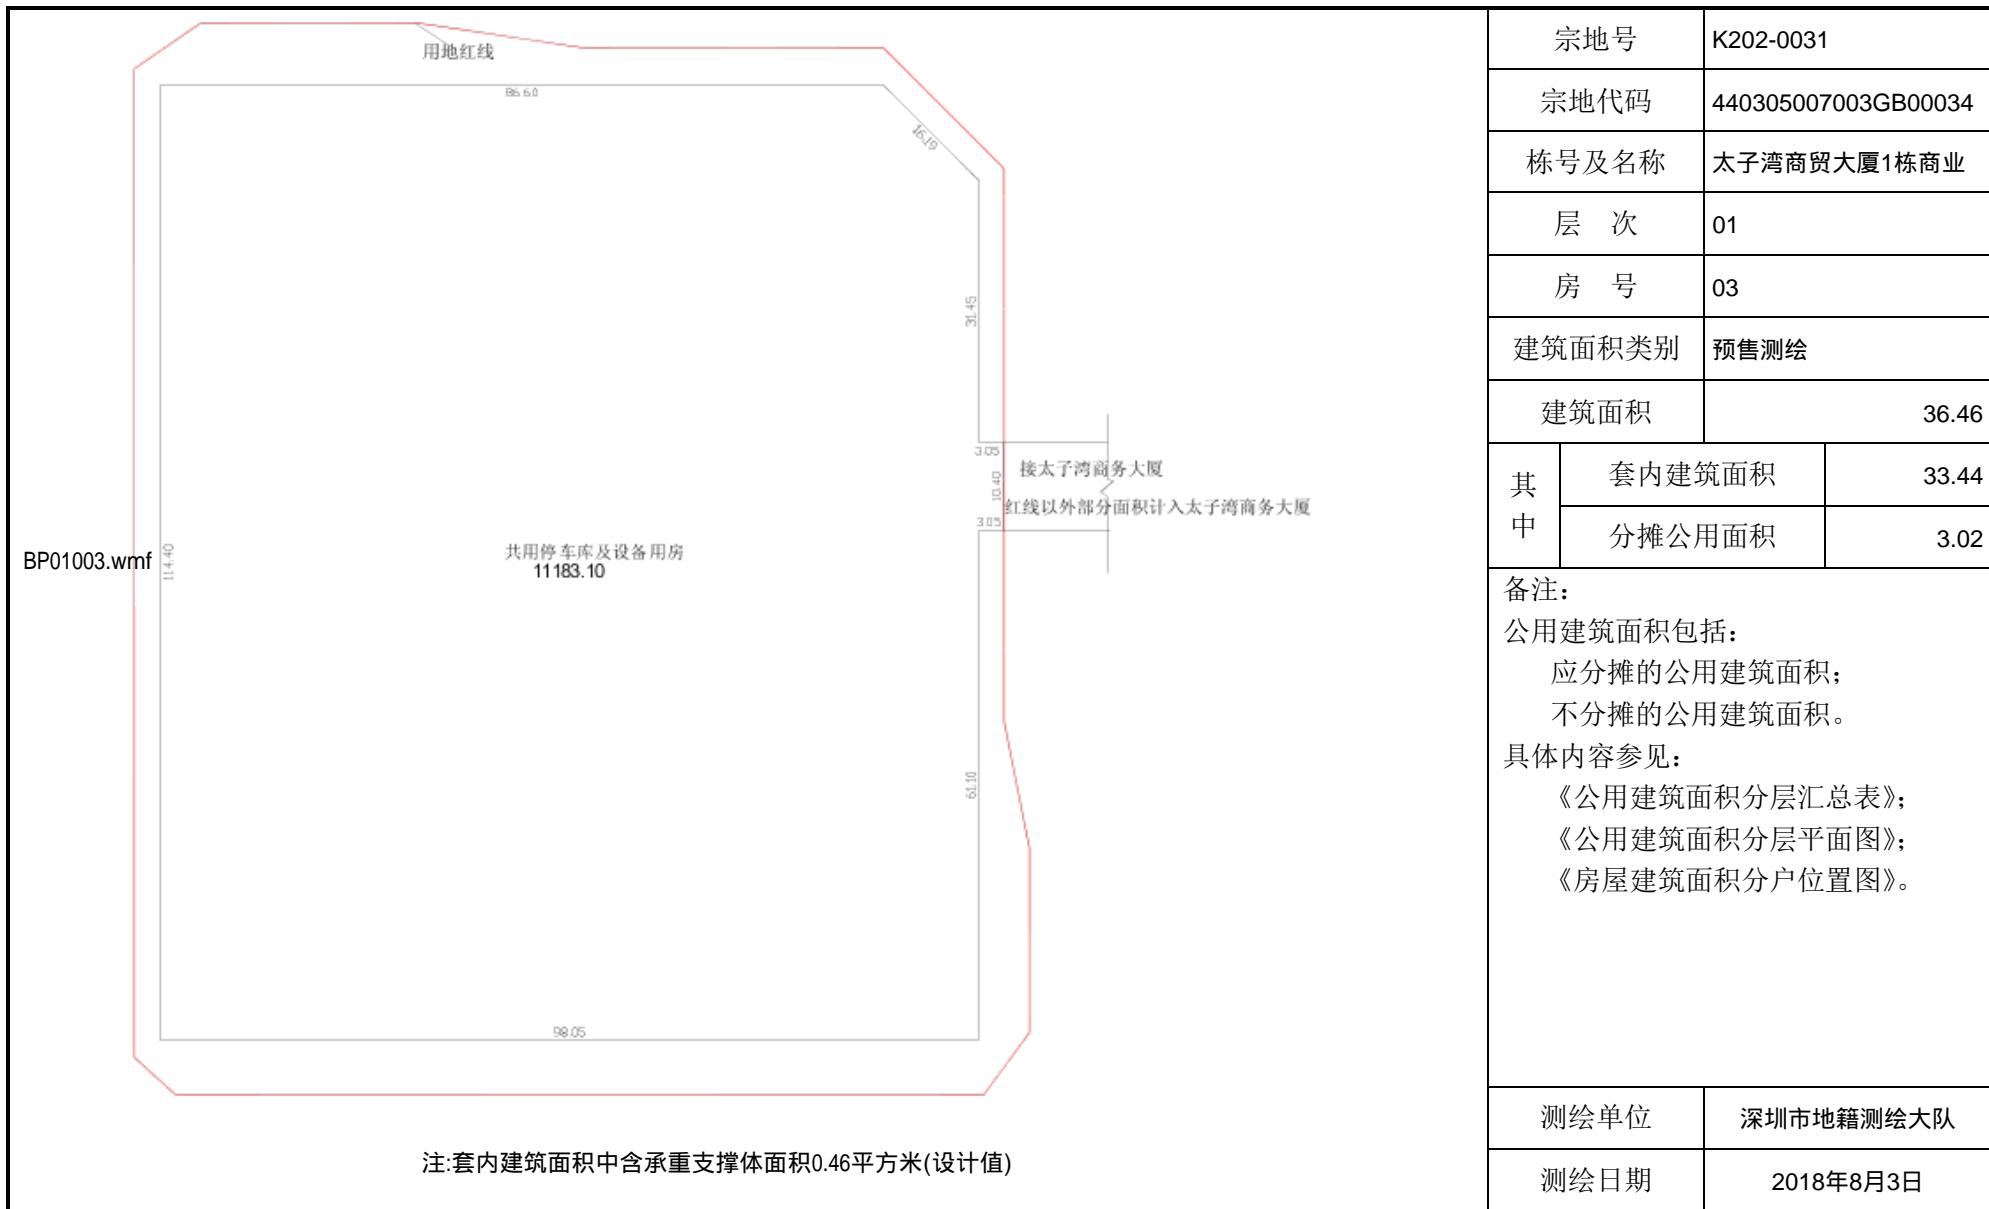


# 房屋建筑面积分户平面图

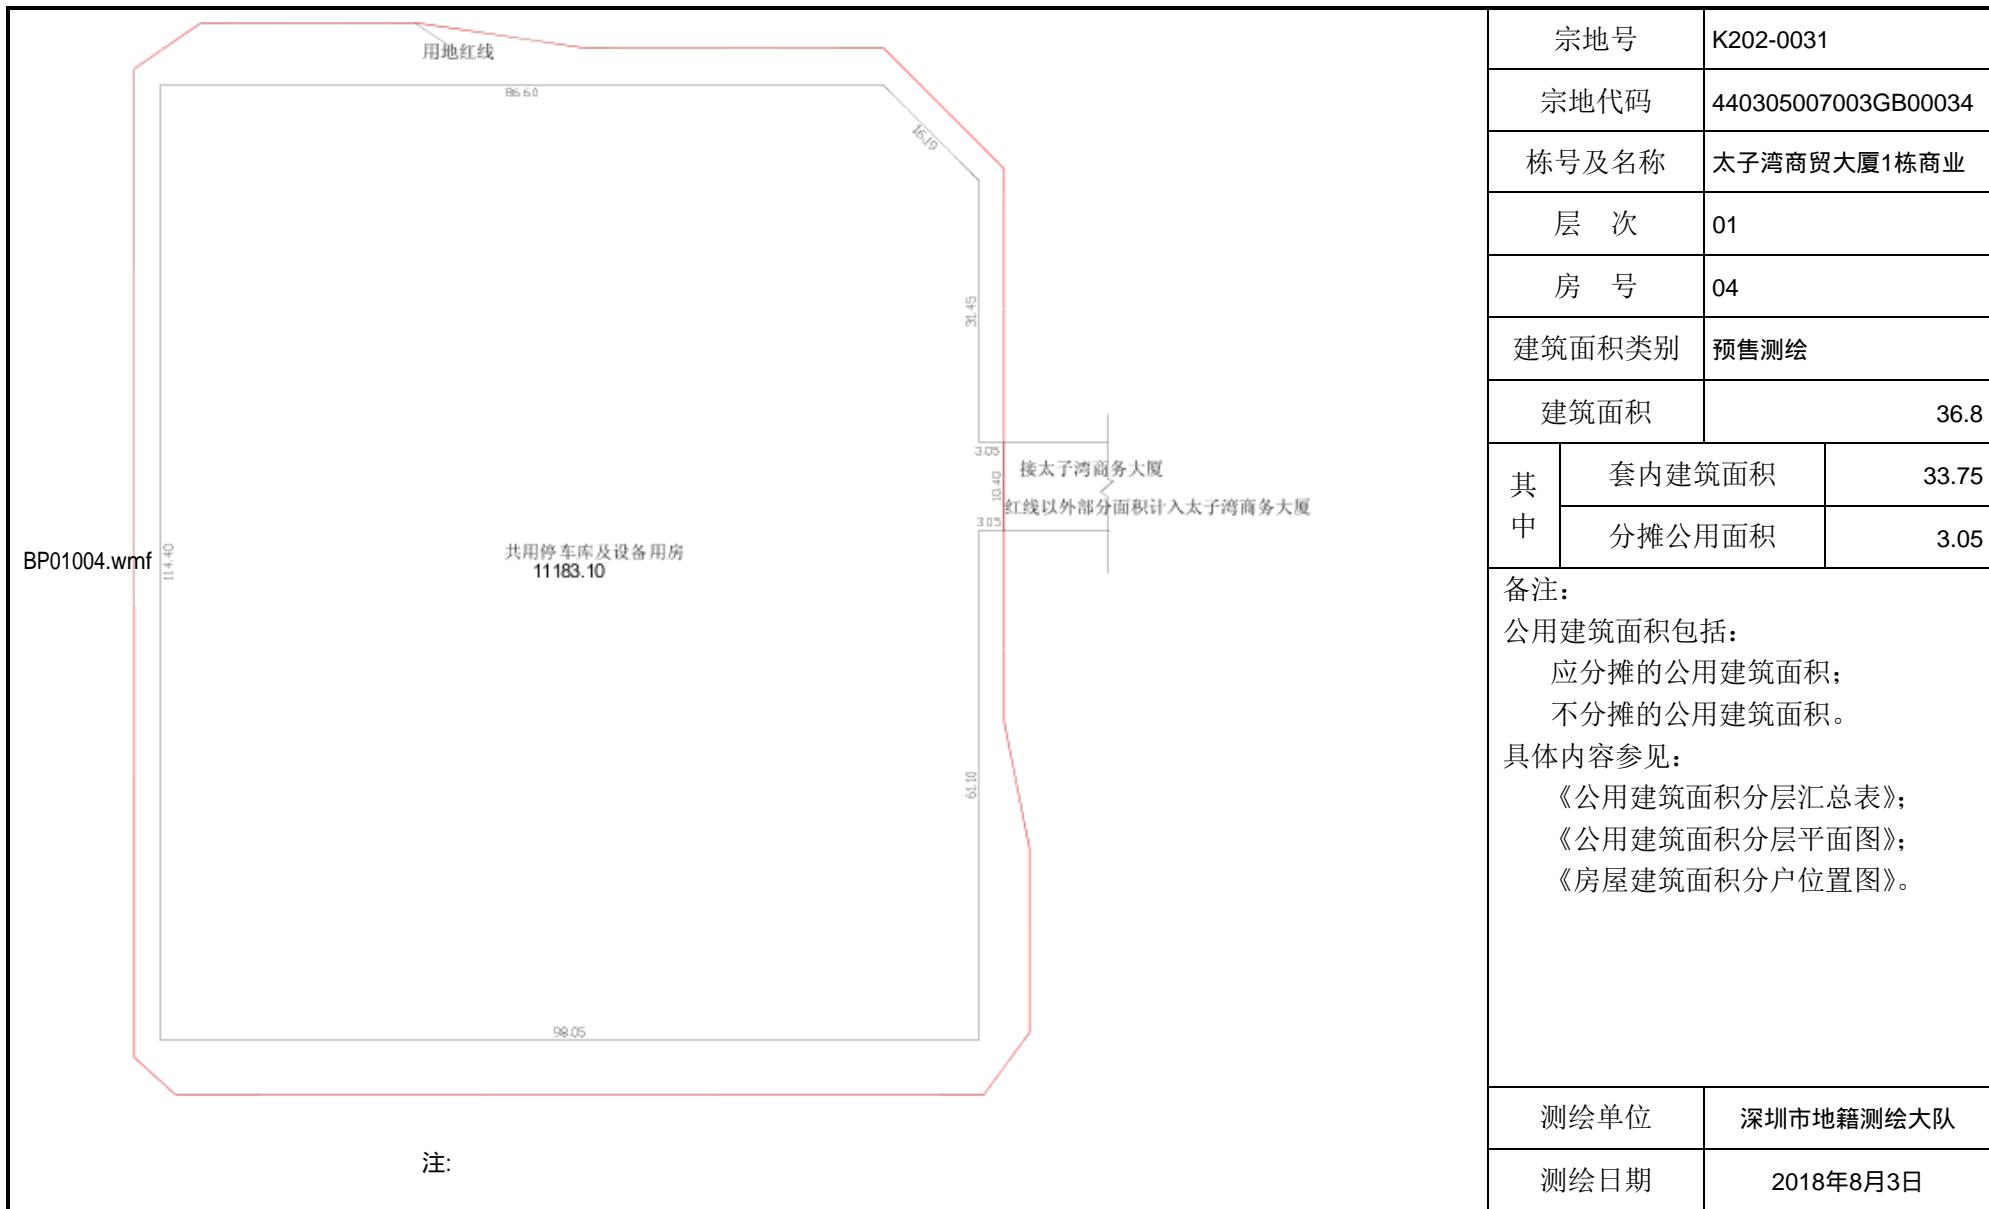


# 房屋建筑面积分户平面图

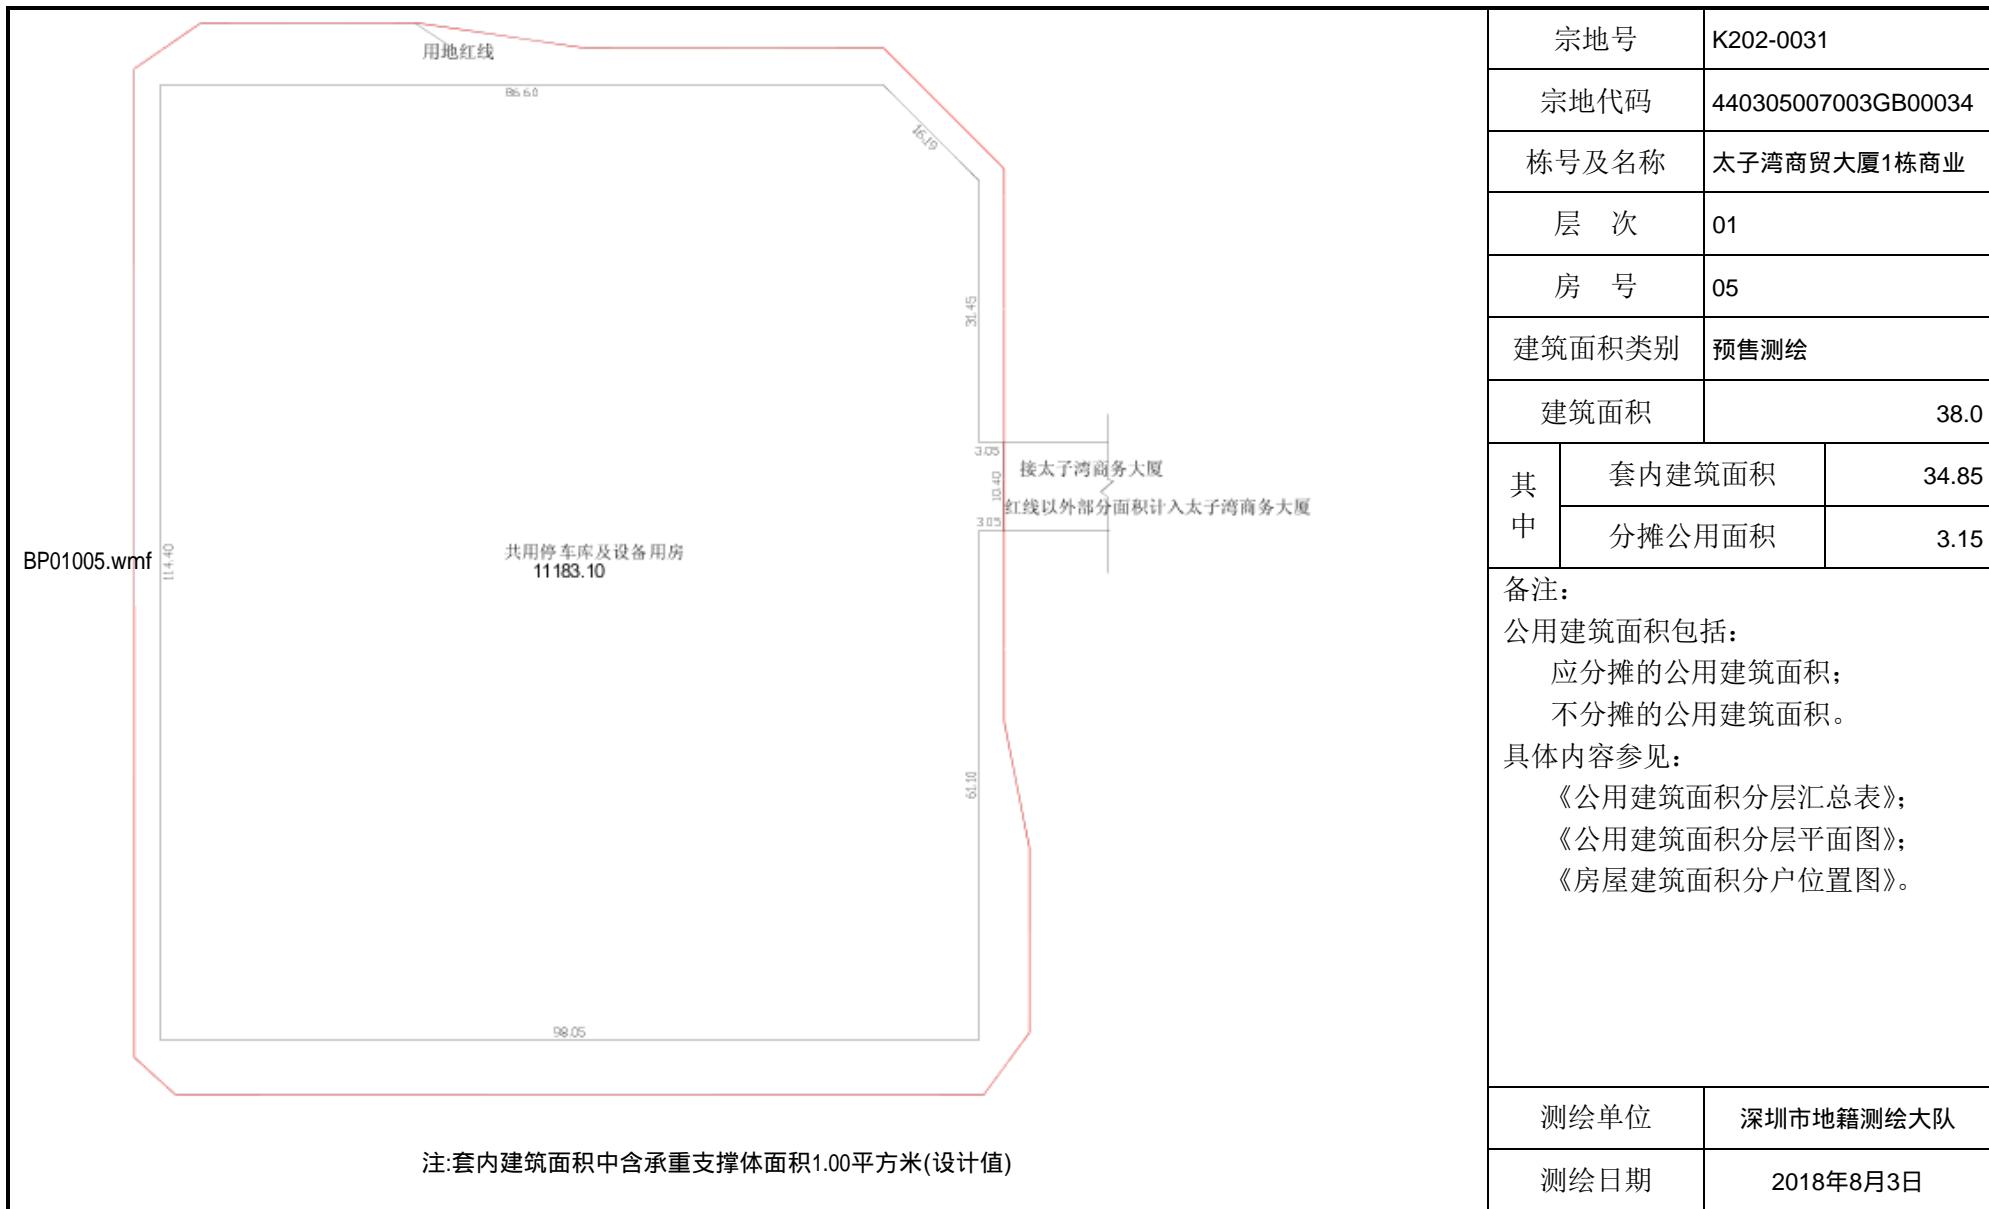


# 房屋建筑面积分户平面图

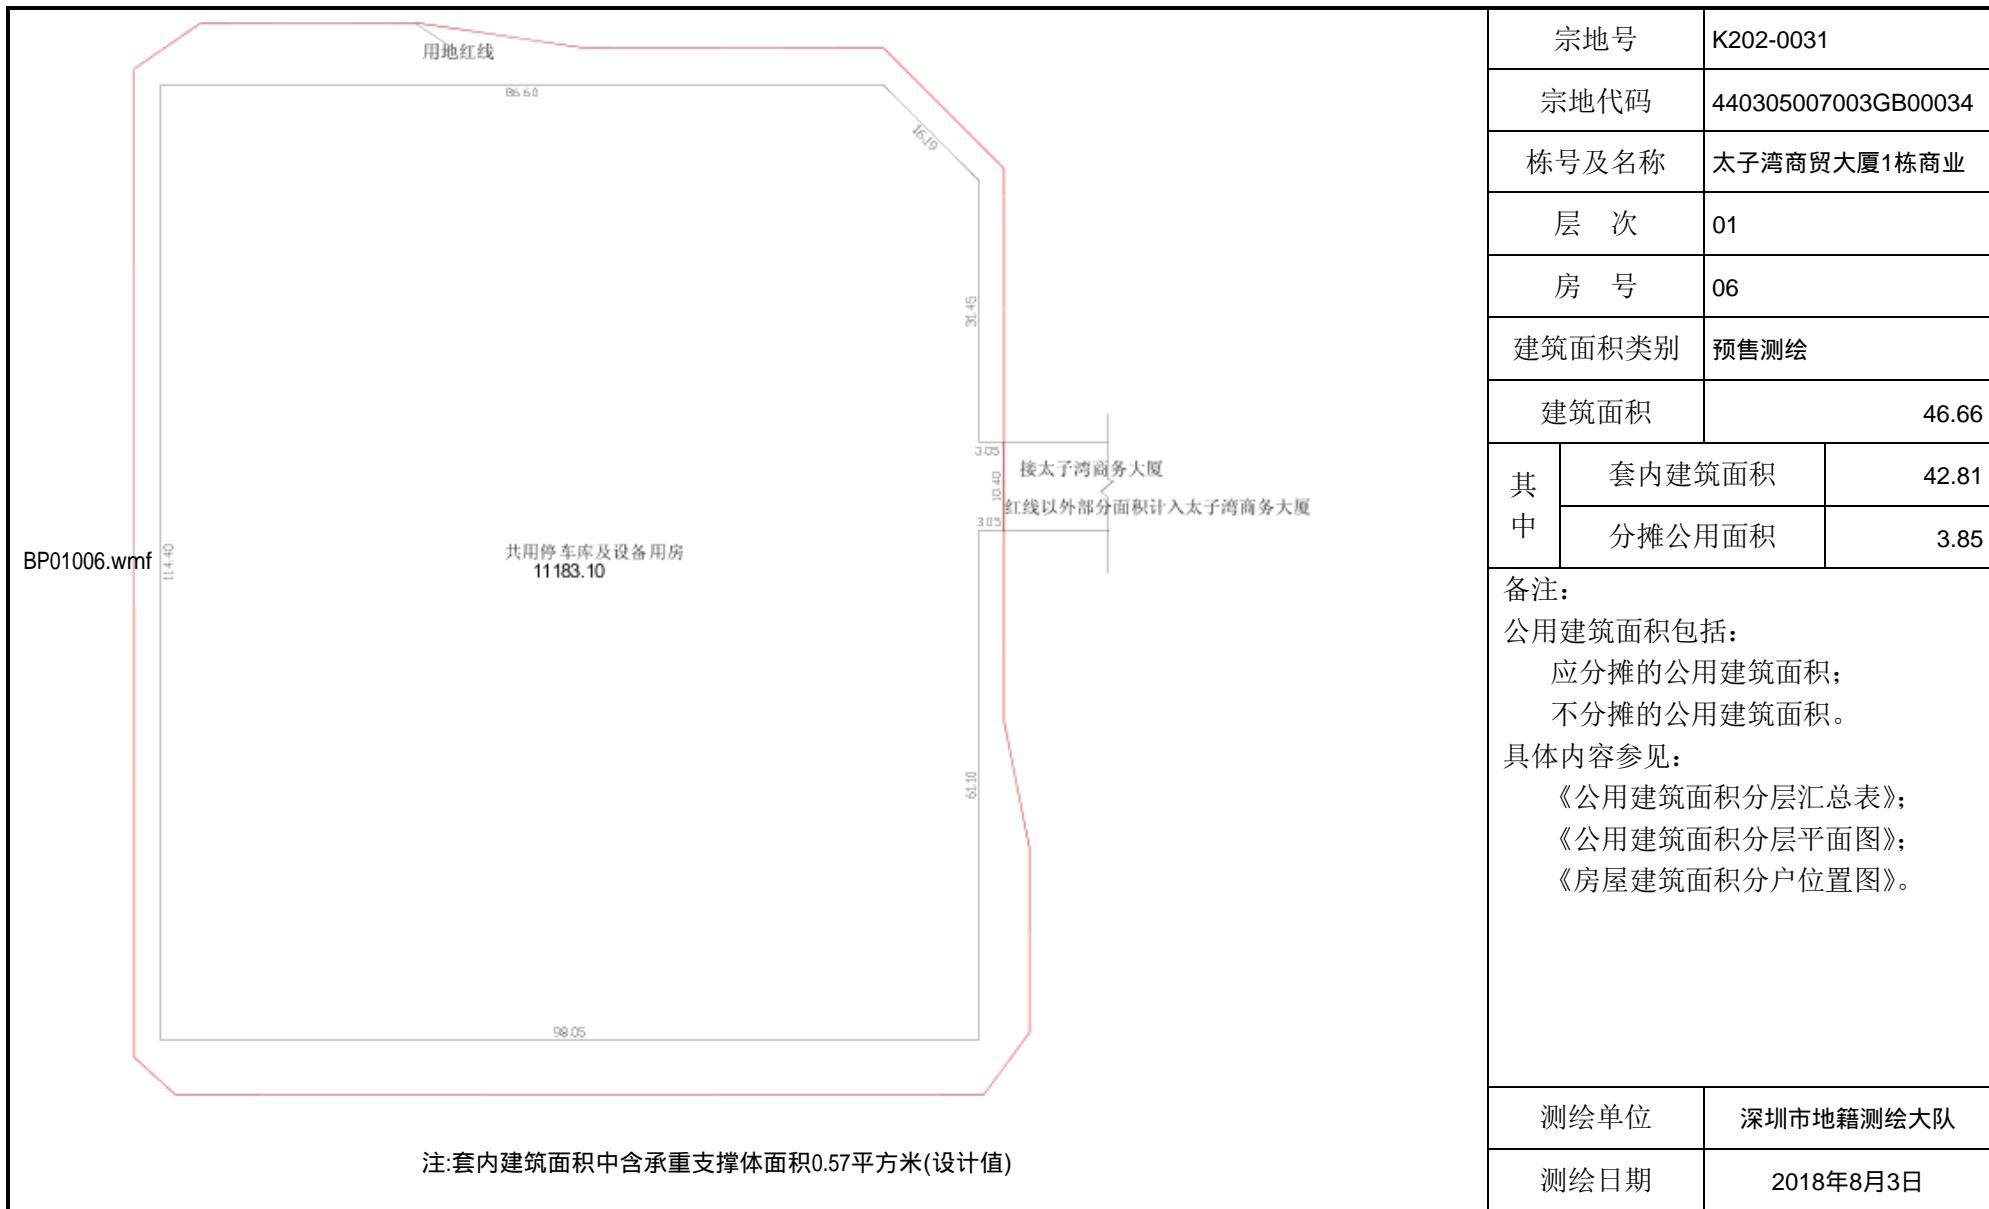


# 房屋建筑面积分户平面图

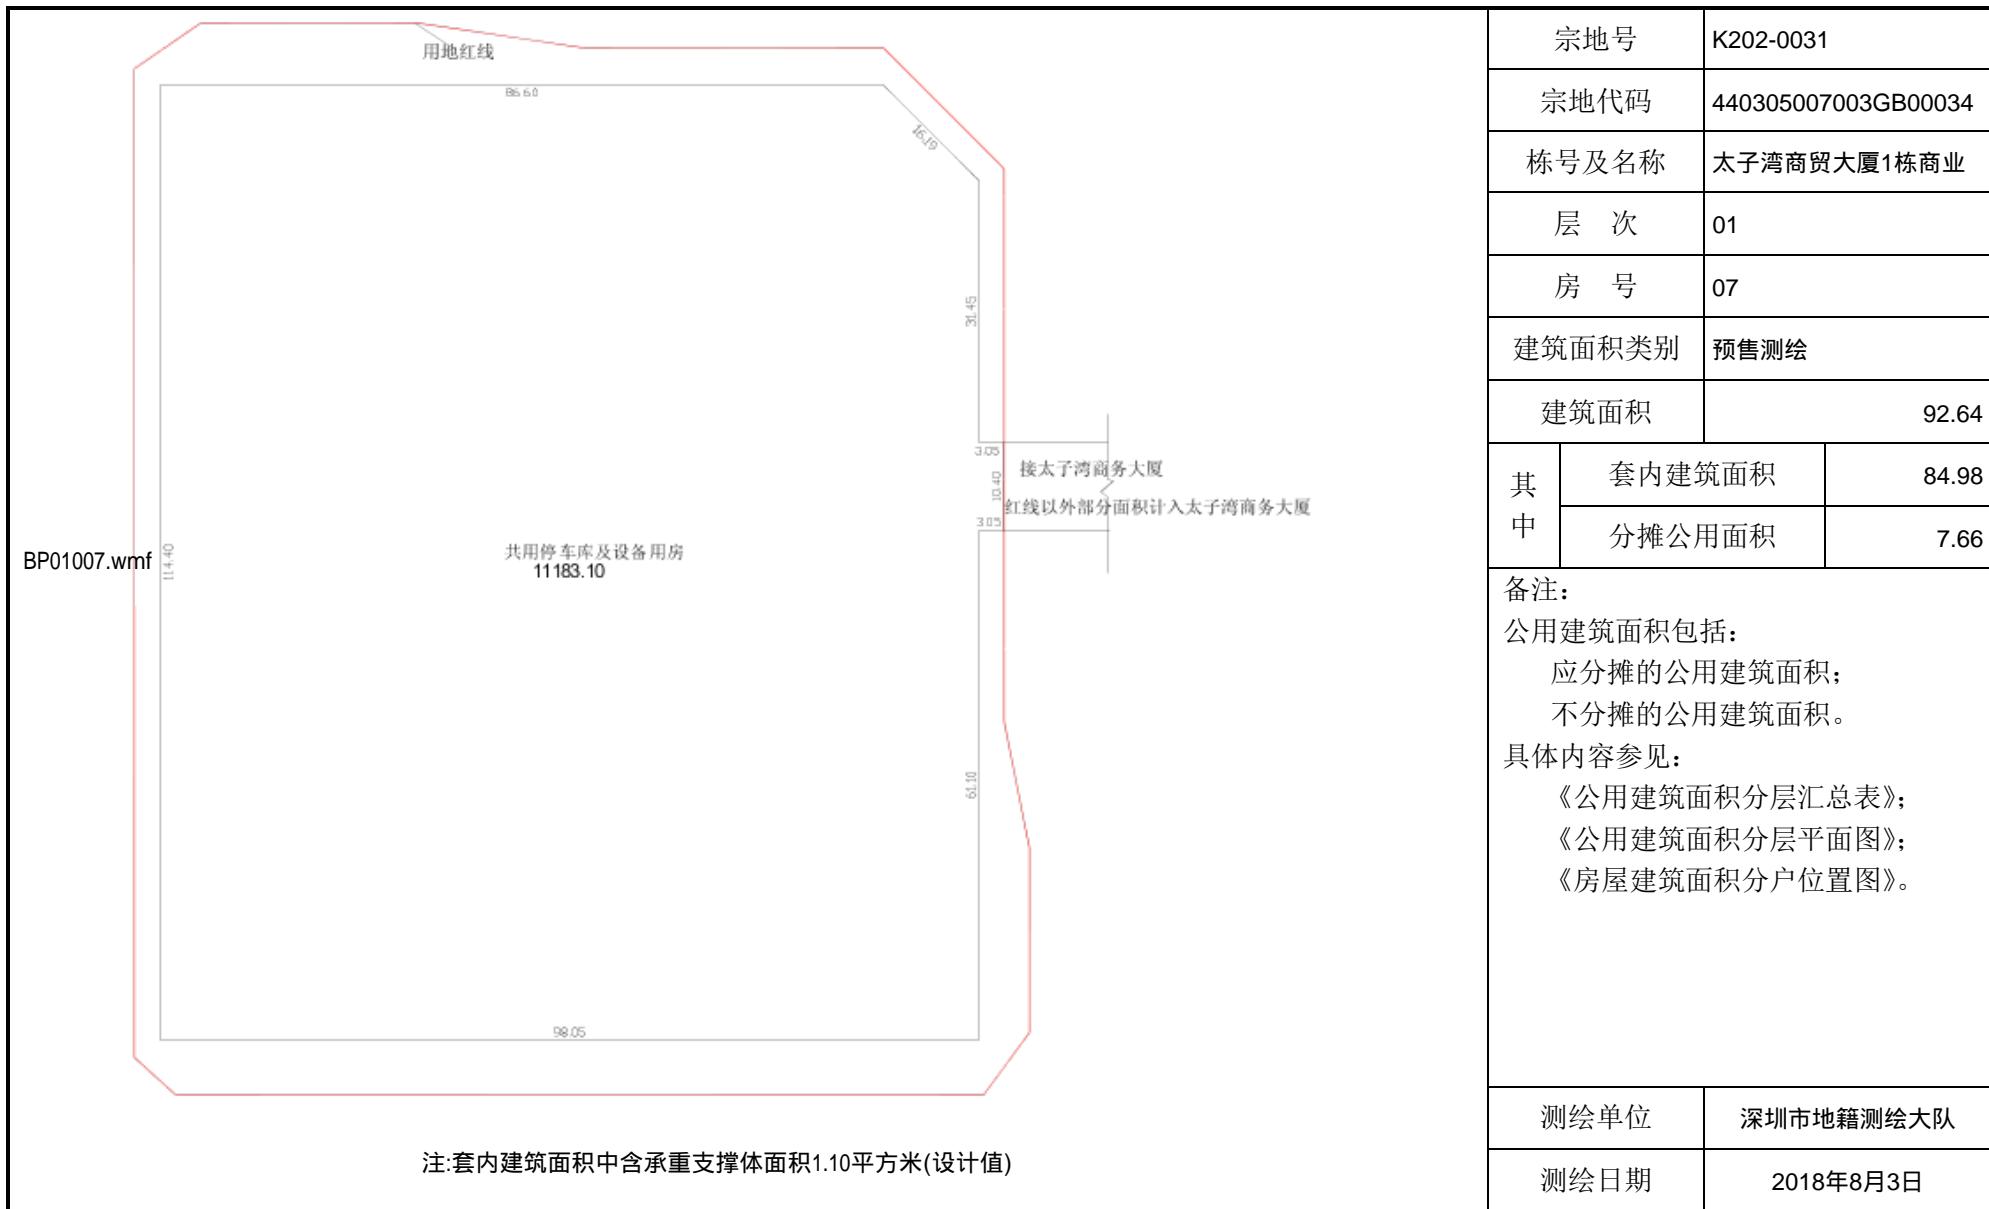


# 房屋建筑面积分户平面图

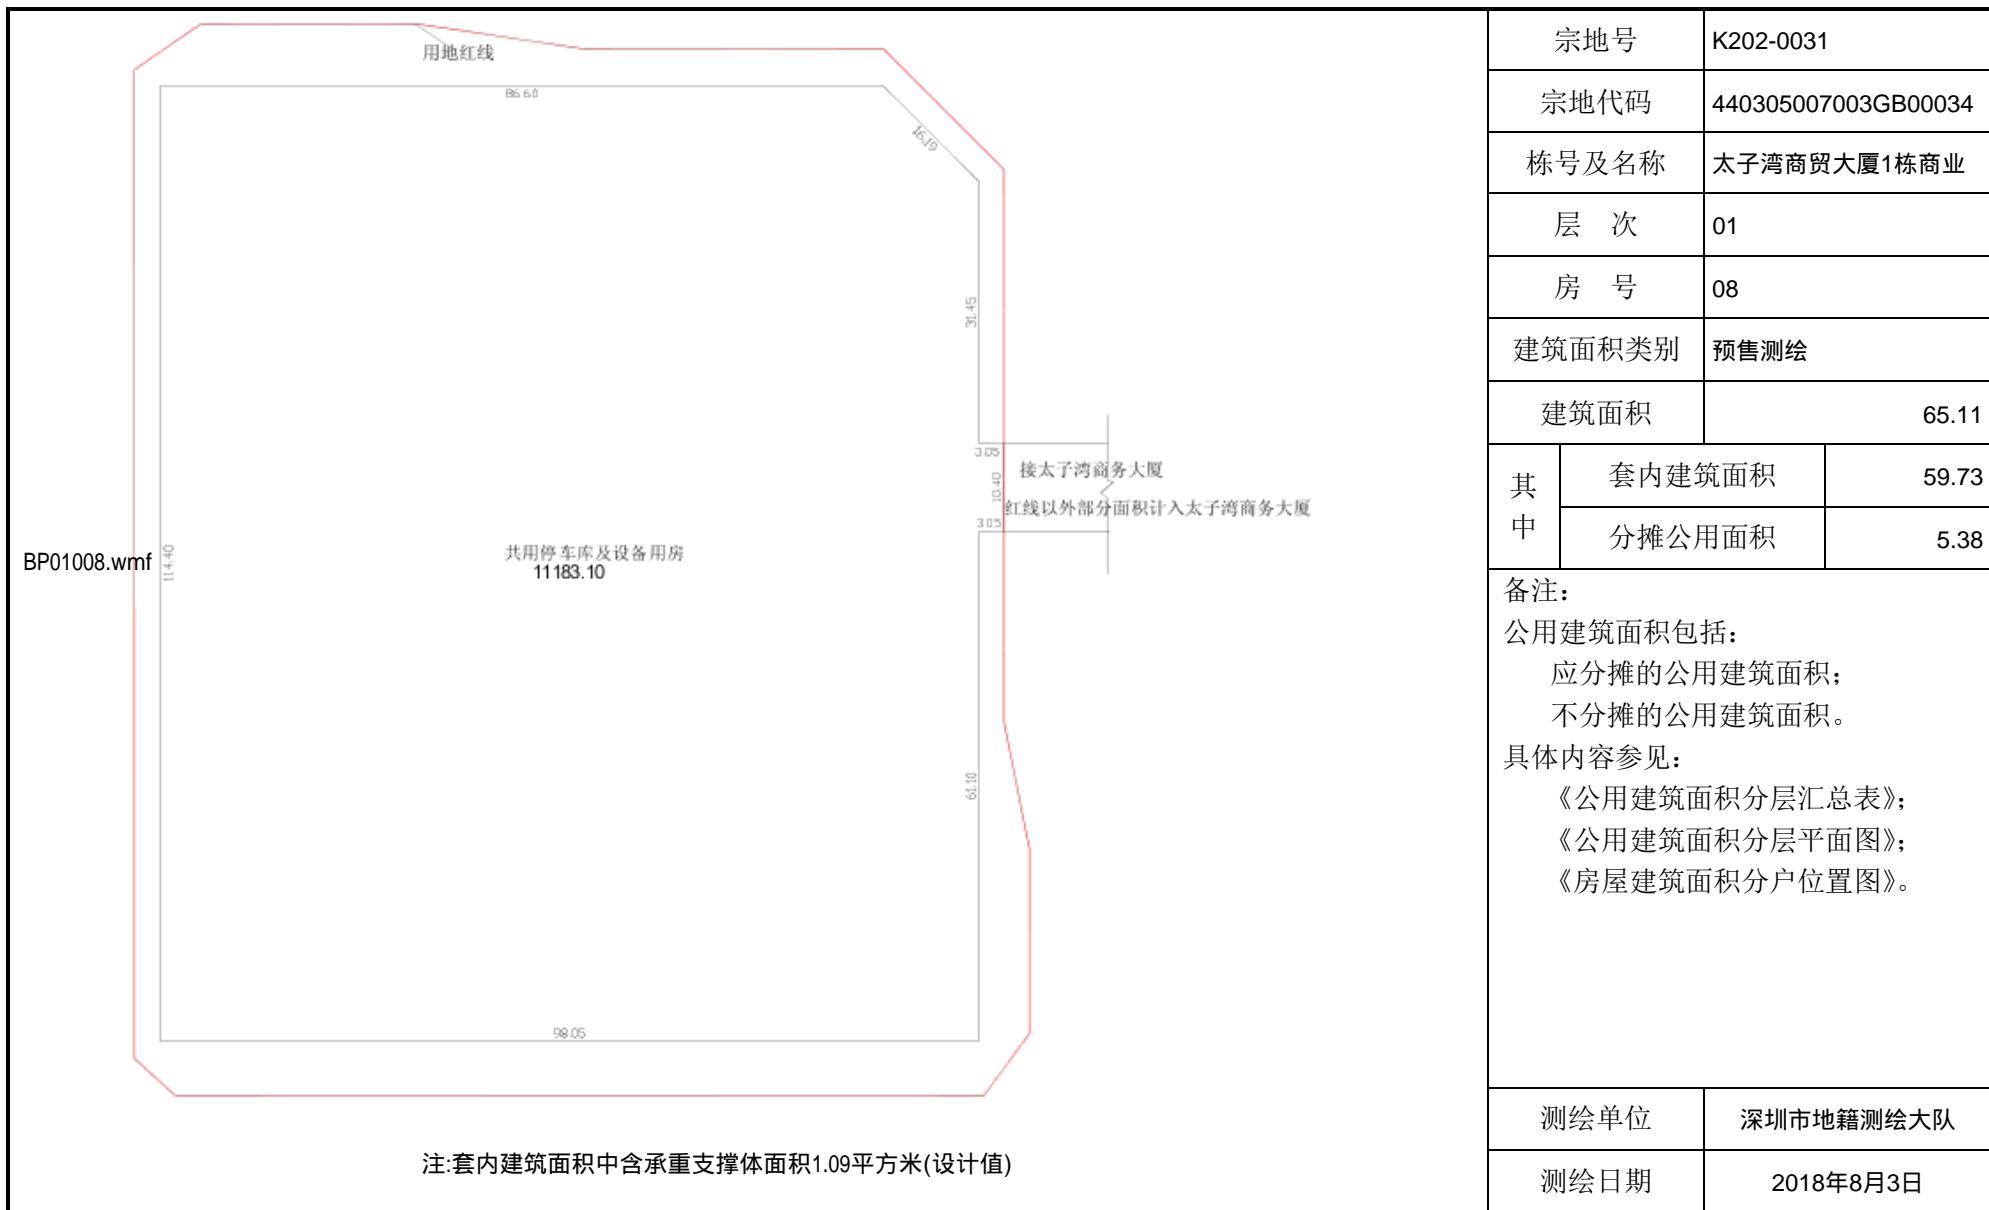


# 房屋建筑面积分户平面图

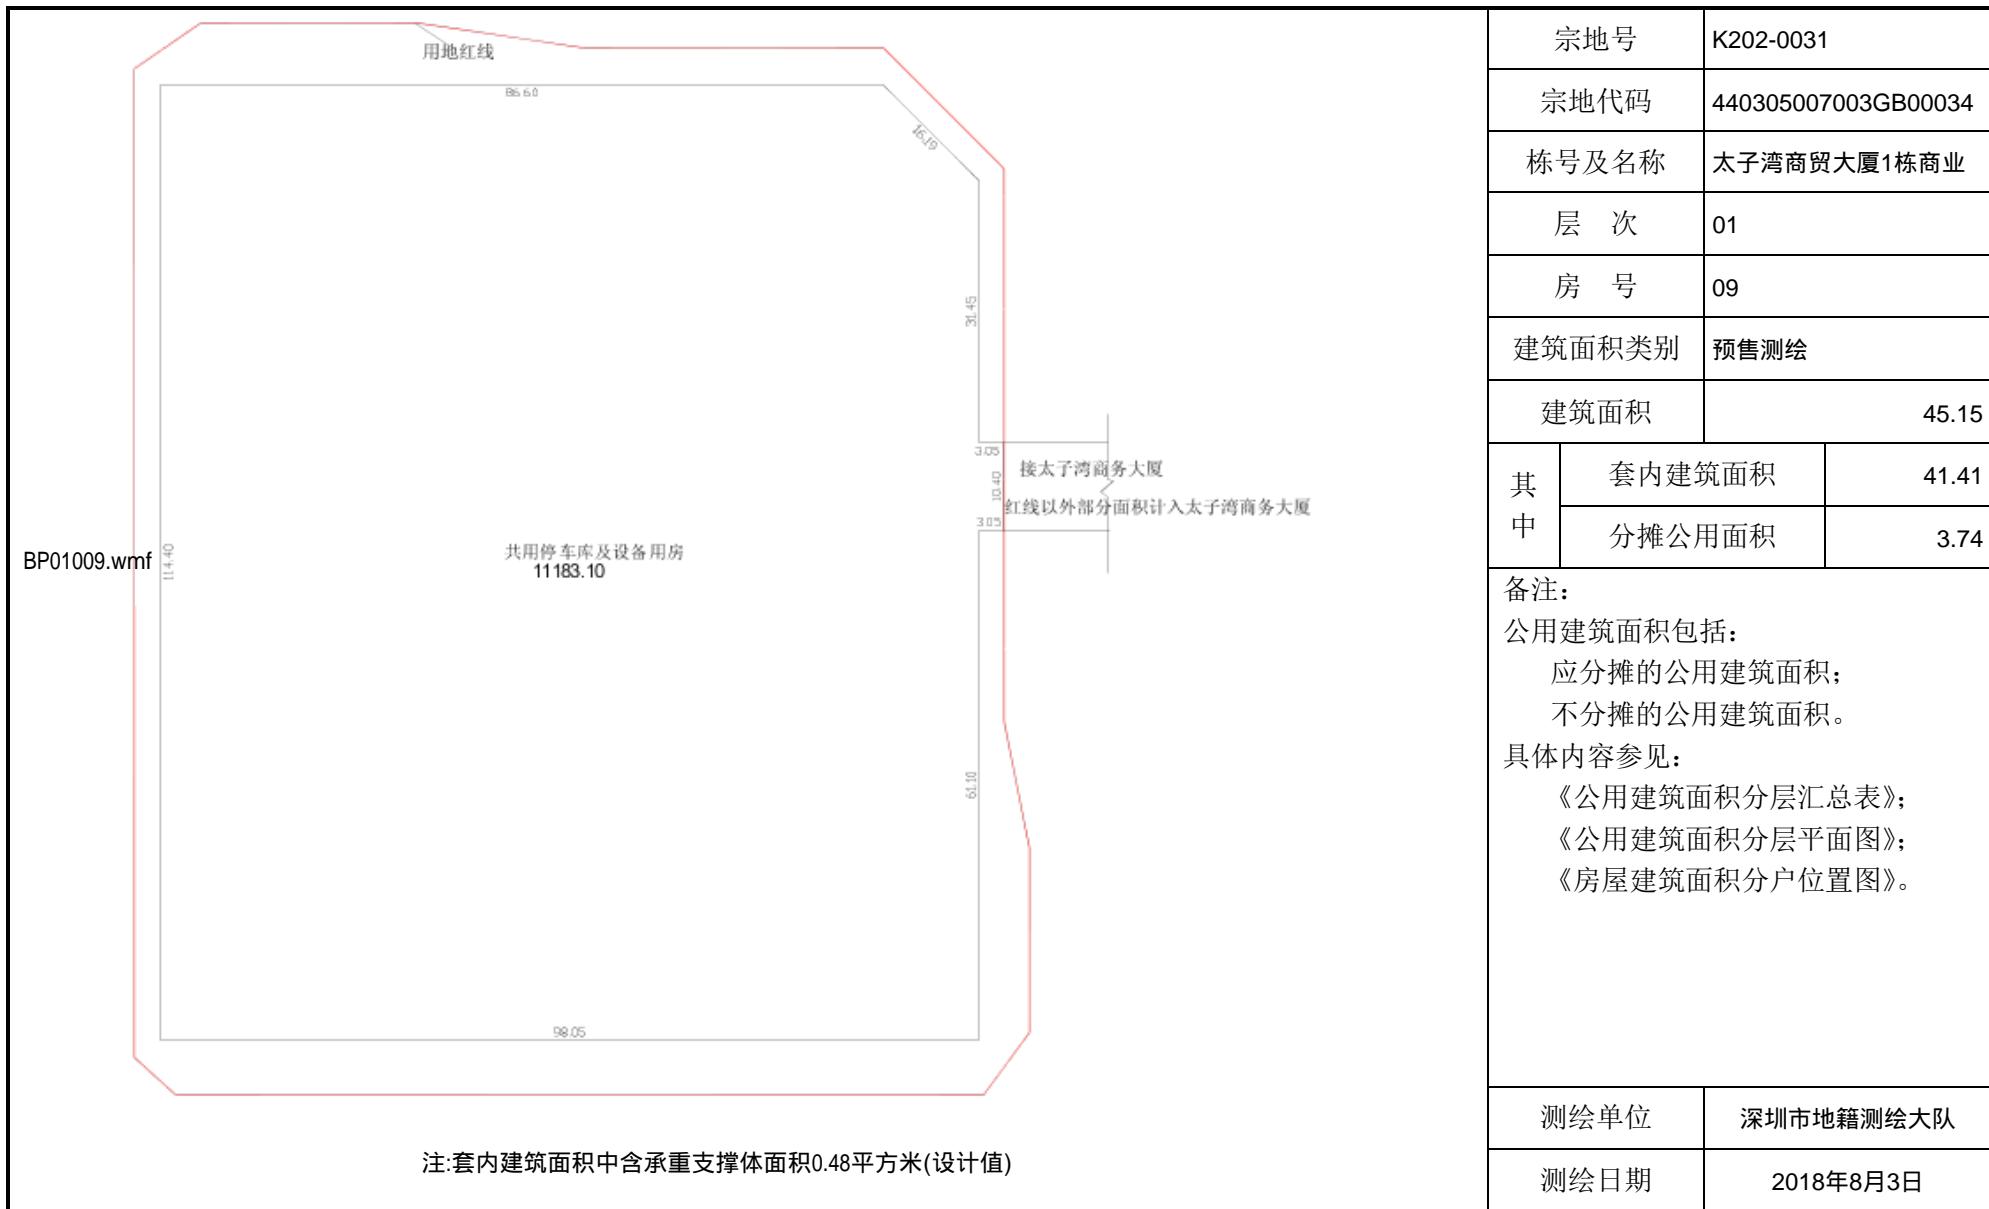


# 房屋建筑面积分户平面图

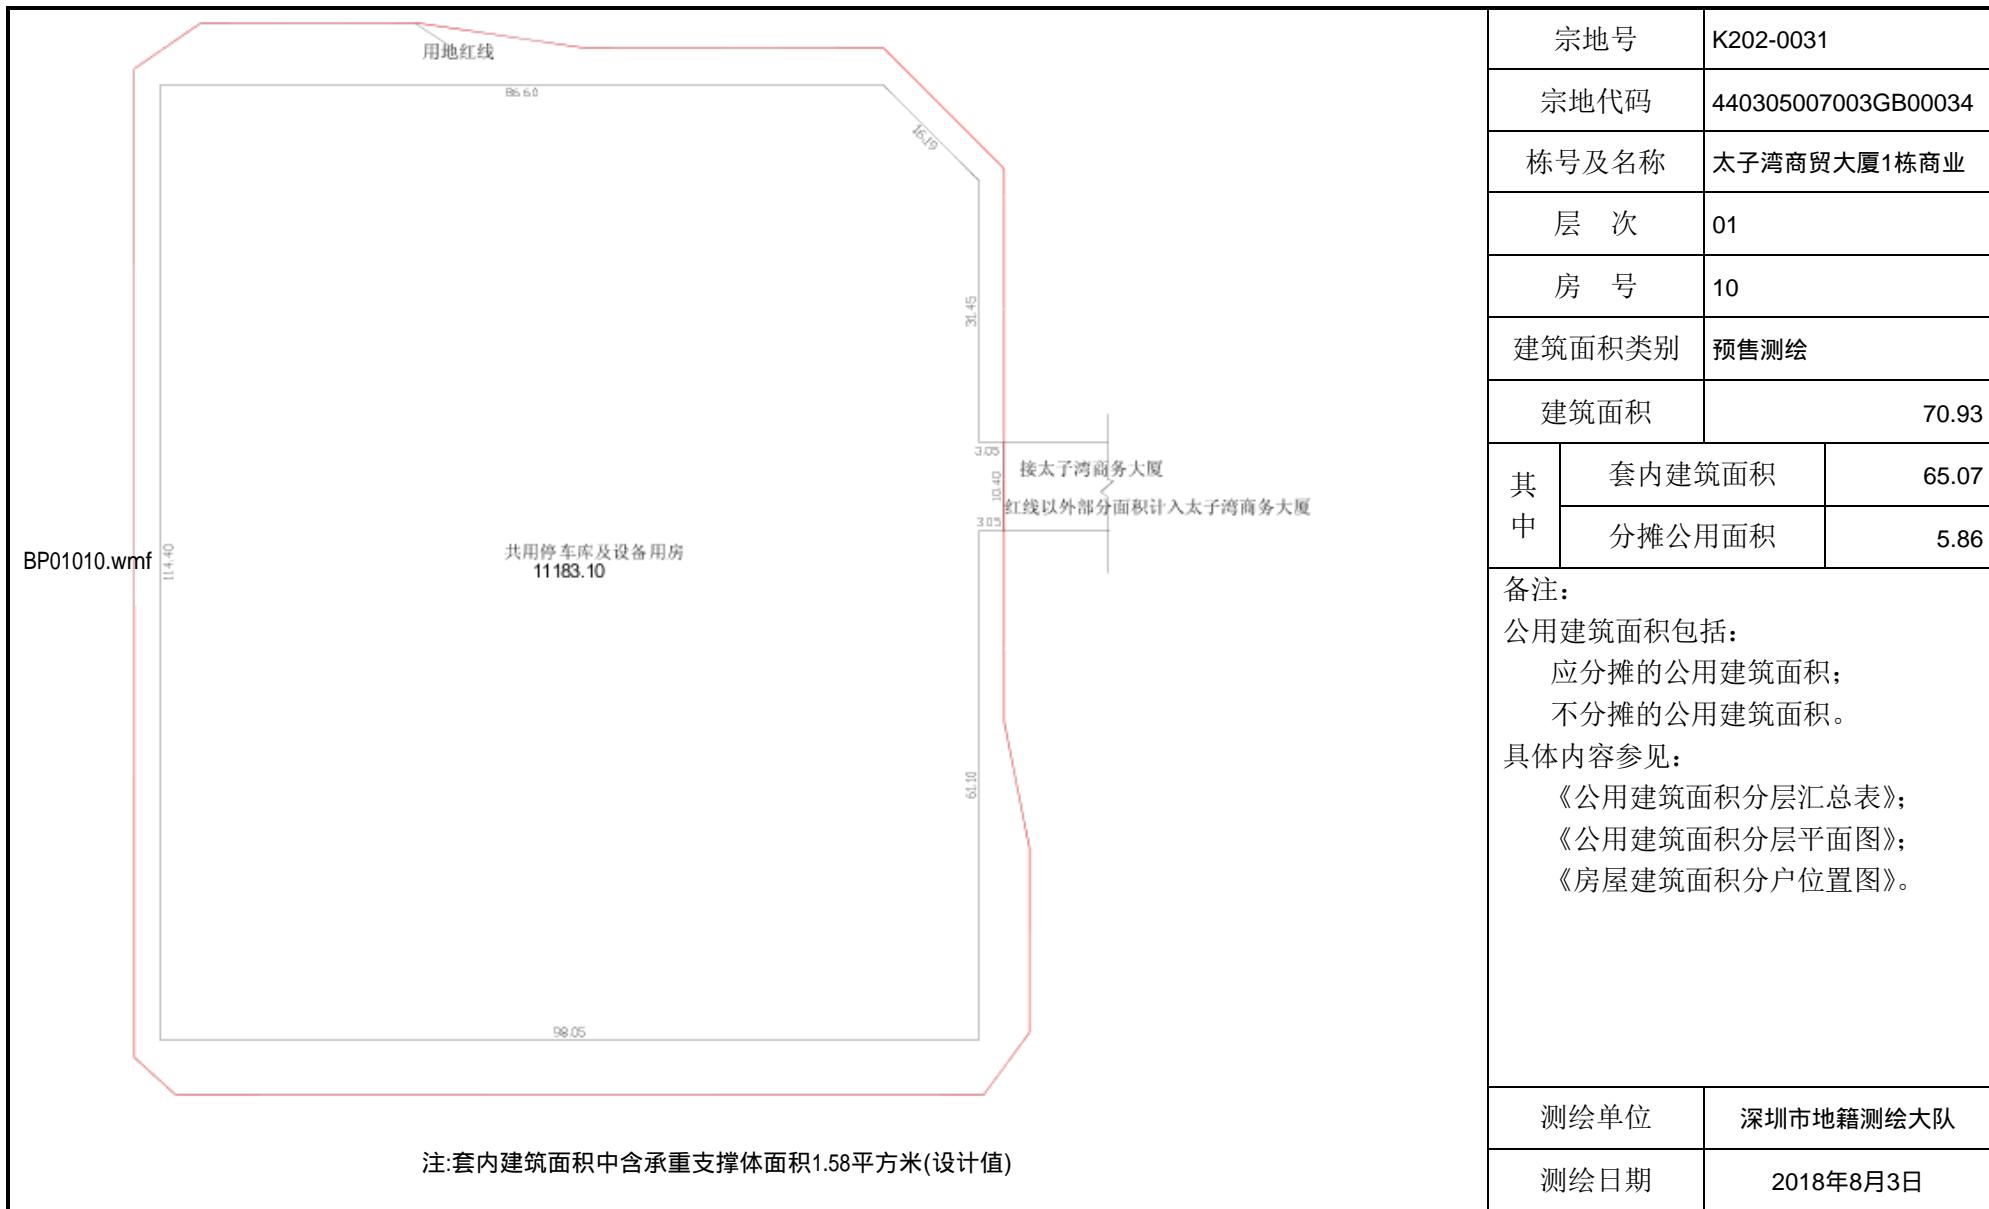


# 房屋建筑面积分户平面图

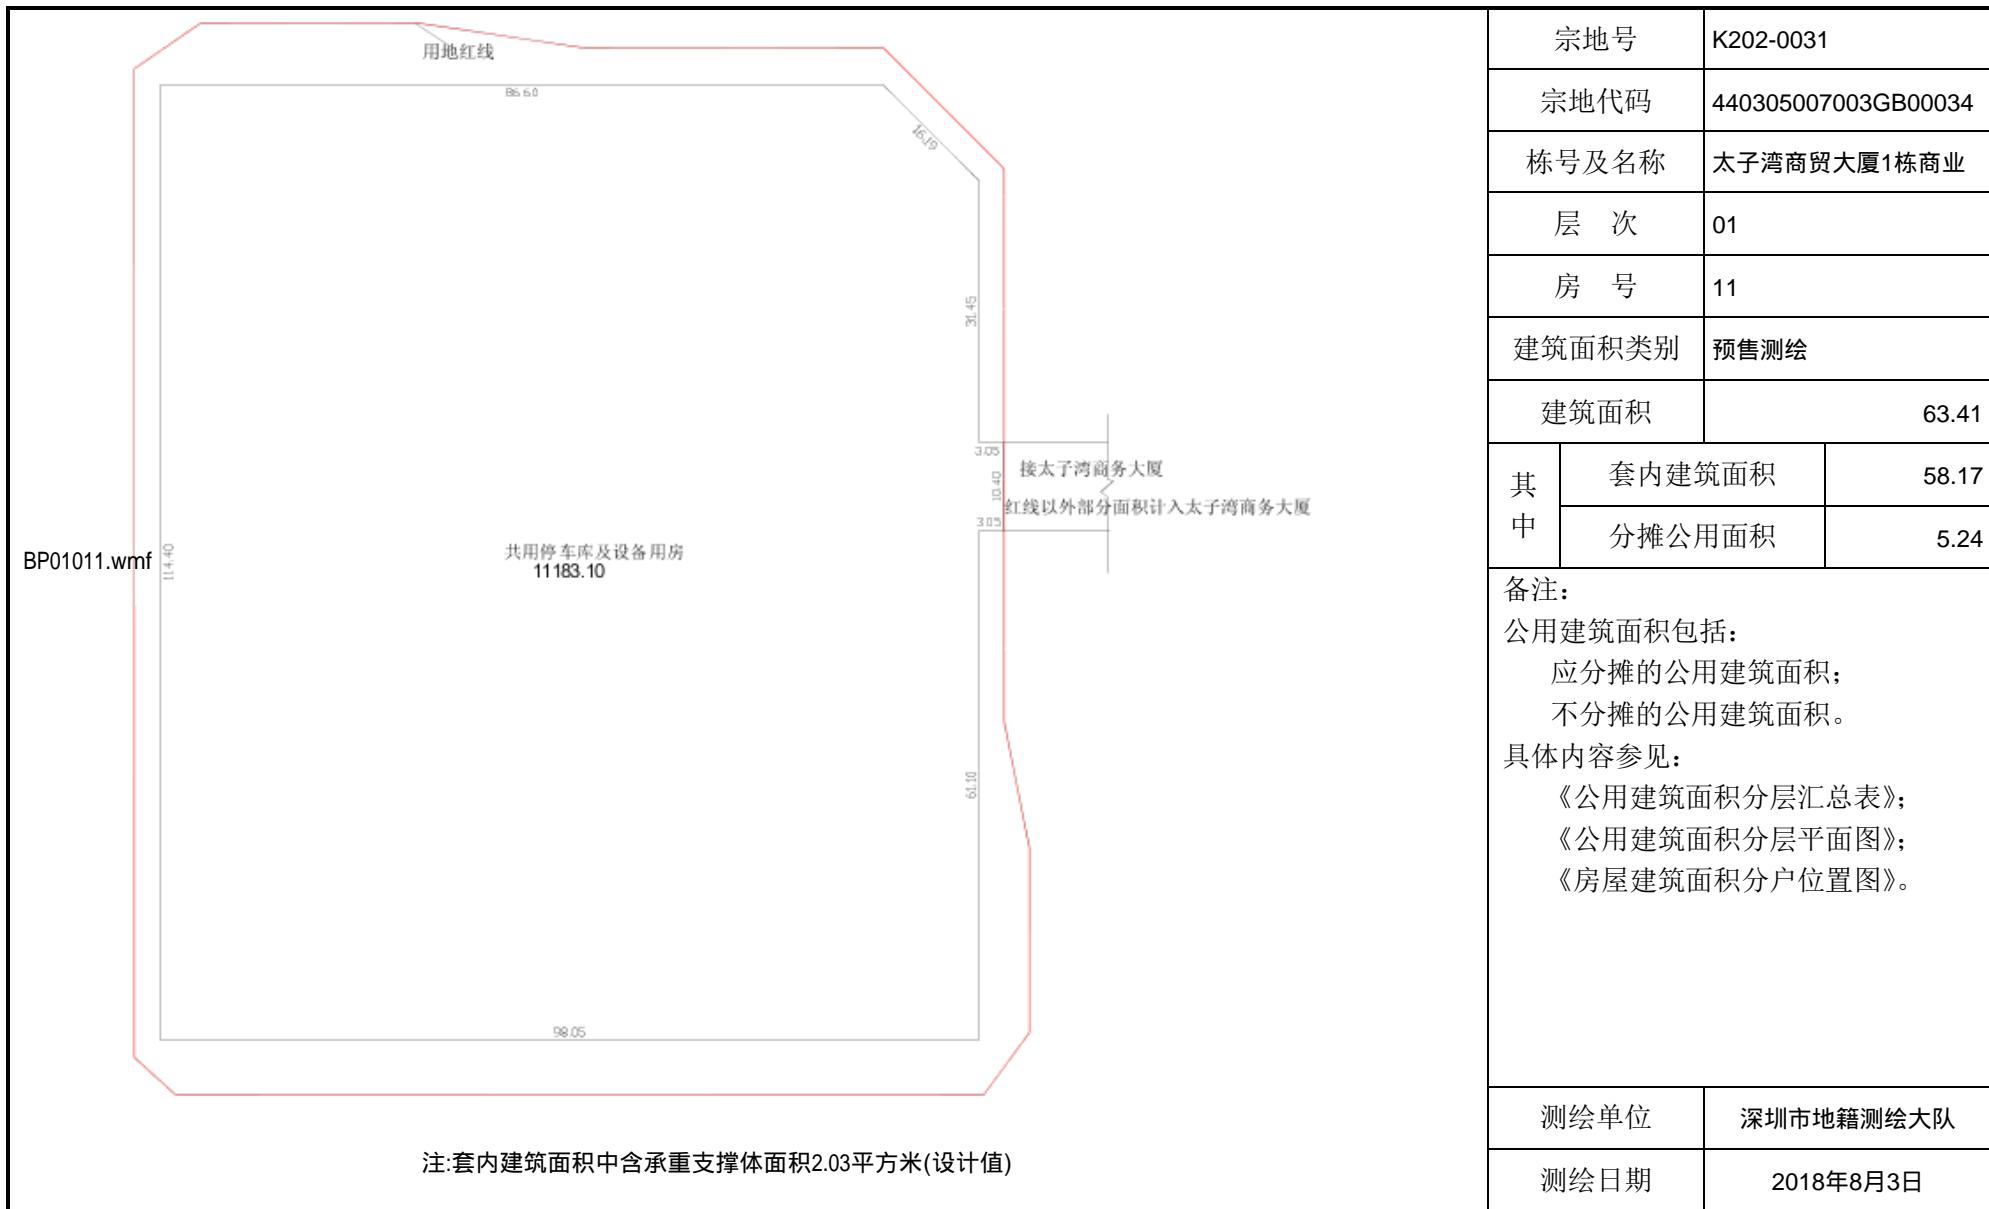


# 房屋建筑面积分户平面图

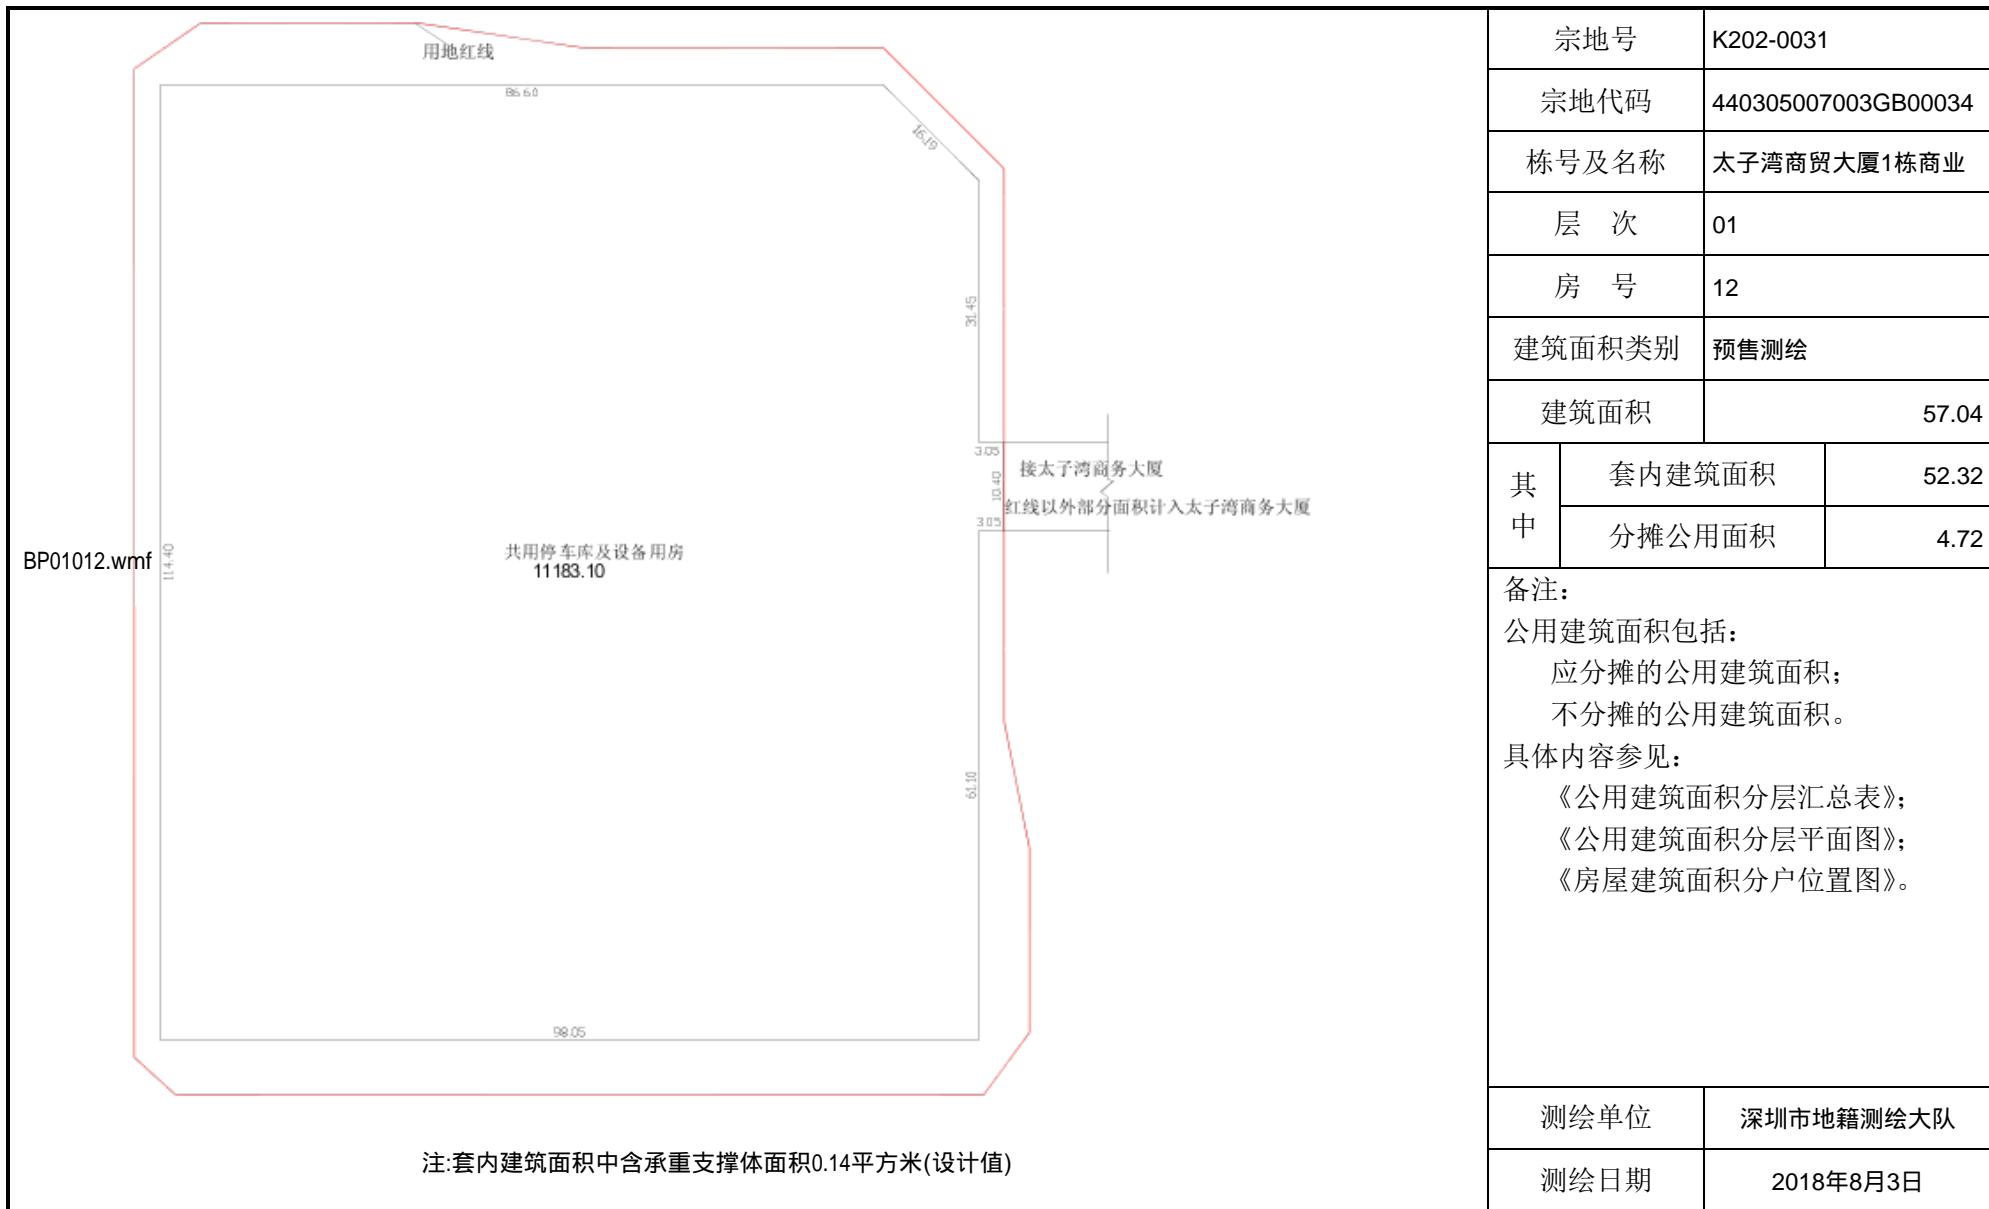


# 房屋建筑面积分户平面图

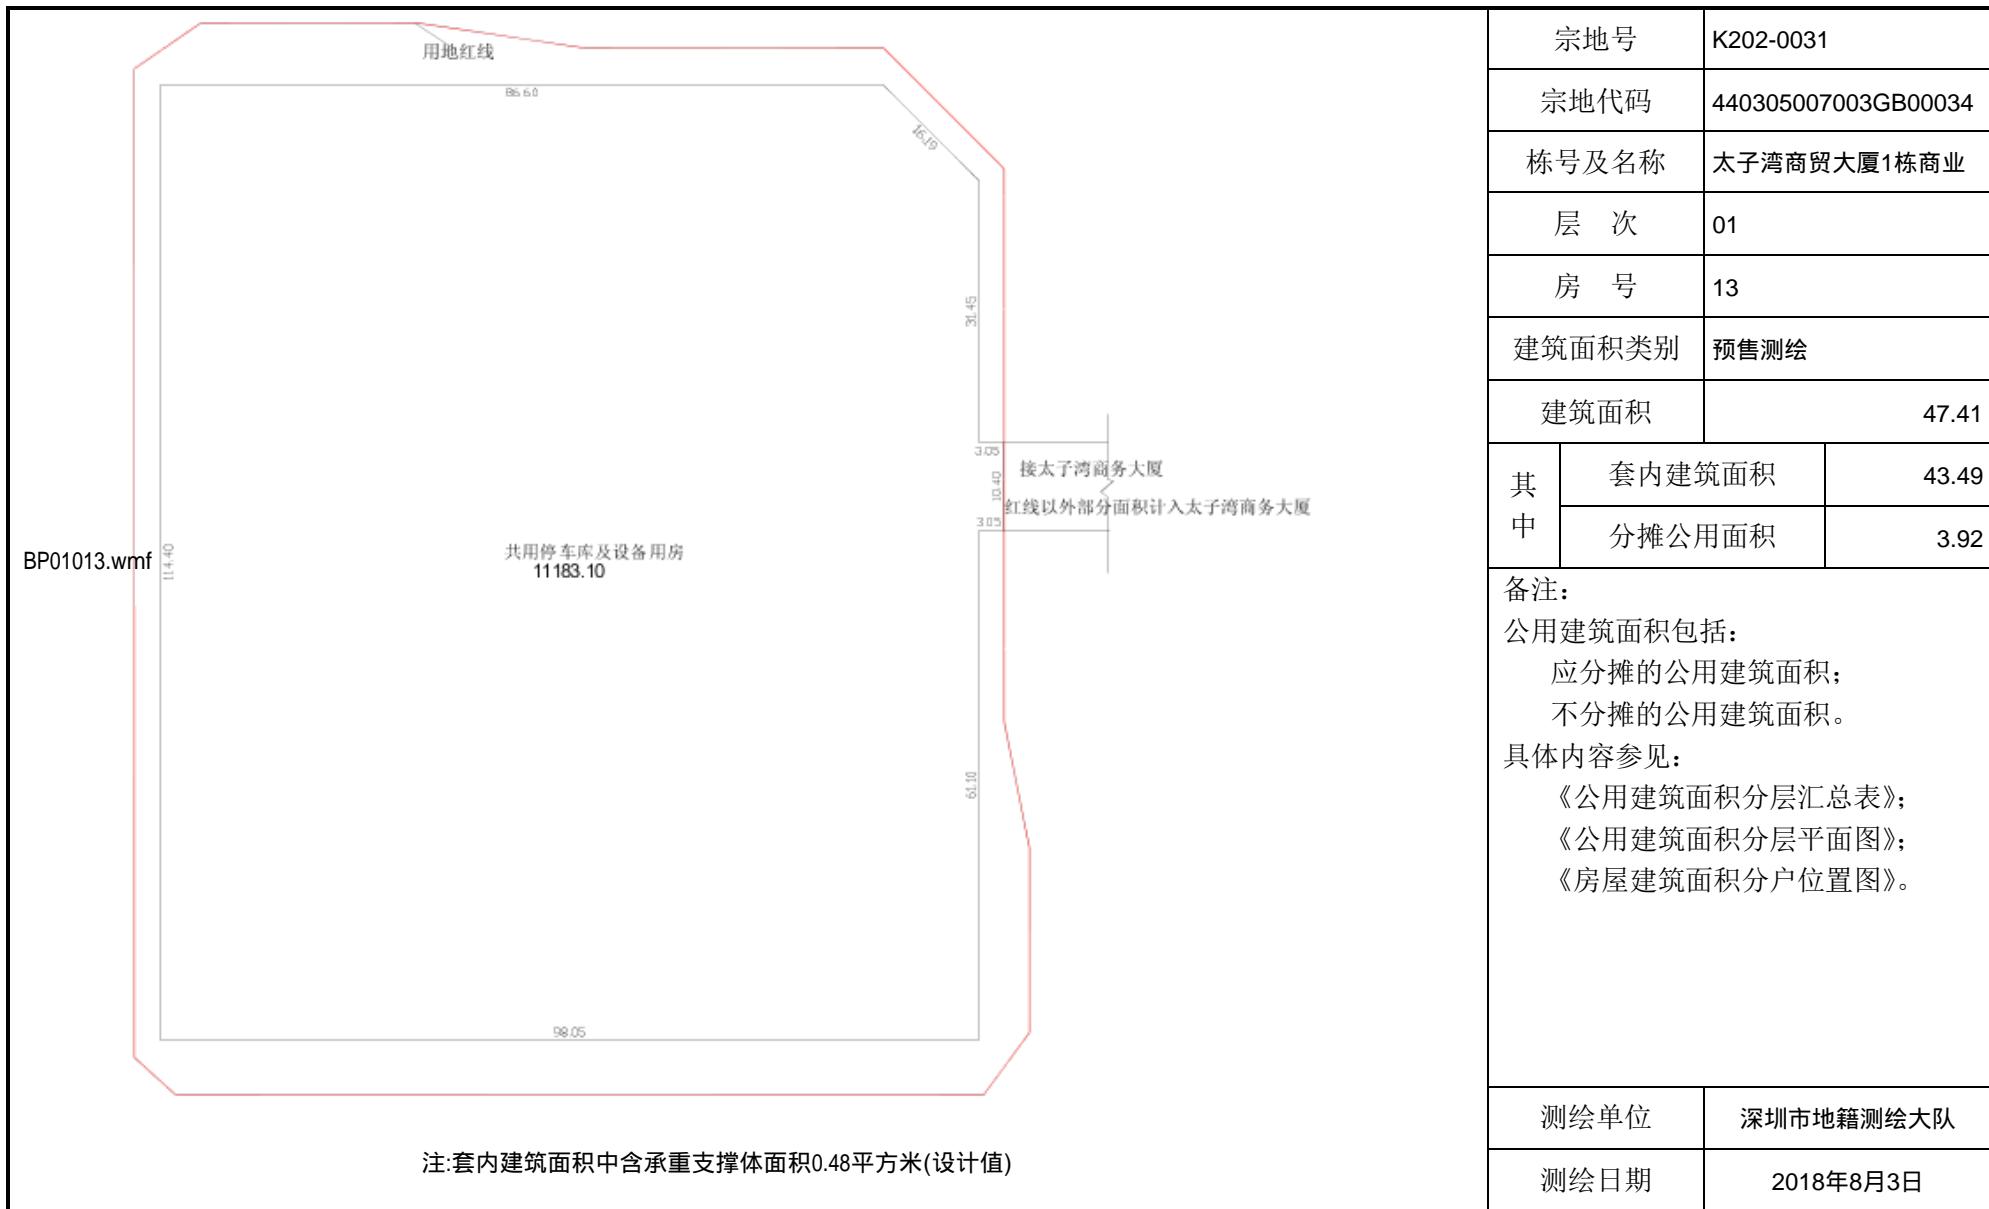


# 房屋建筑面积分户平面图

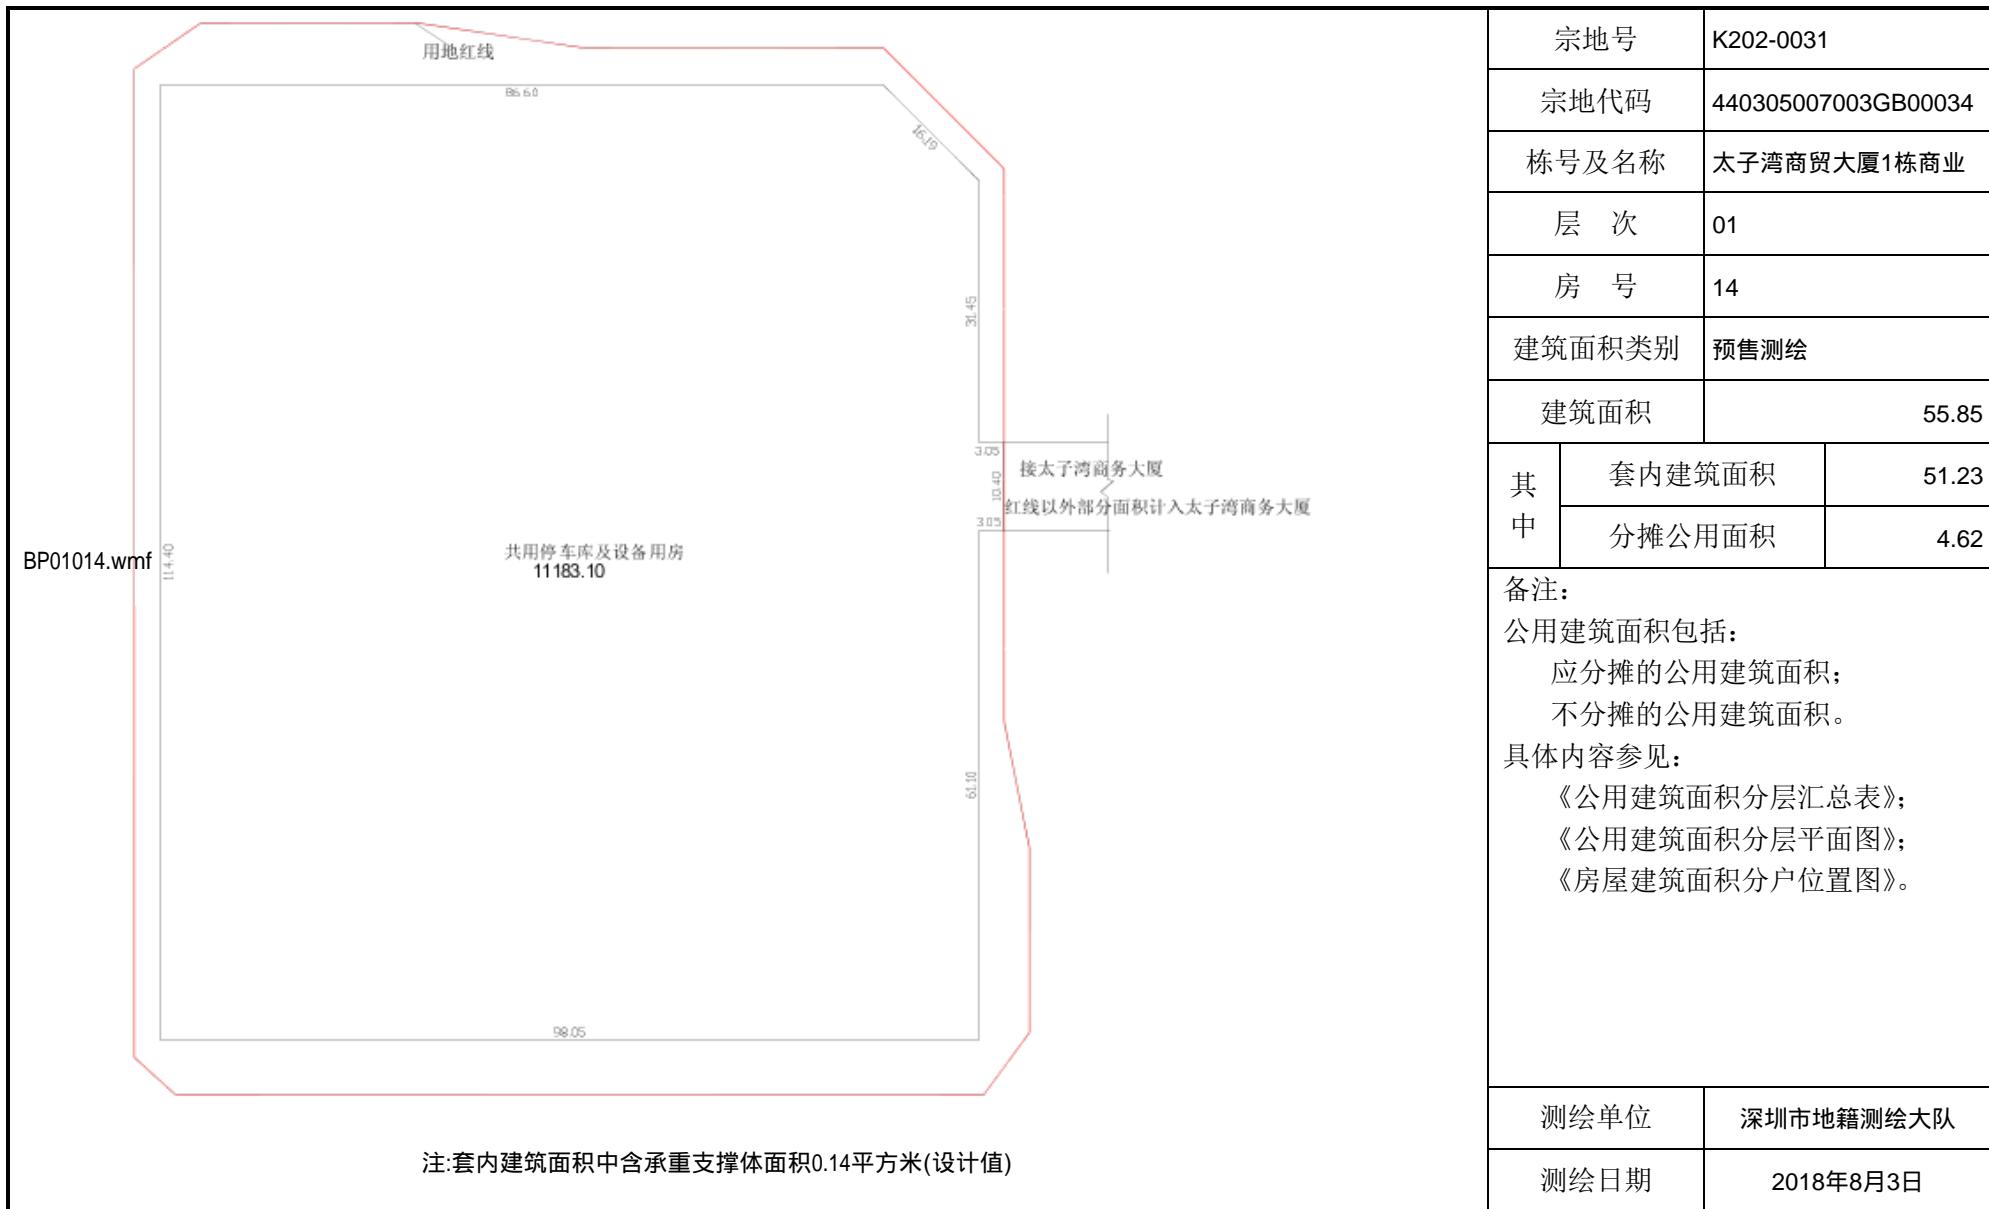


# 房屋建筑面积分户平面图

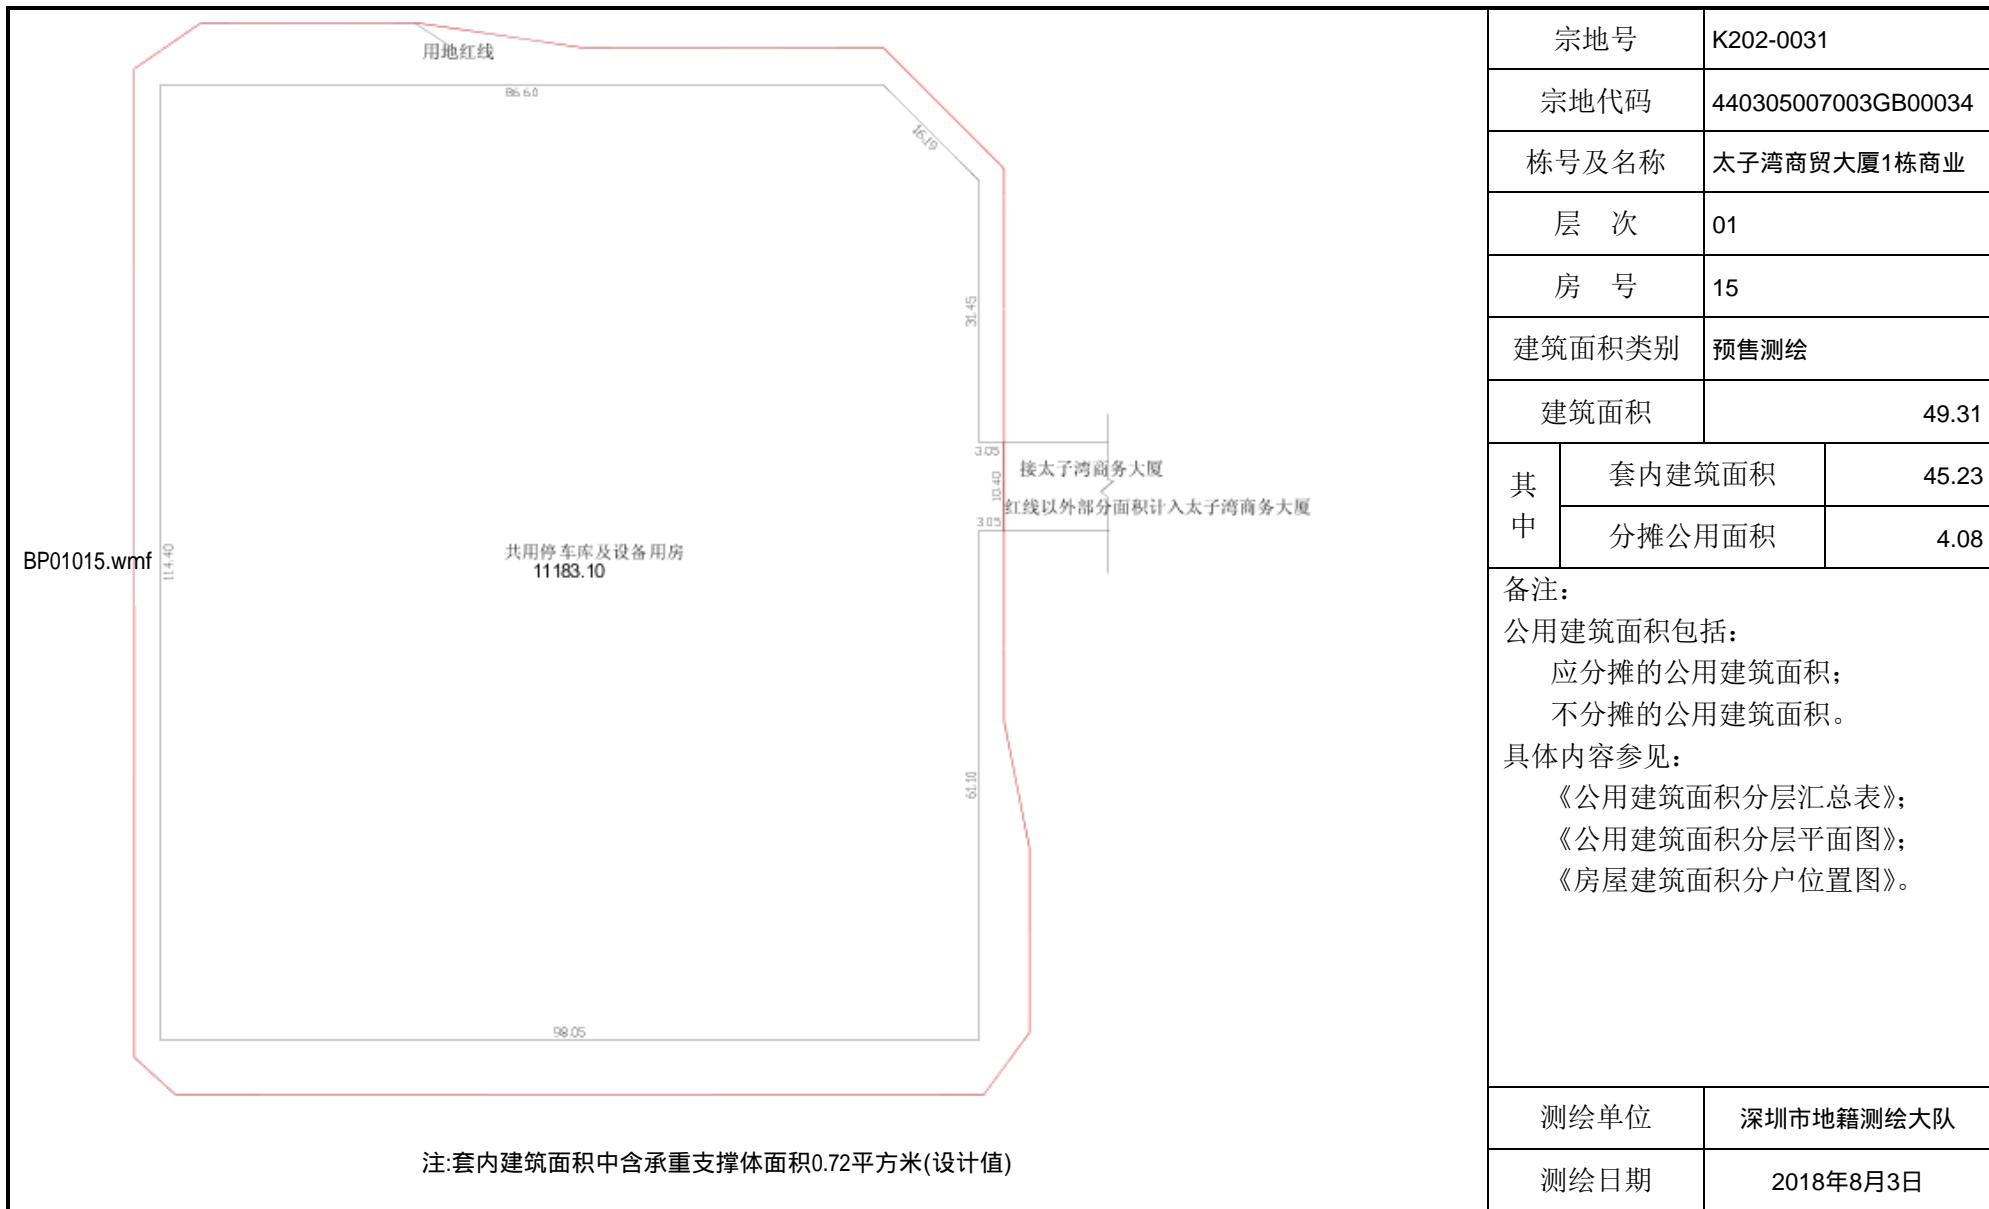


# 房屋建筑面积分户平面图

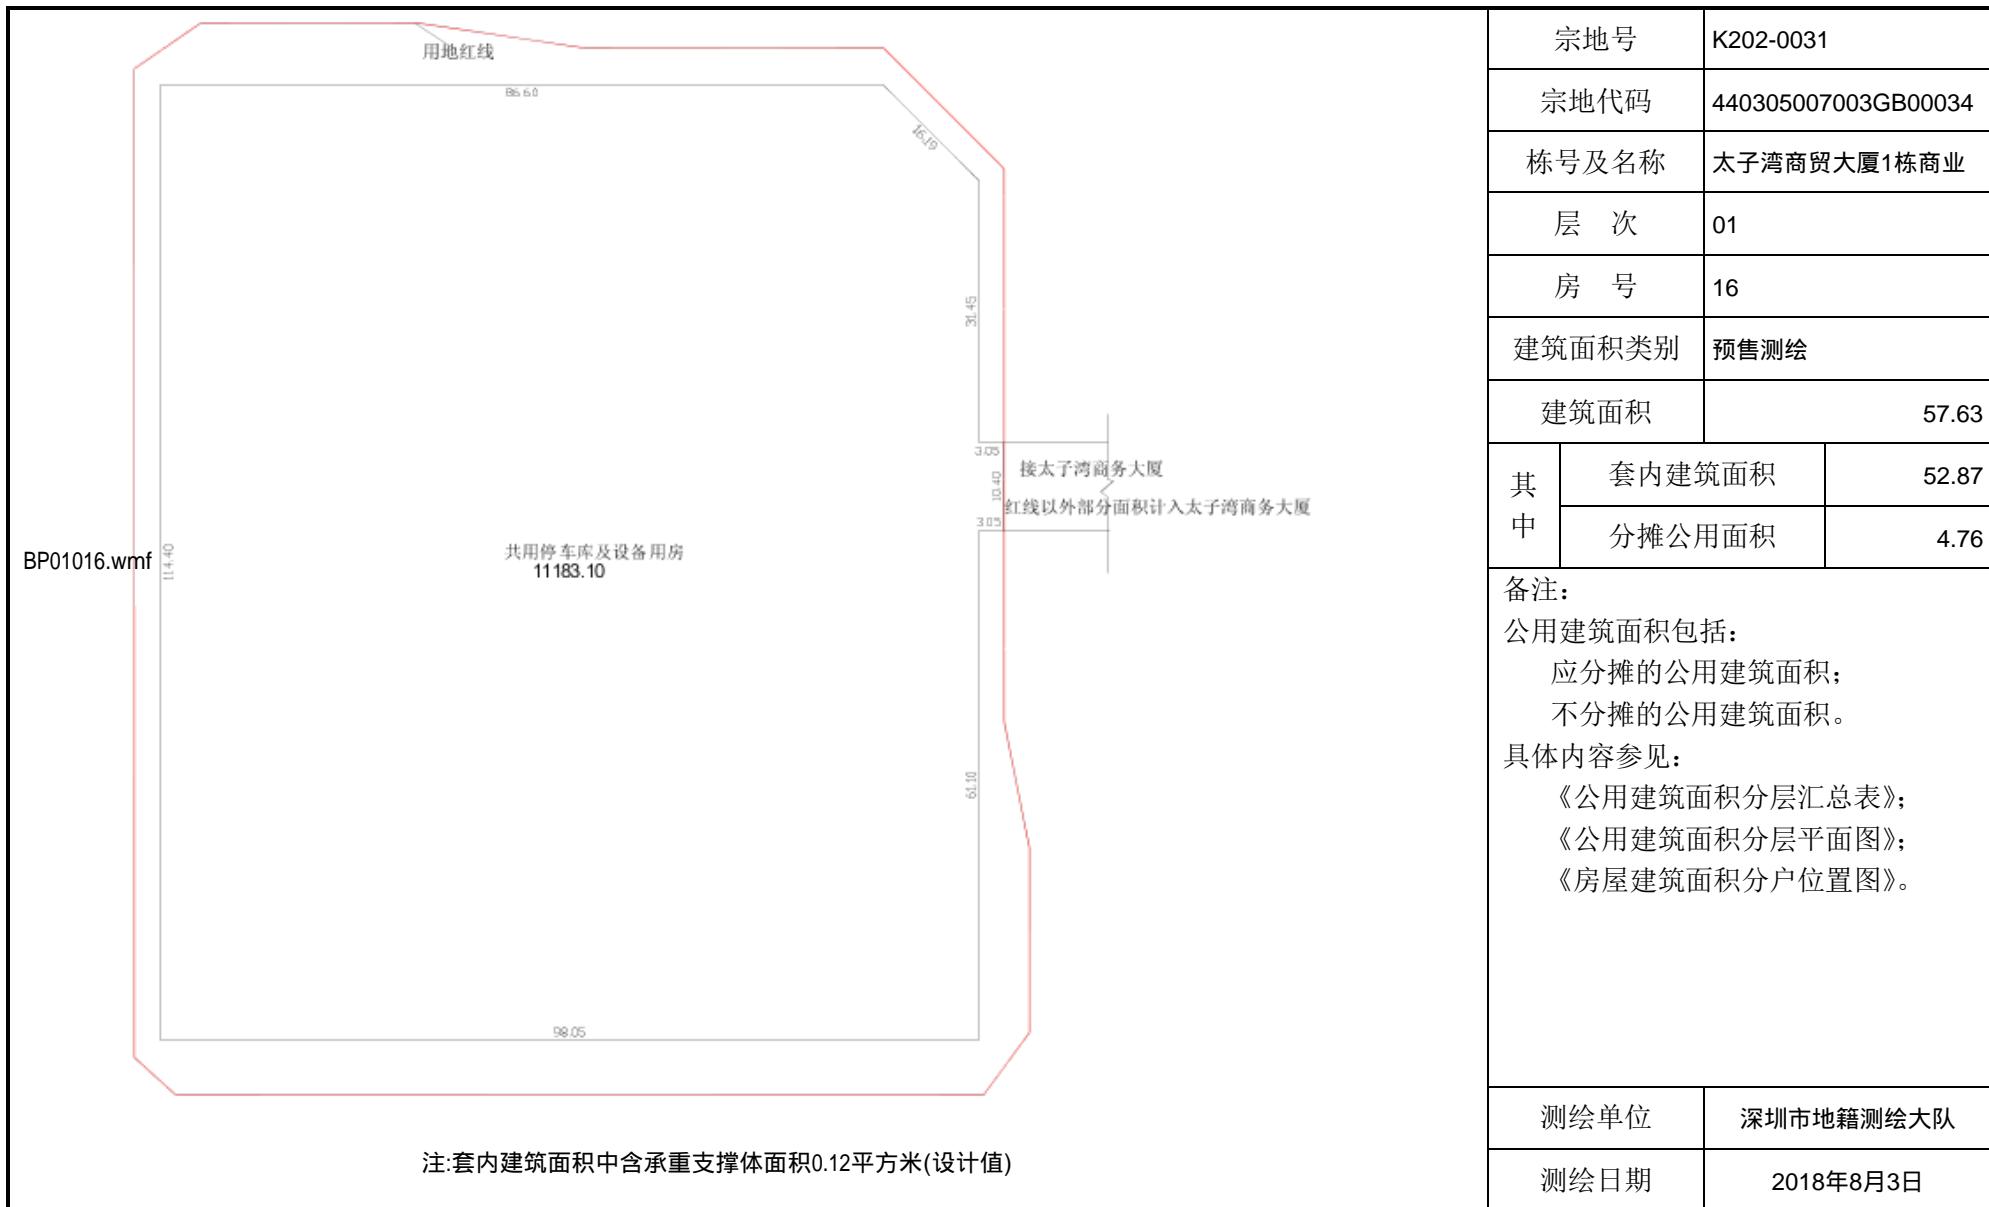


# 房屋建筑面积分户平面图

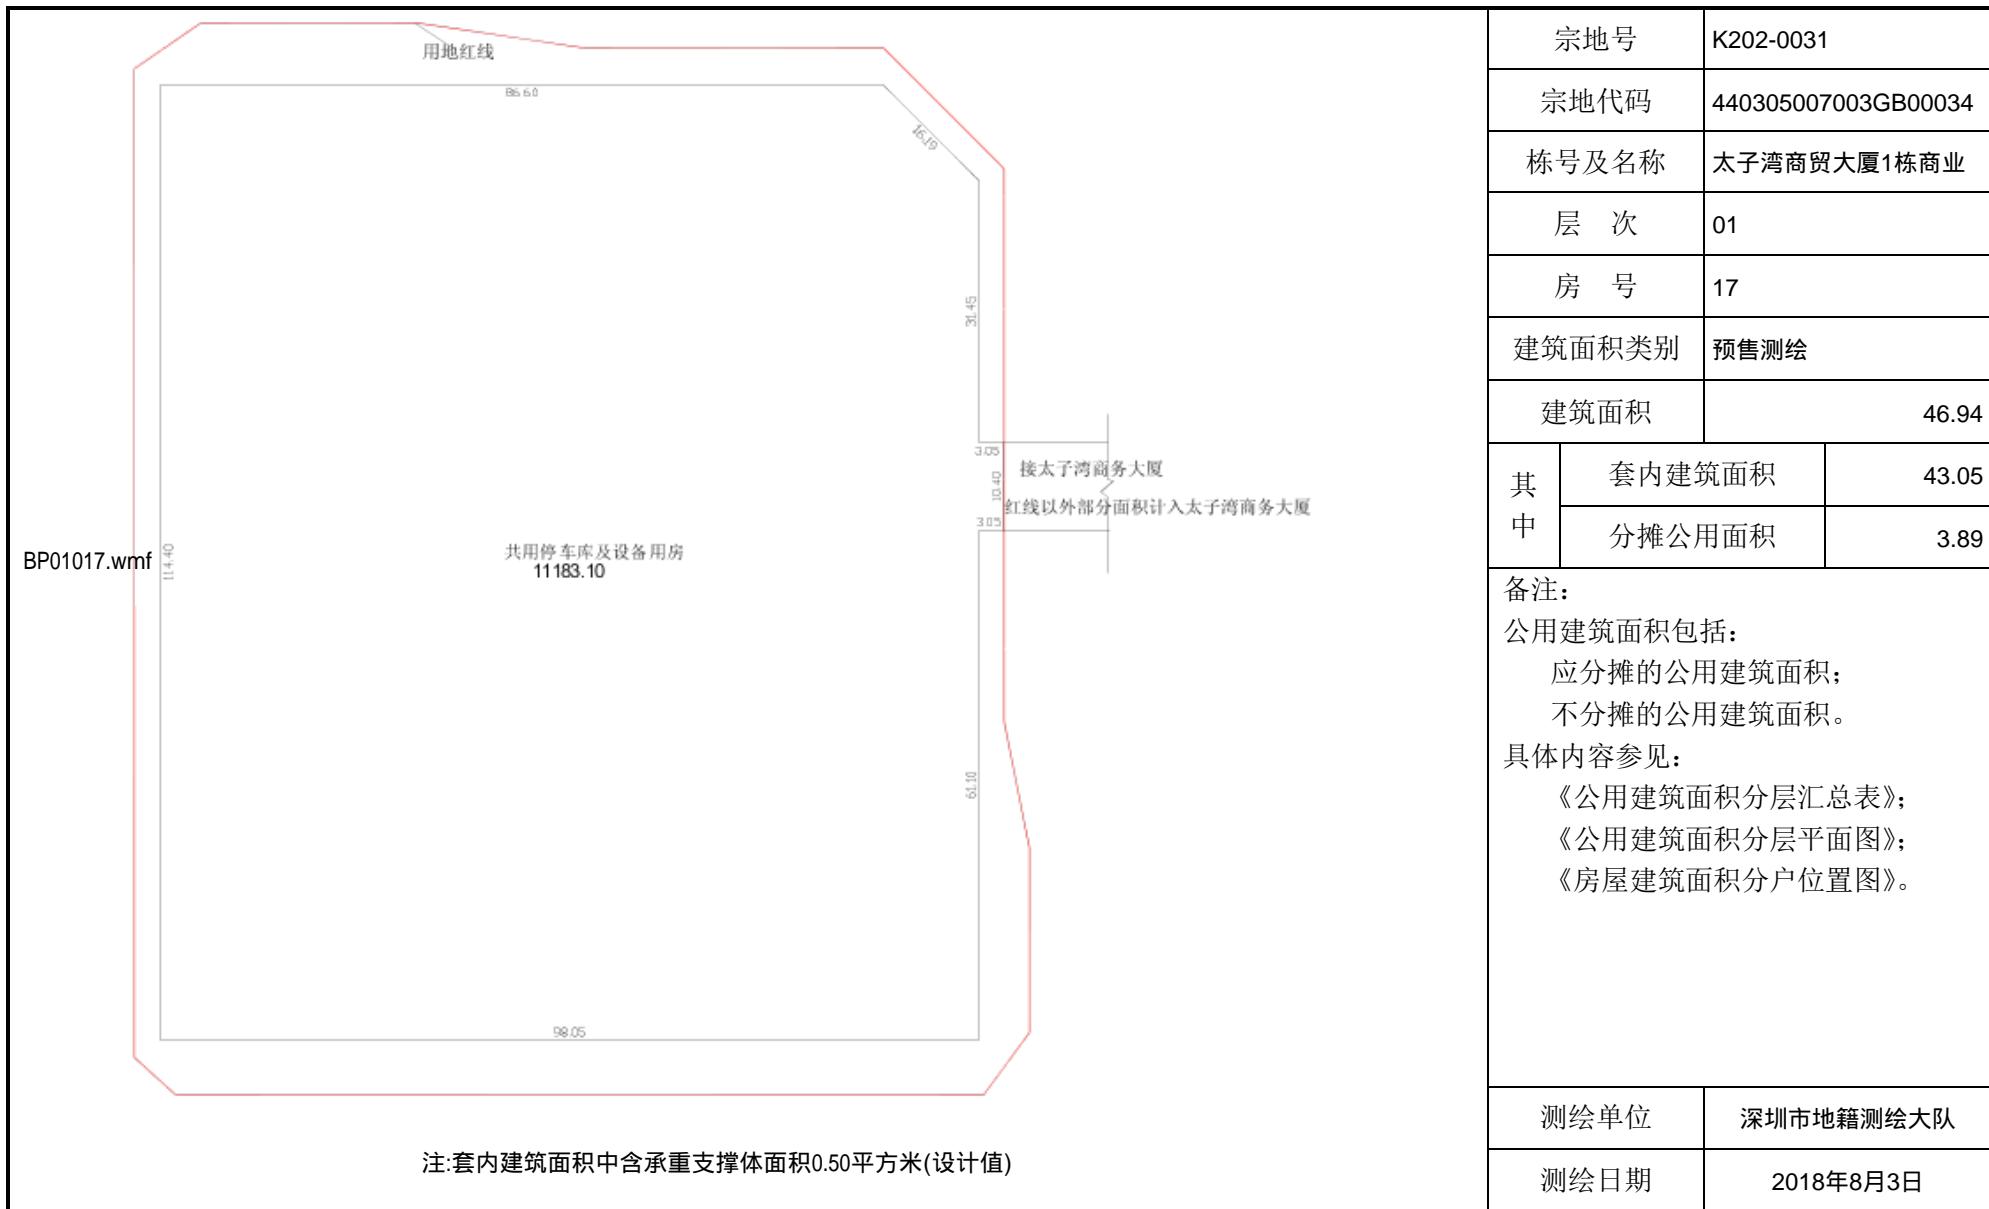


# 房屋建筑面积分户平面图

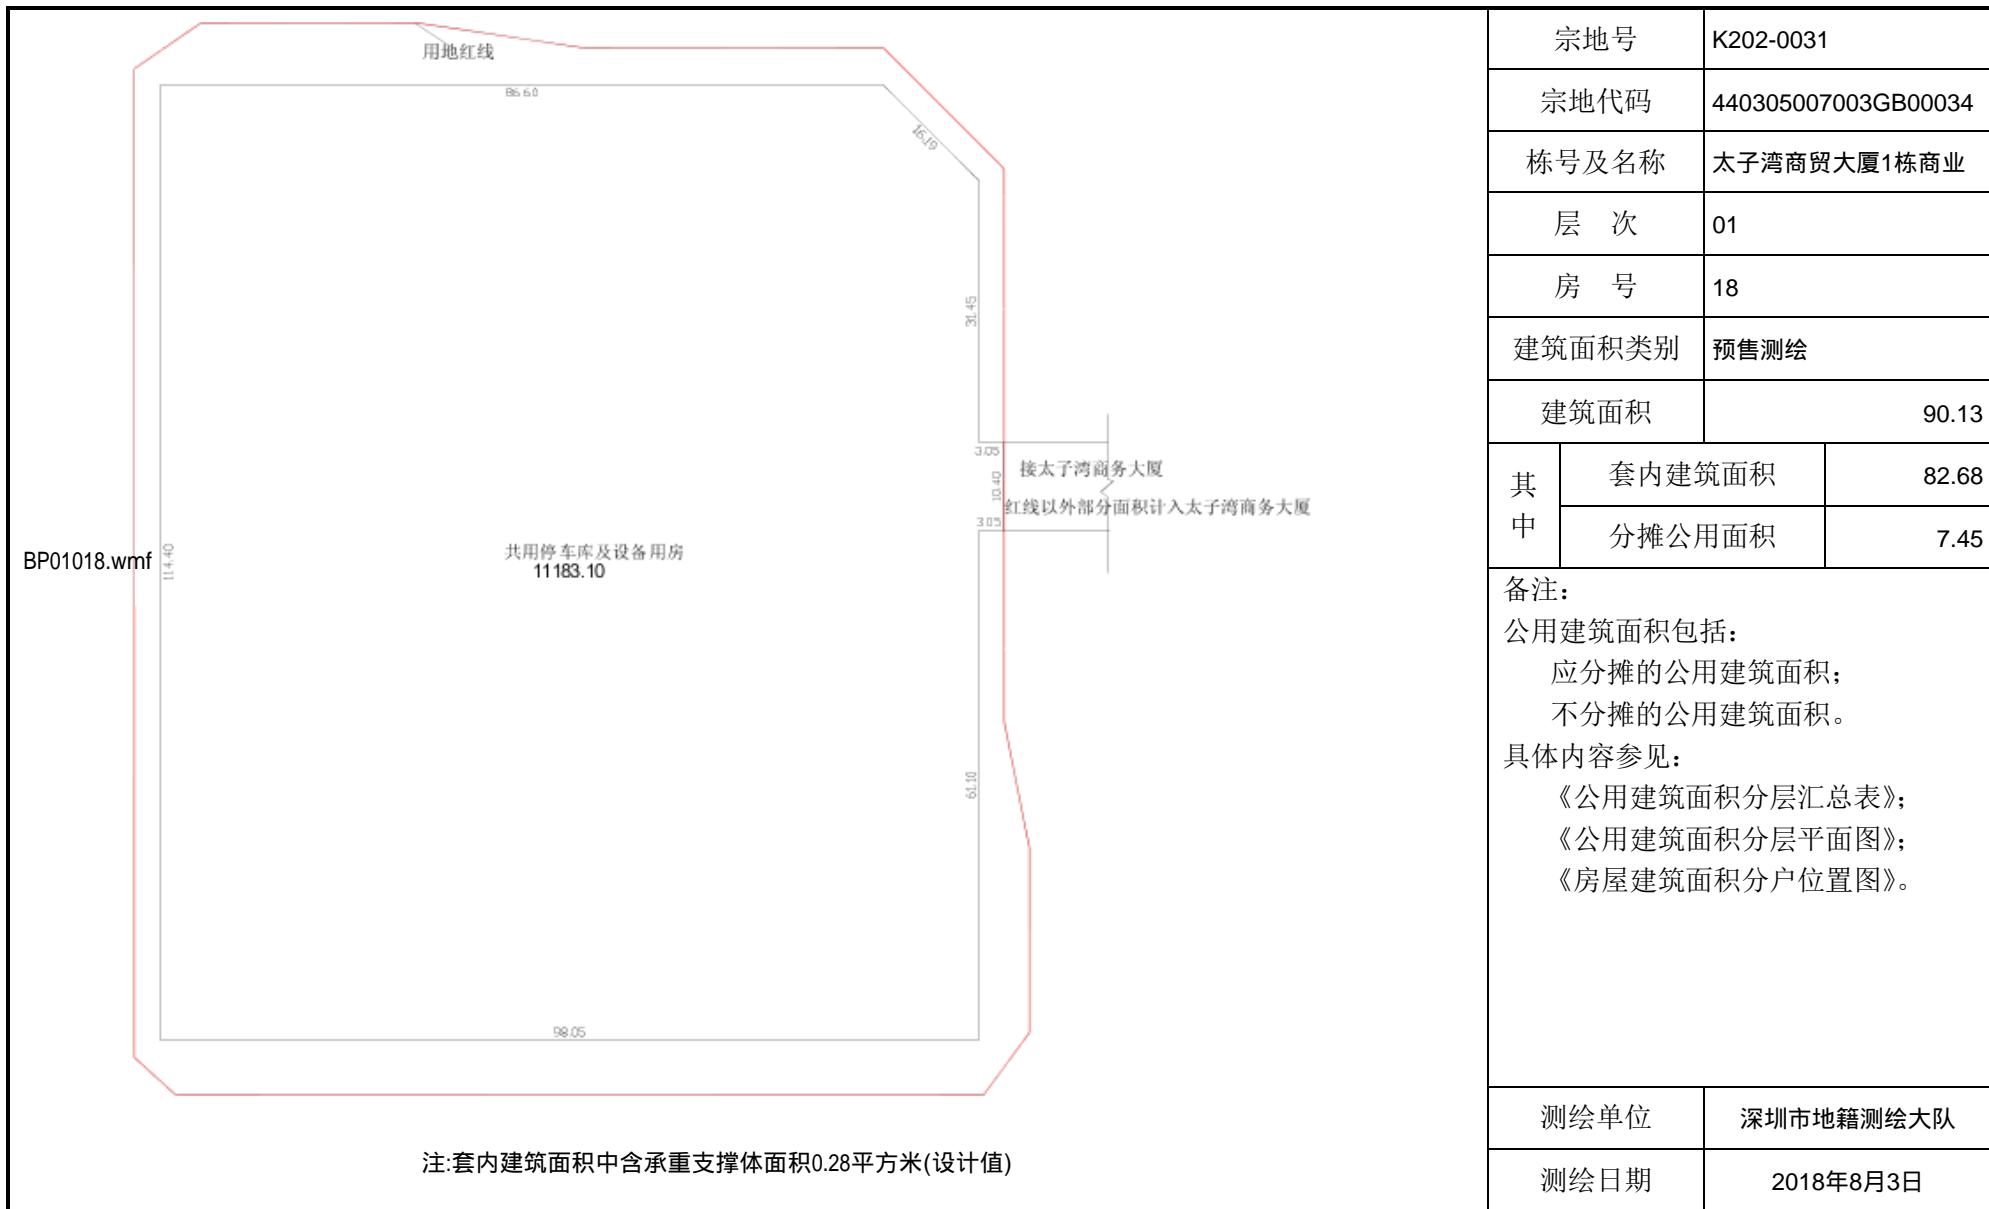


# 房屋建筑面积分户平面图

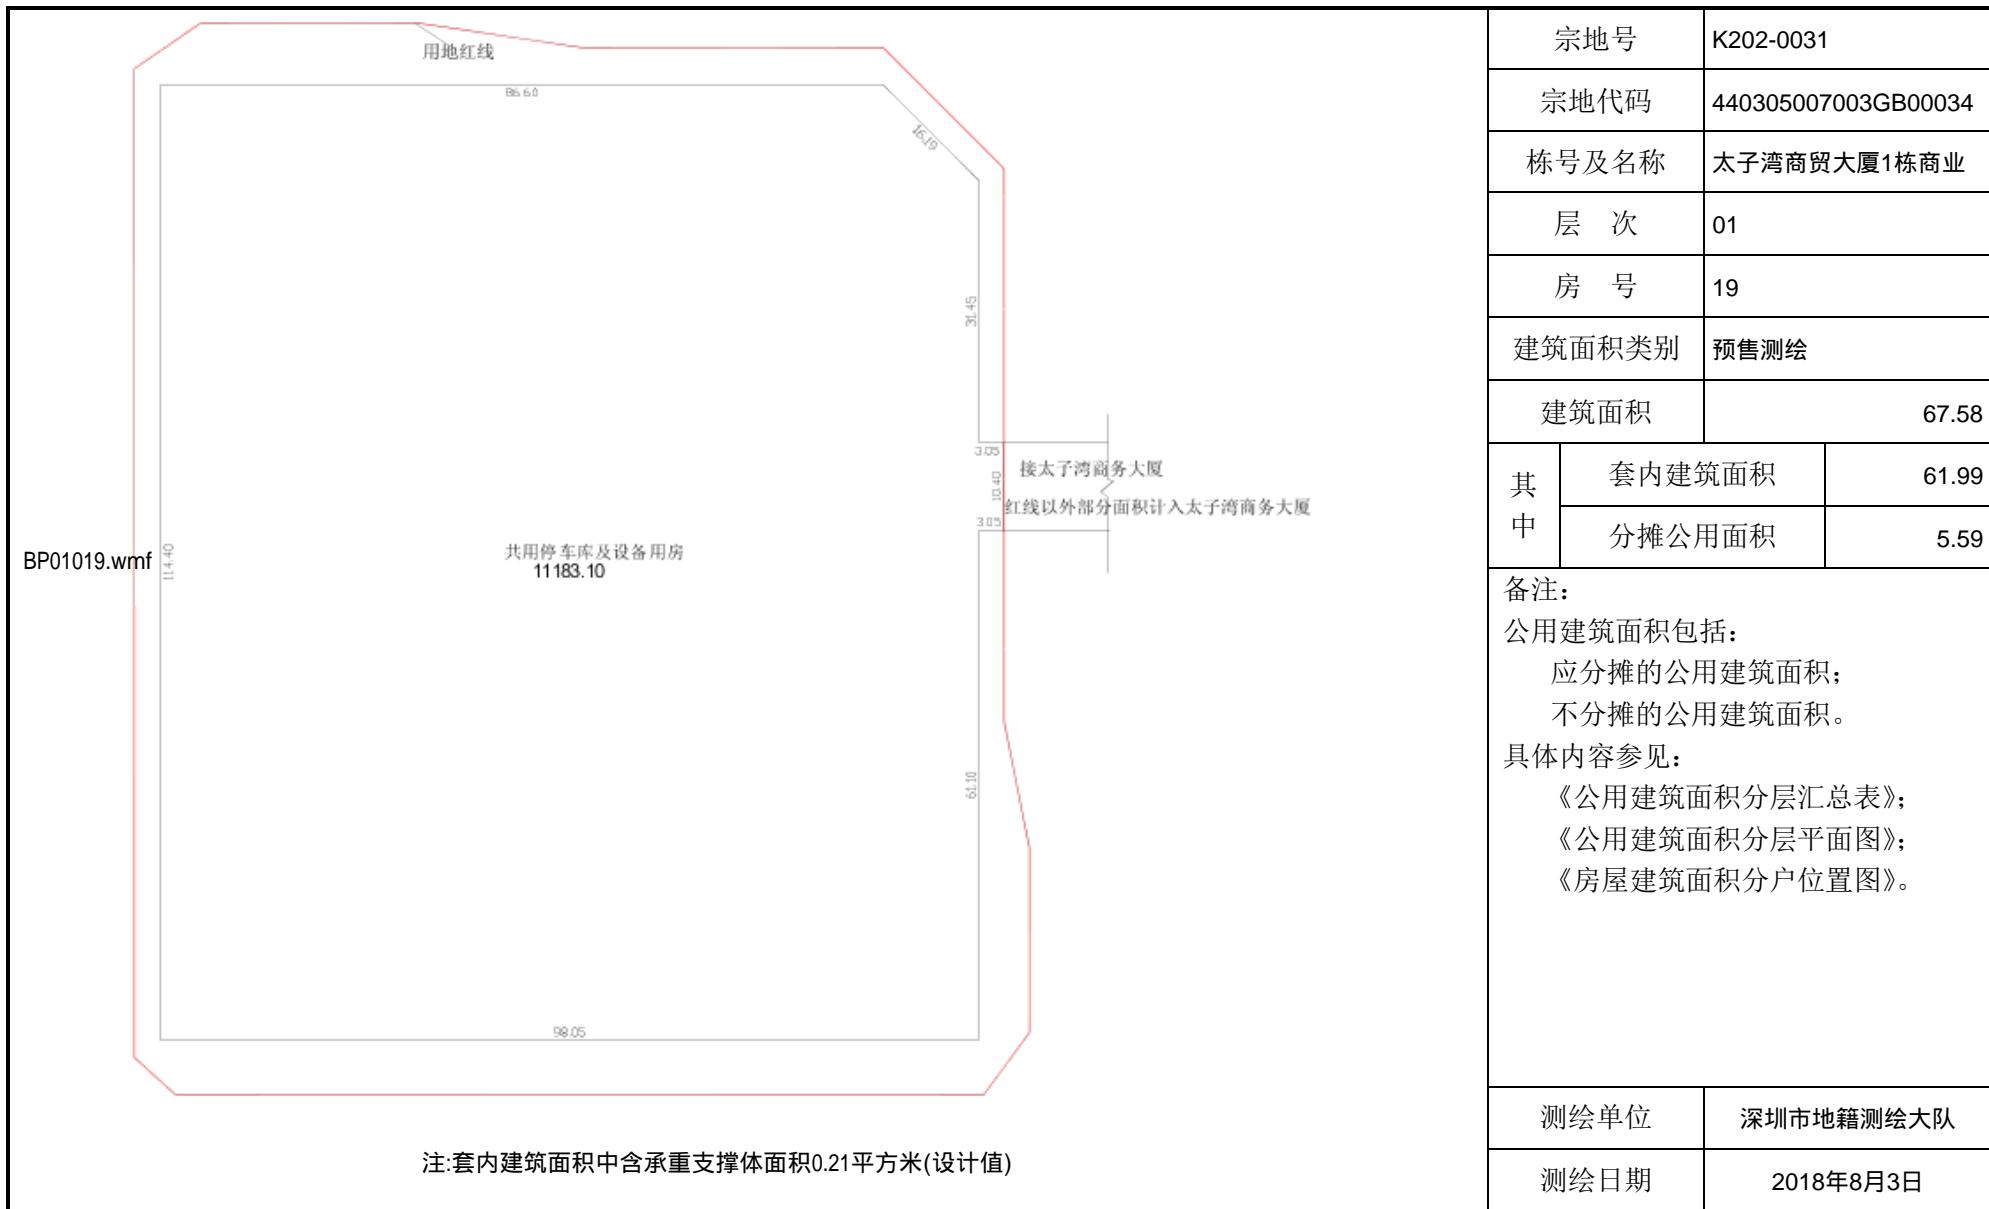


# 房屋建筑面积分户平面图

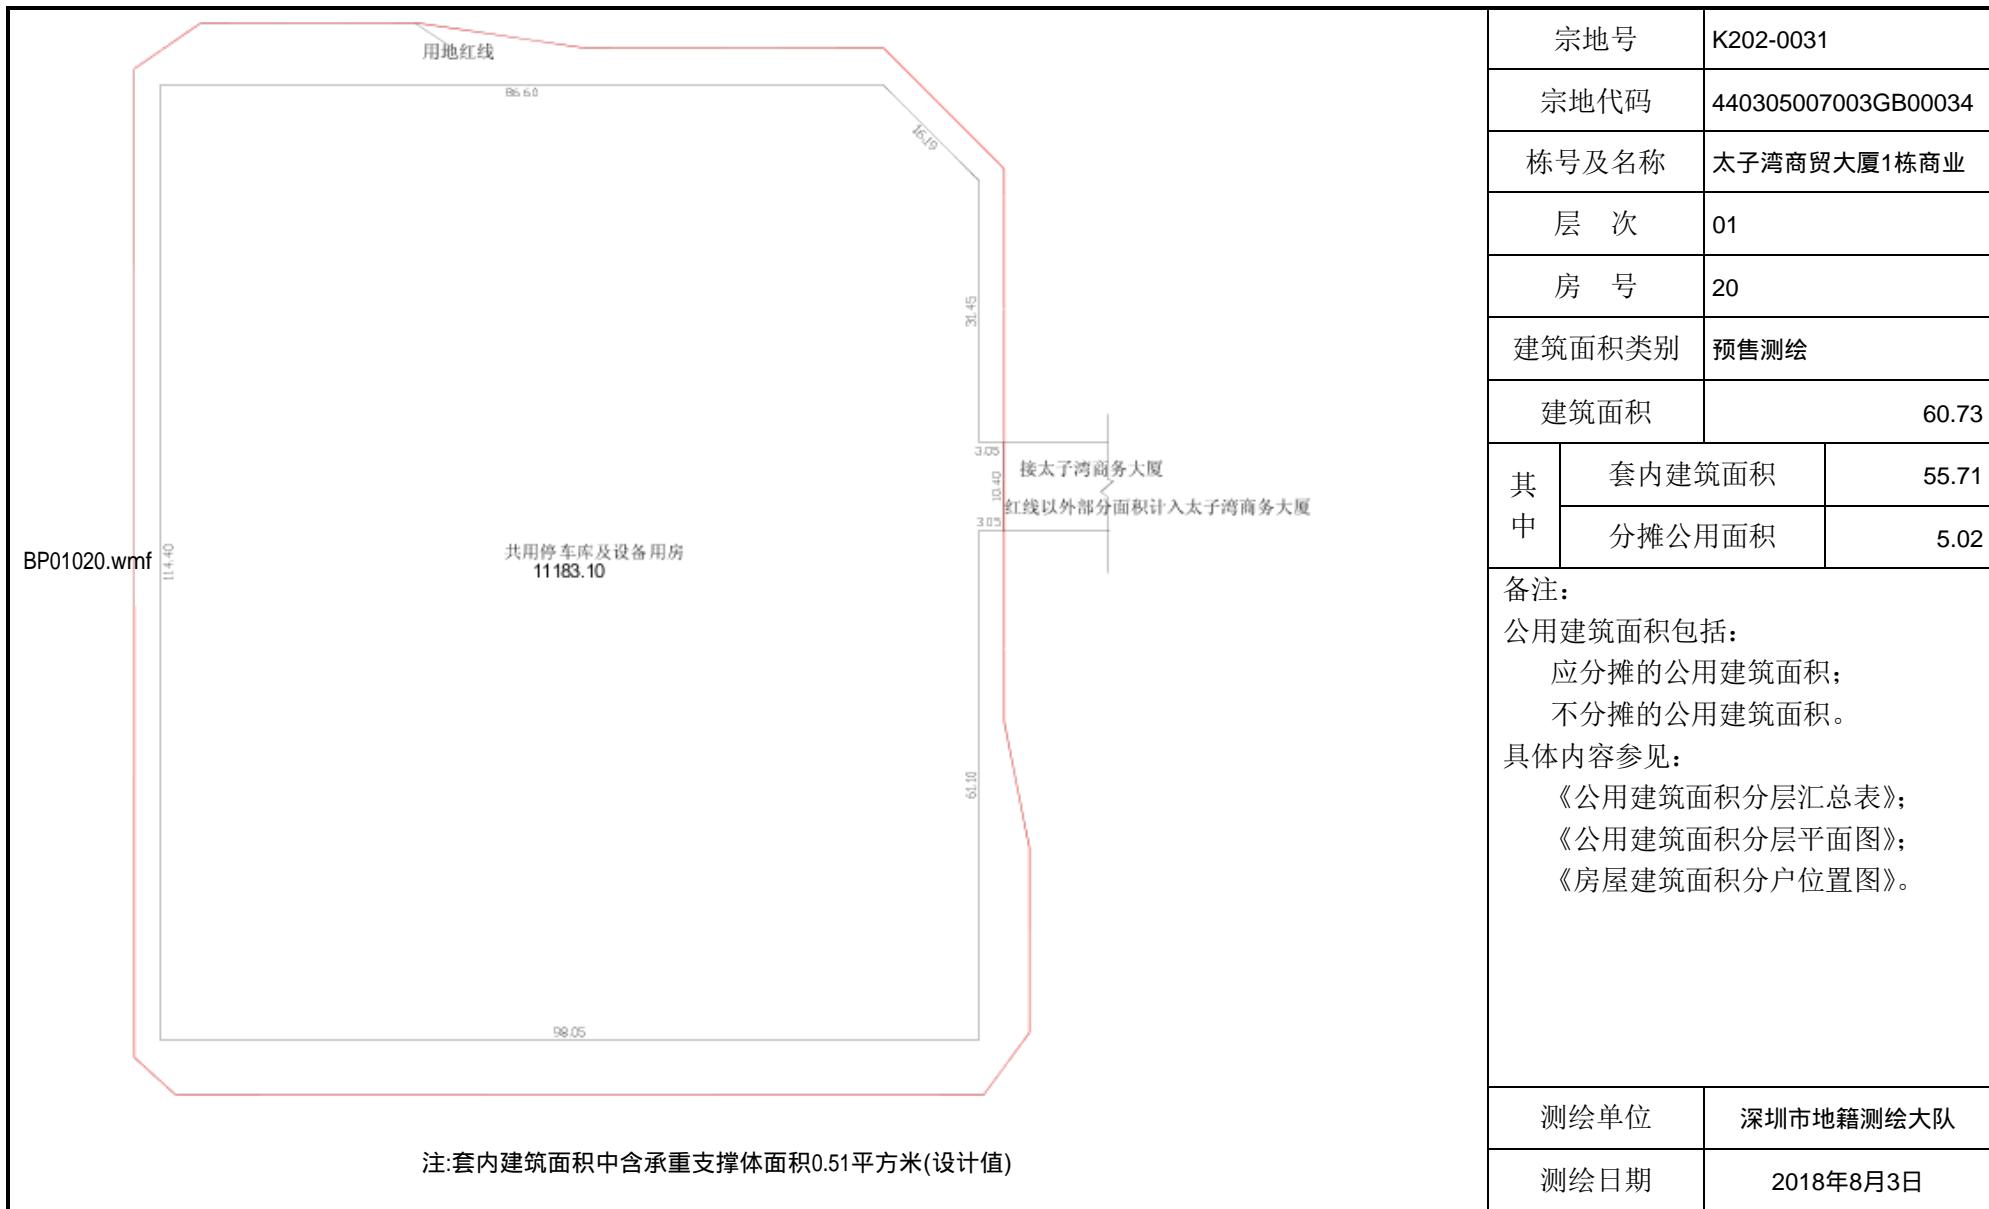


# 房屋建筑面积分户平面图

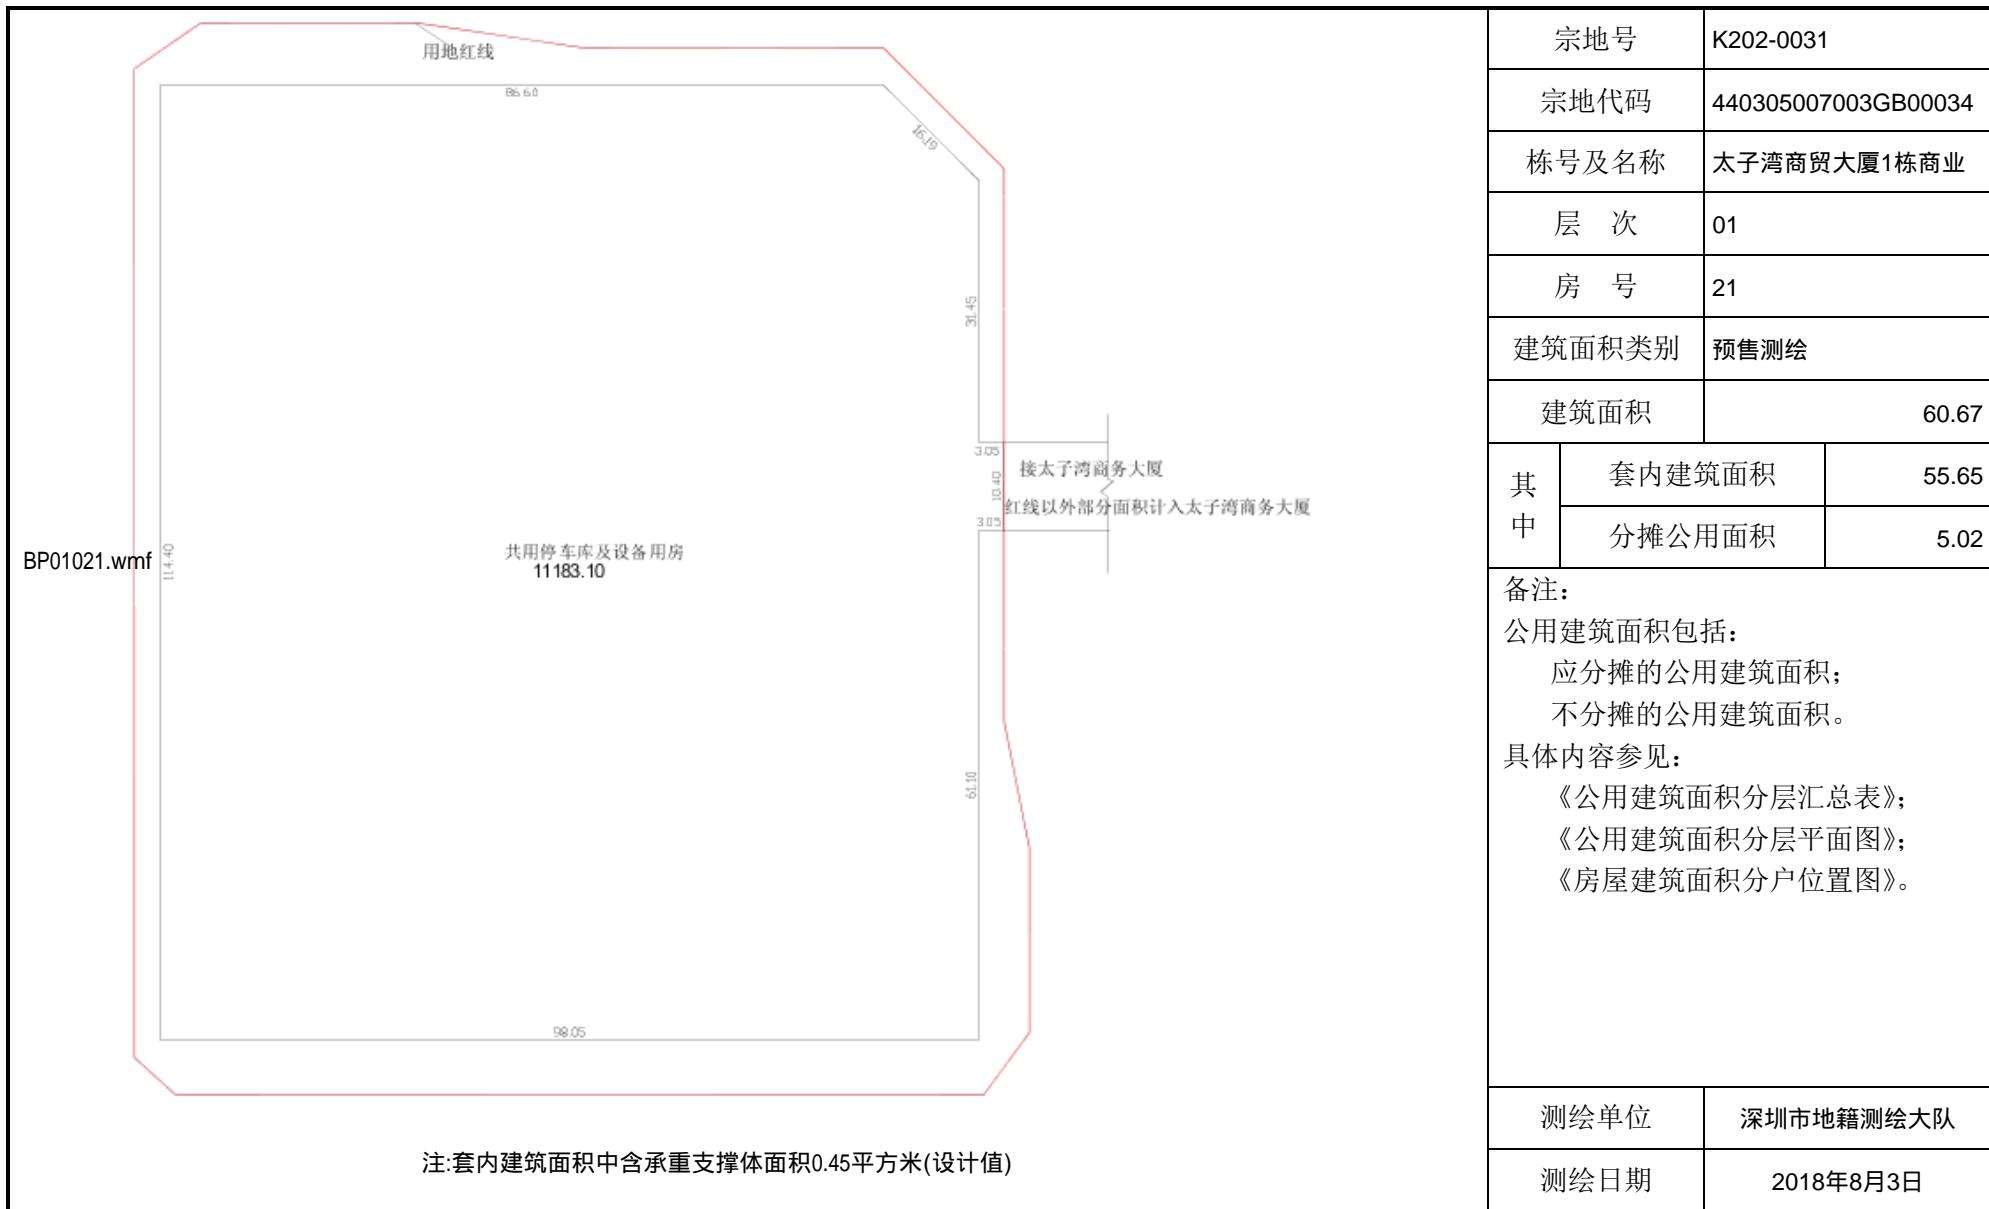


# 房屋建筑面积分户平面图

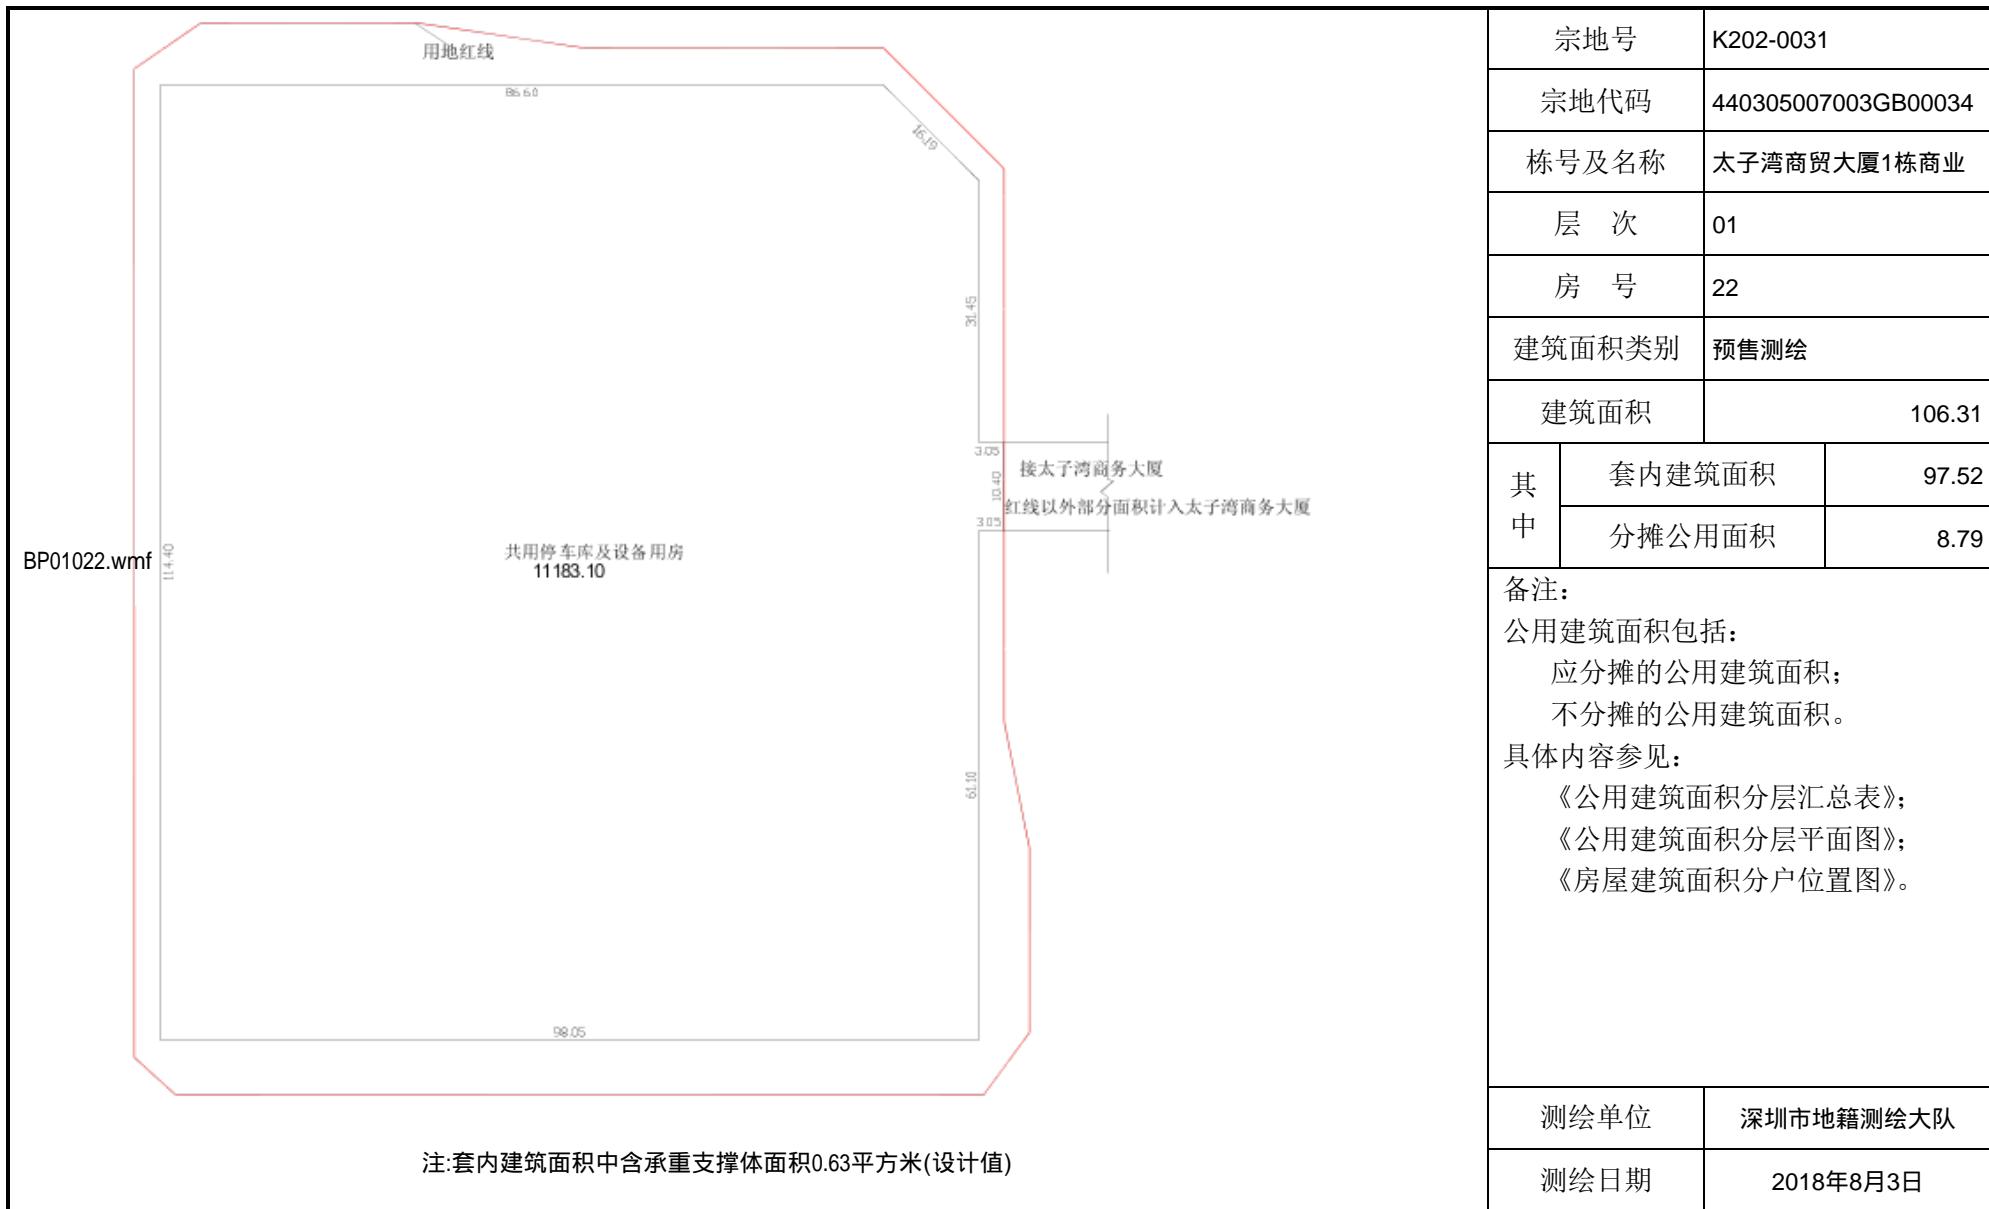


# 房屋建筑面积分户平面图

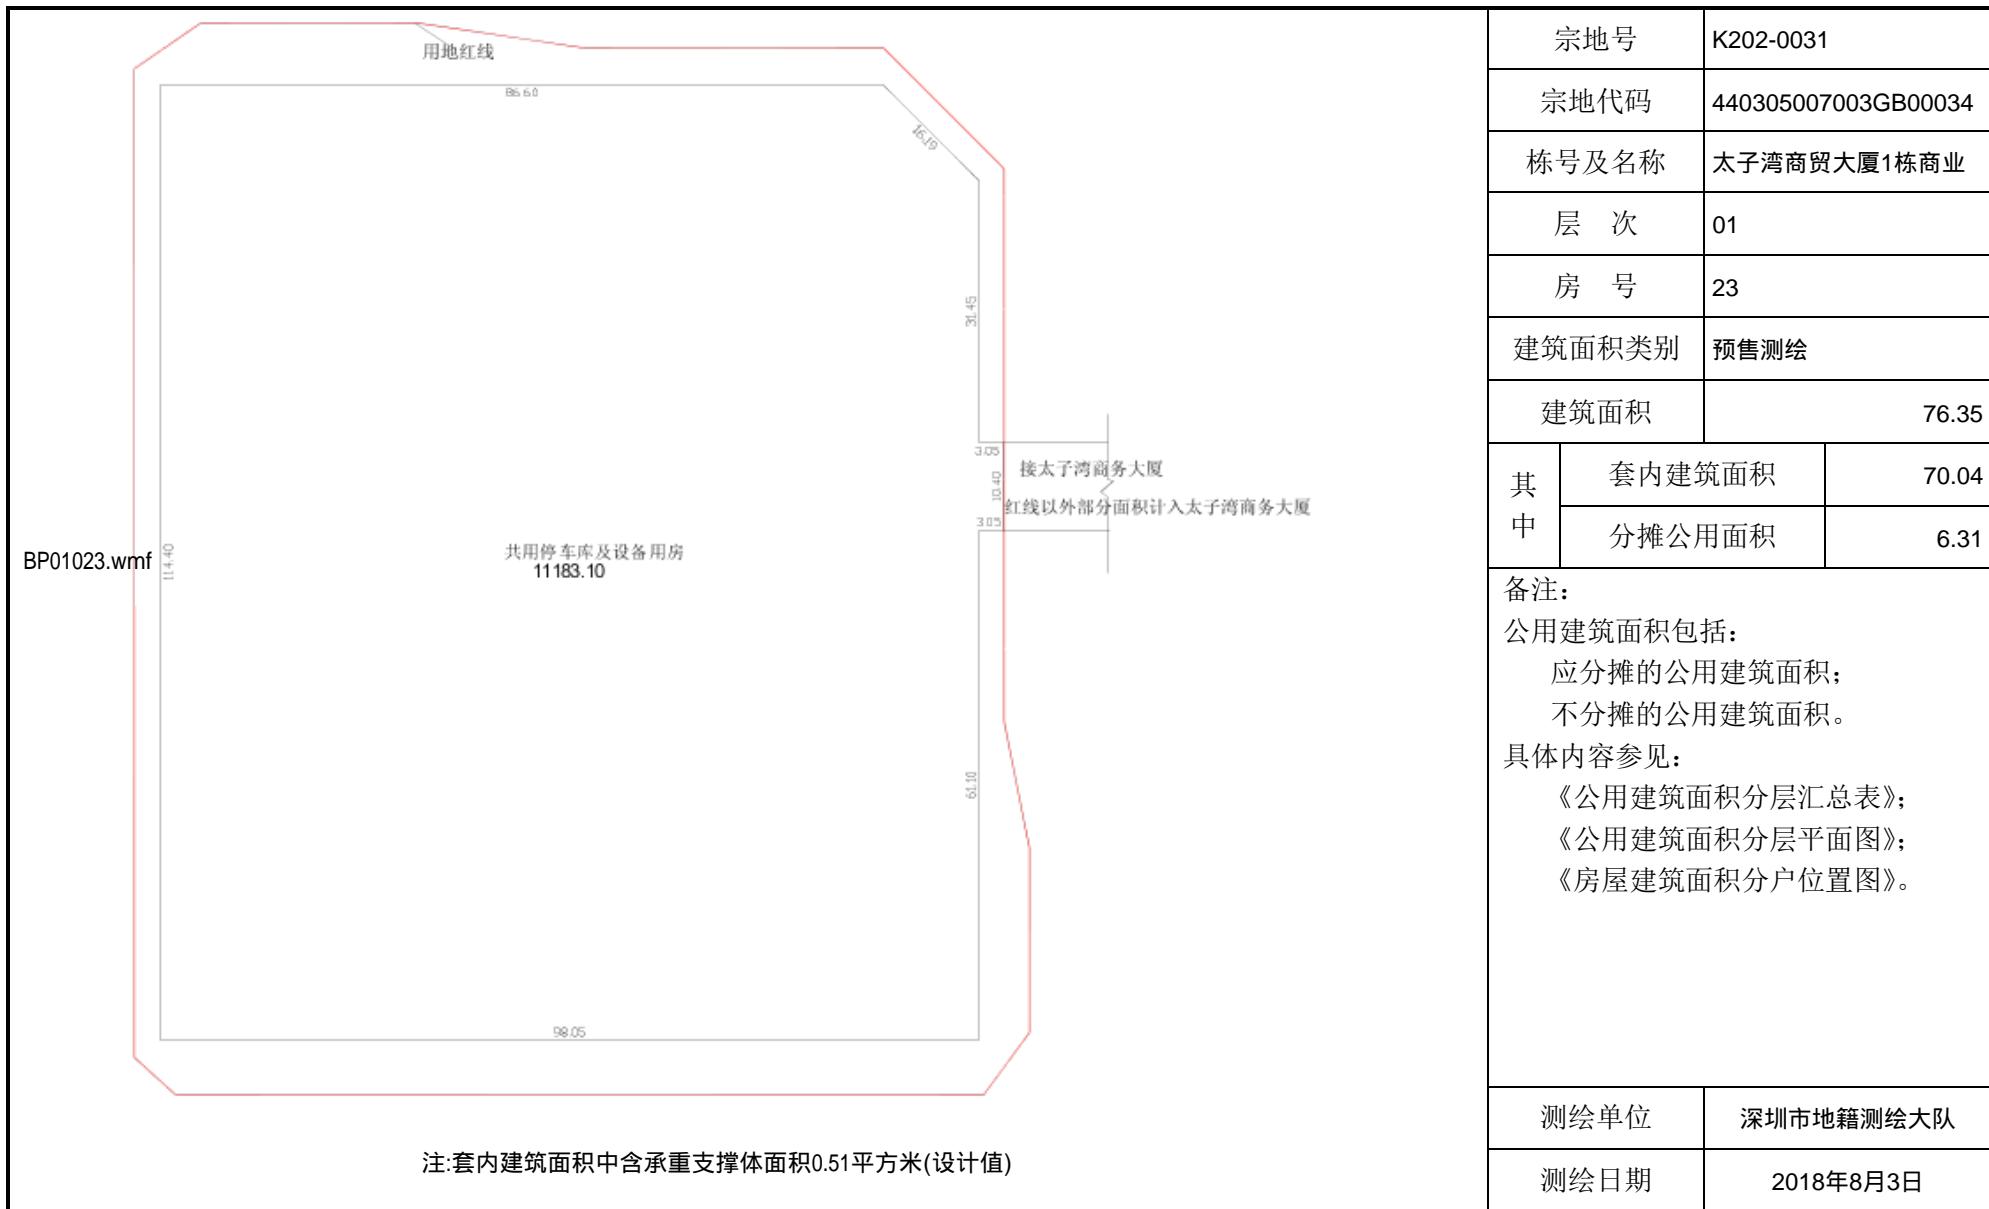


# 房屋建筑面积分户平面图

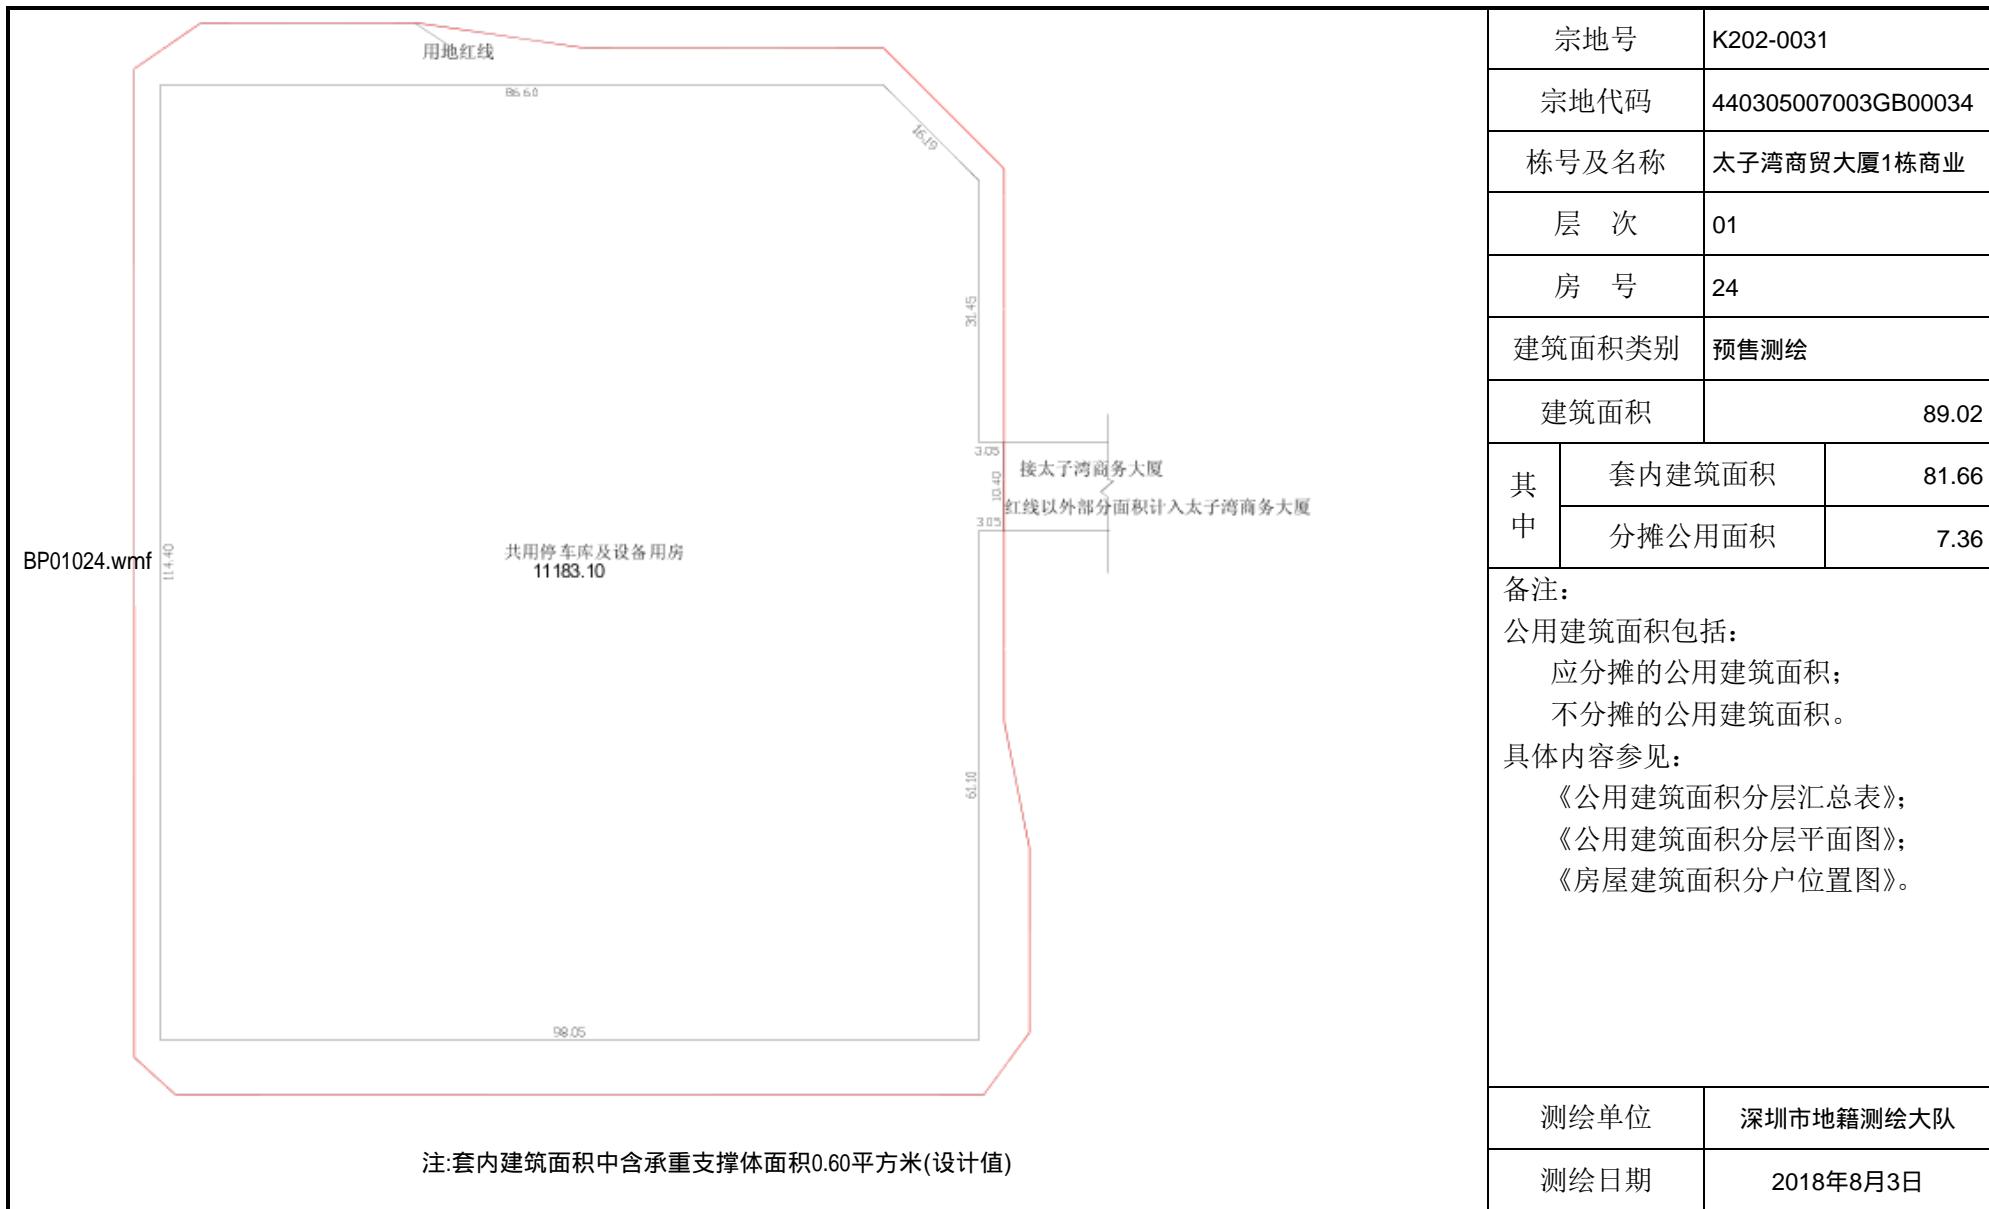


# 房屋建筑面积分户平面图

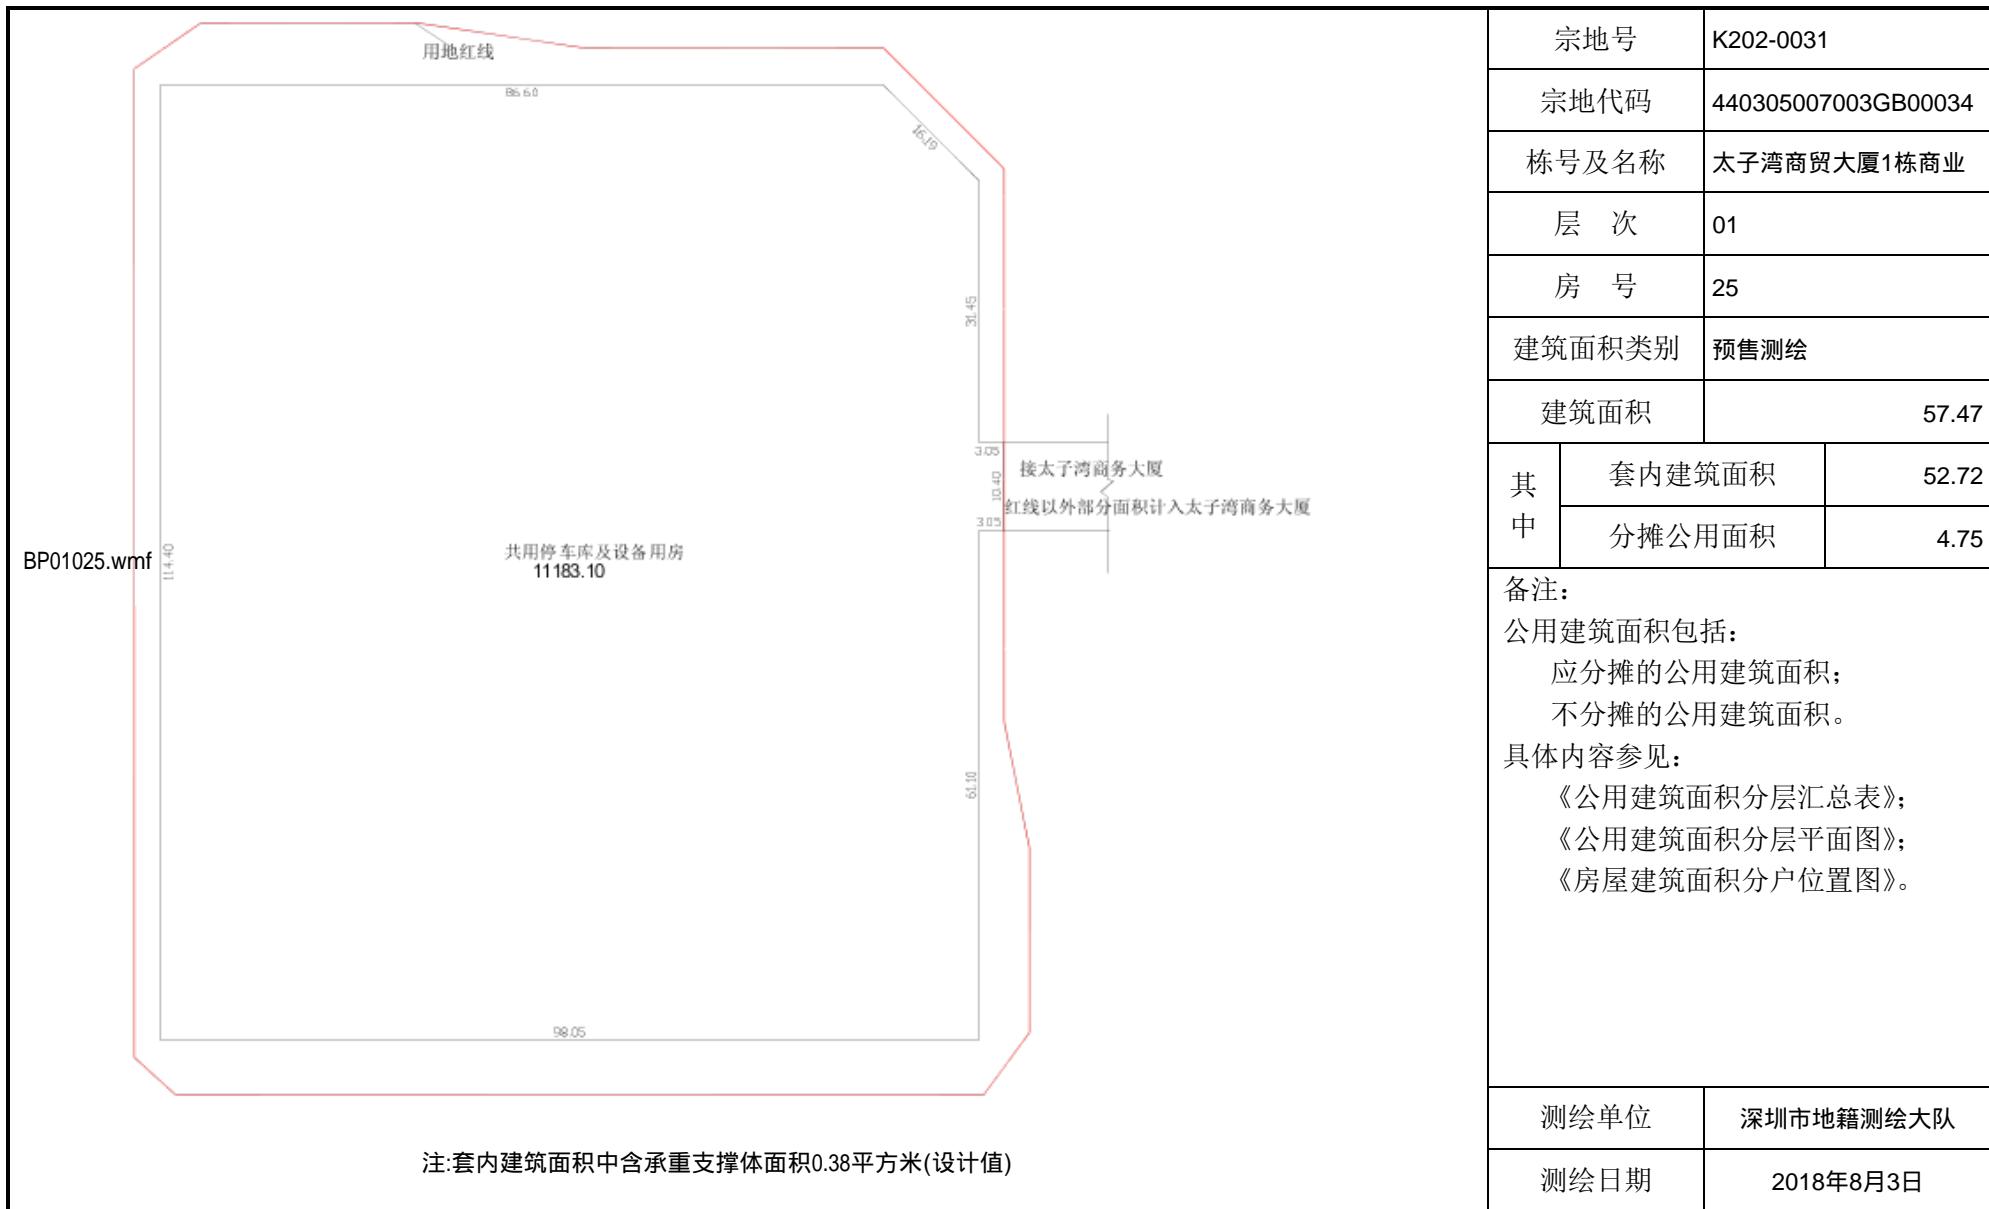


# 房屋建筑面积分户平面图

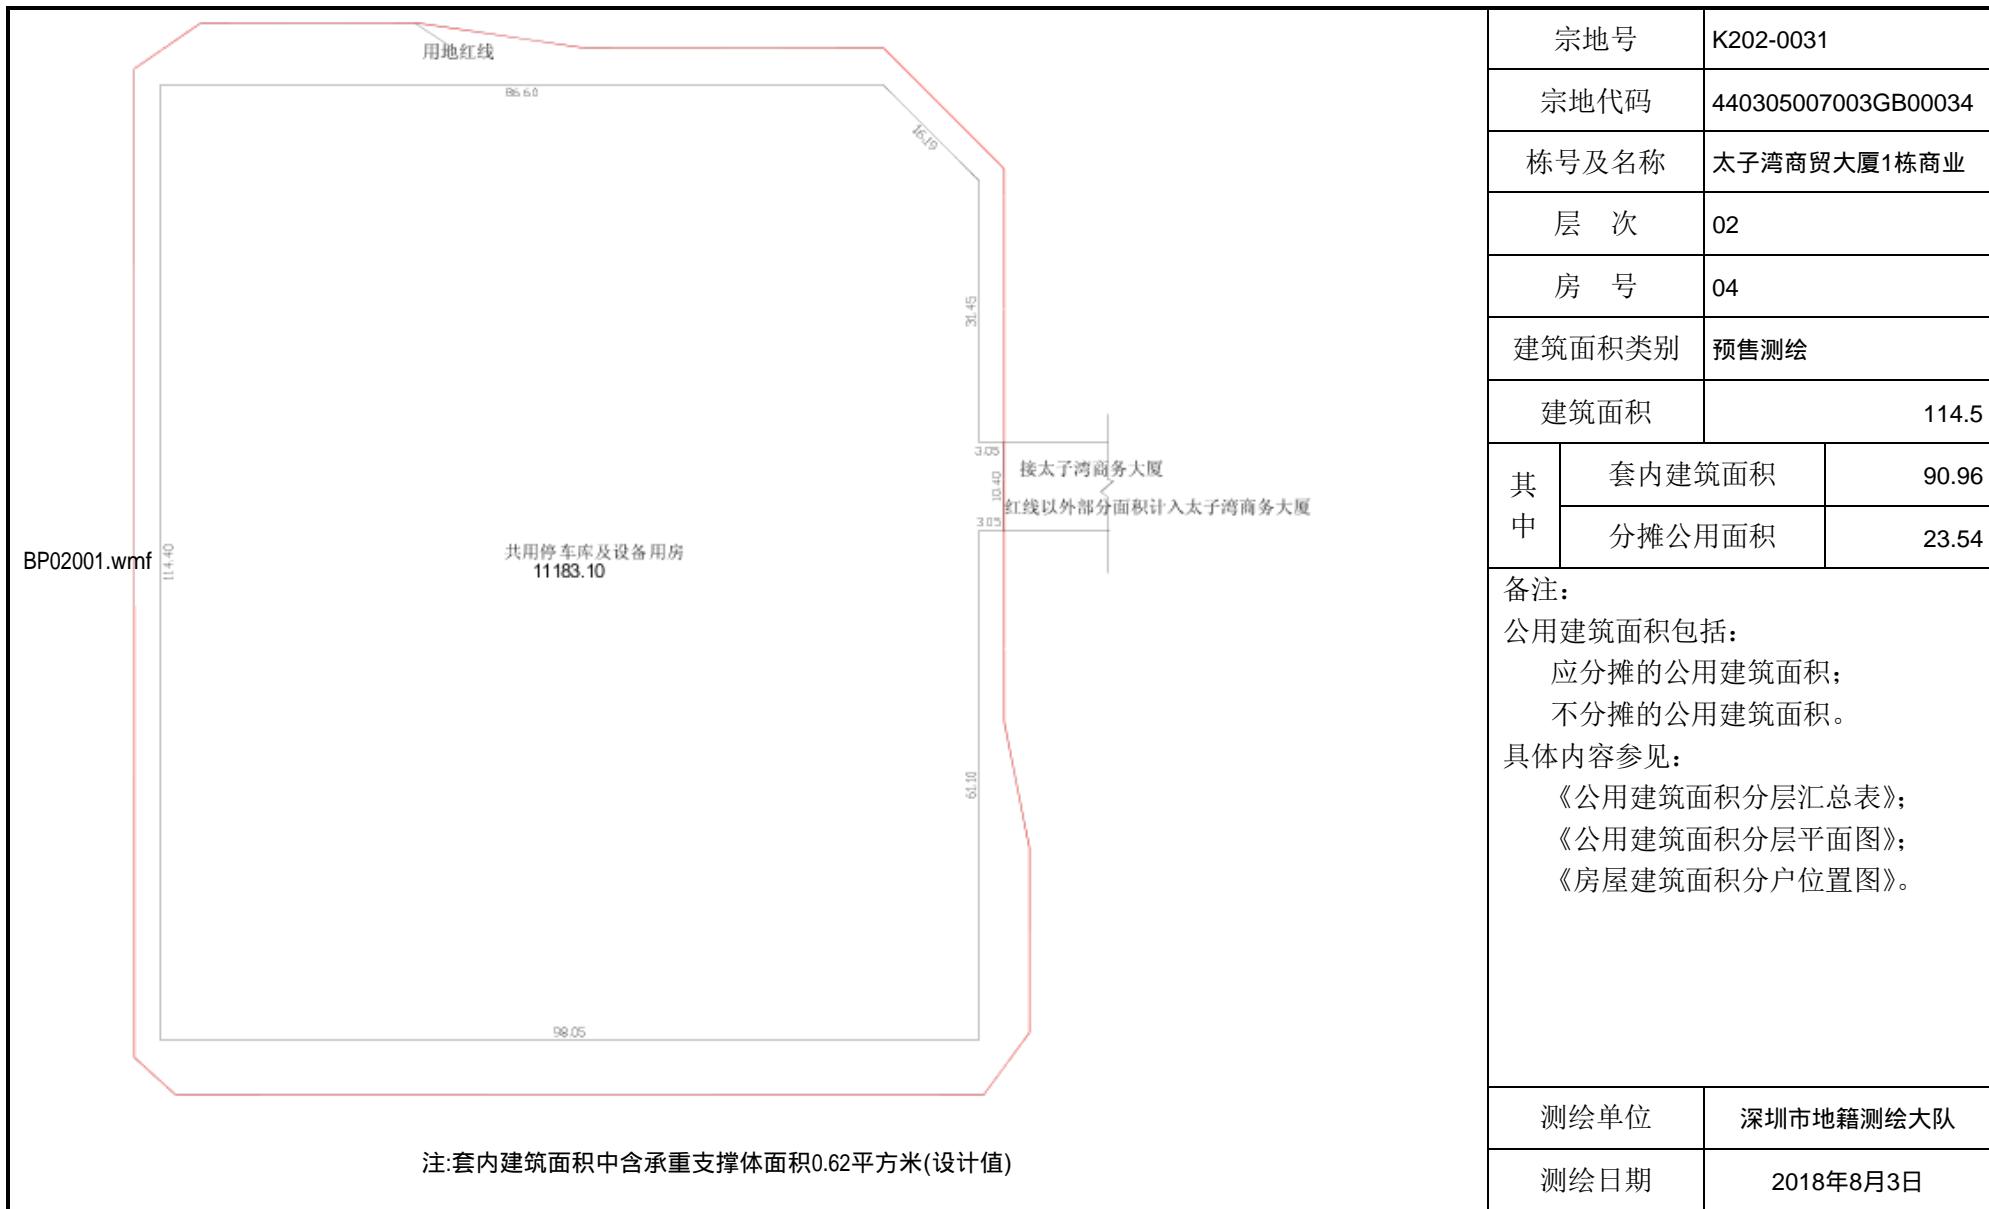


# 房屋建筑面积分户平面图

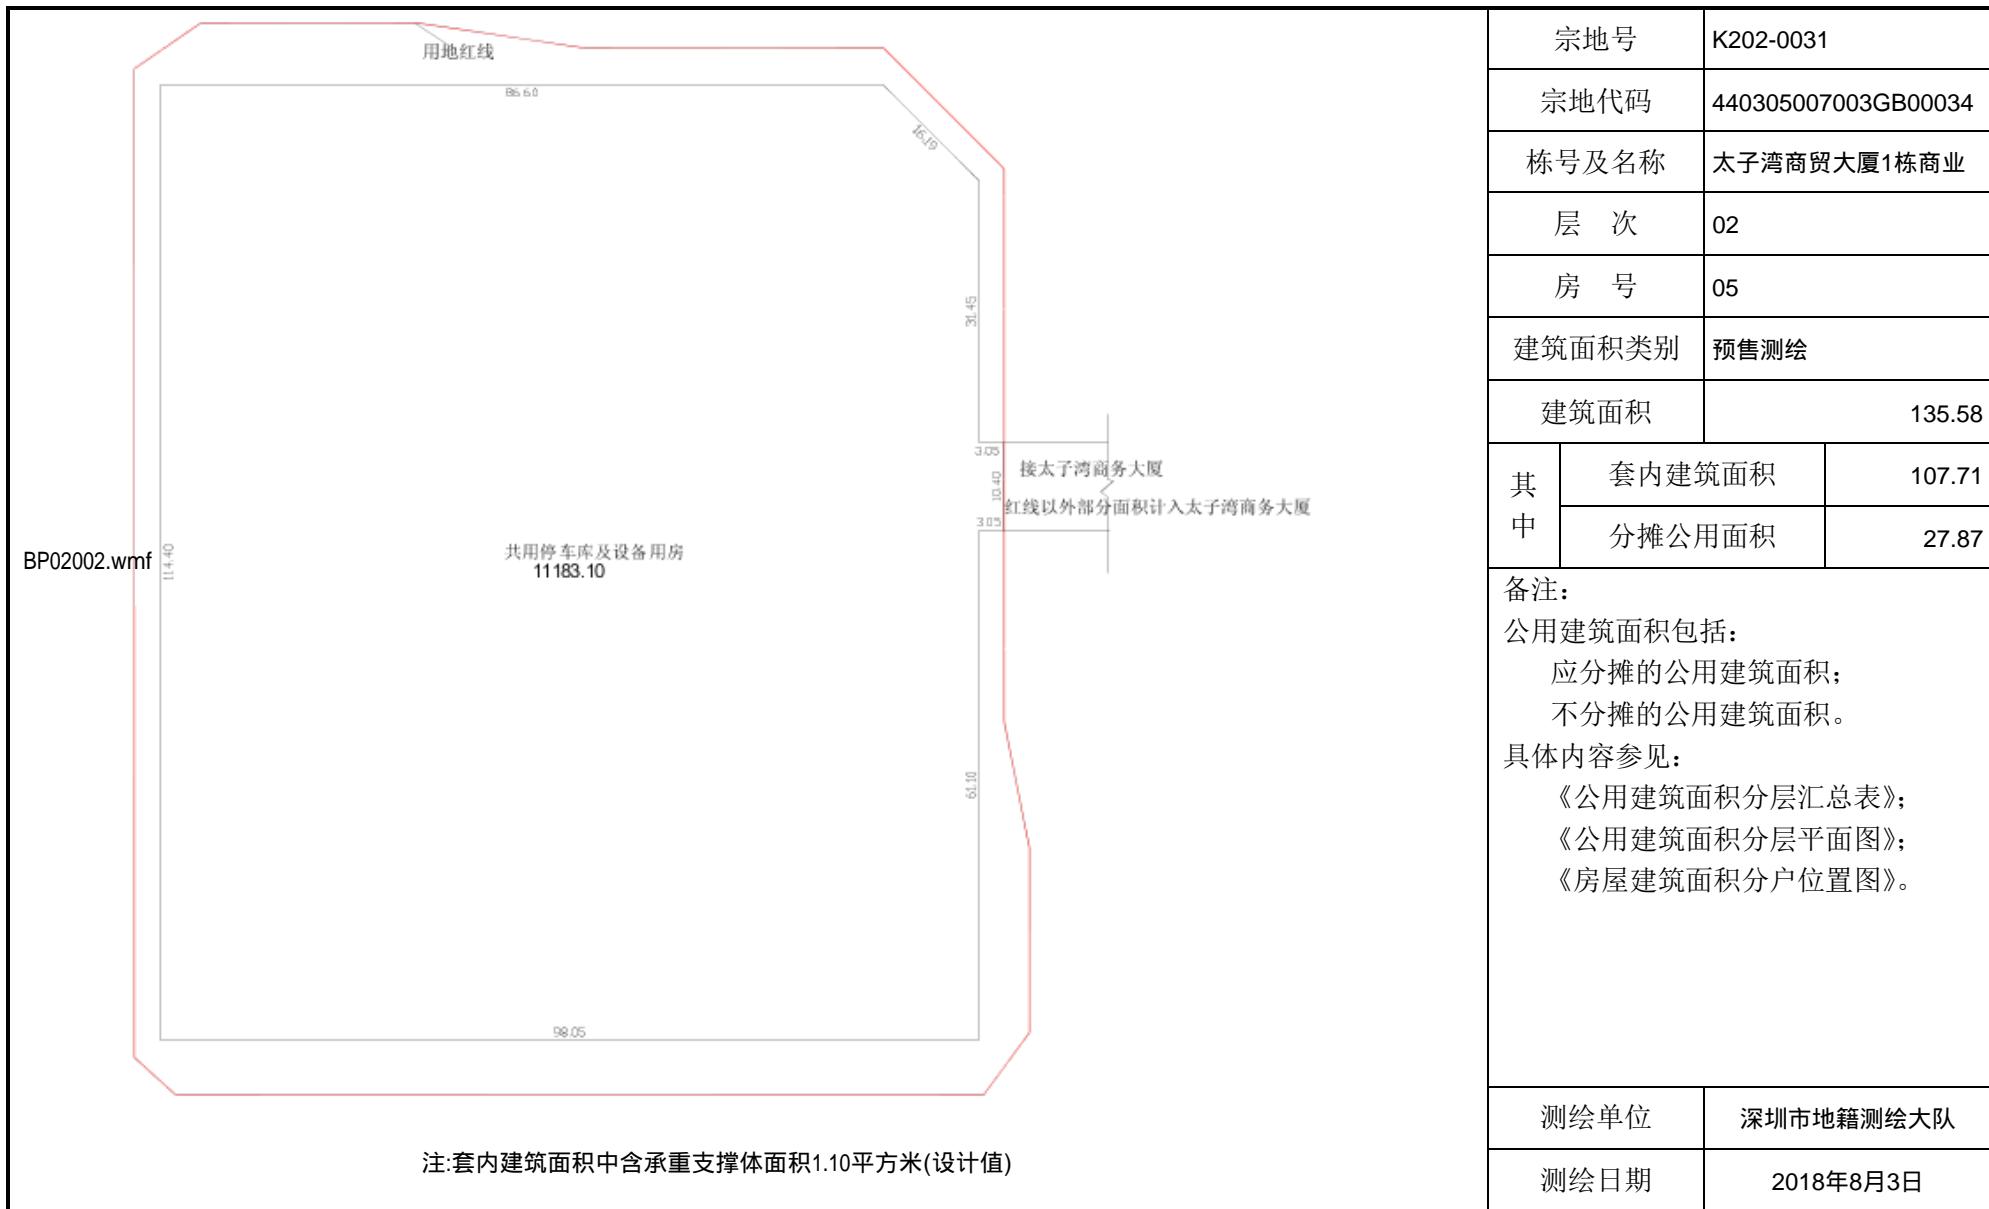


# 房屋建筑面积分户平面图

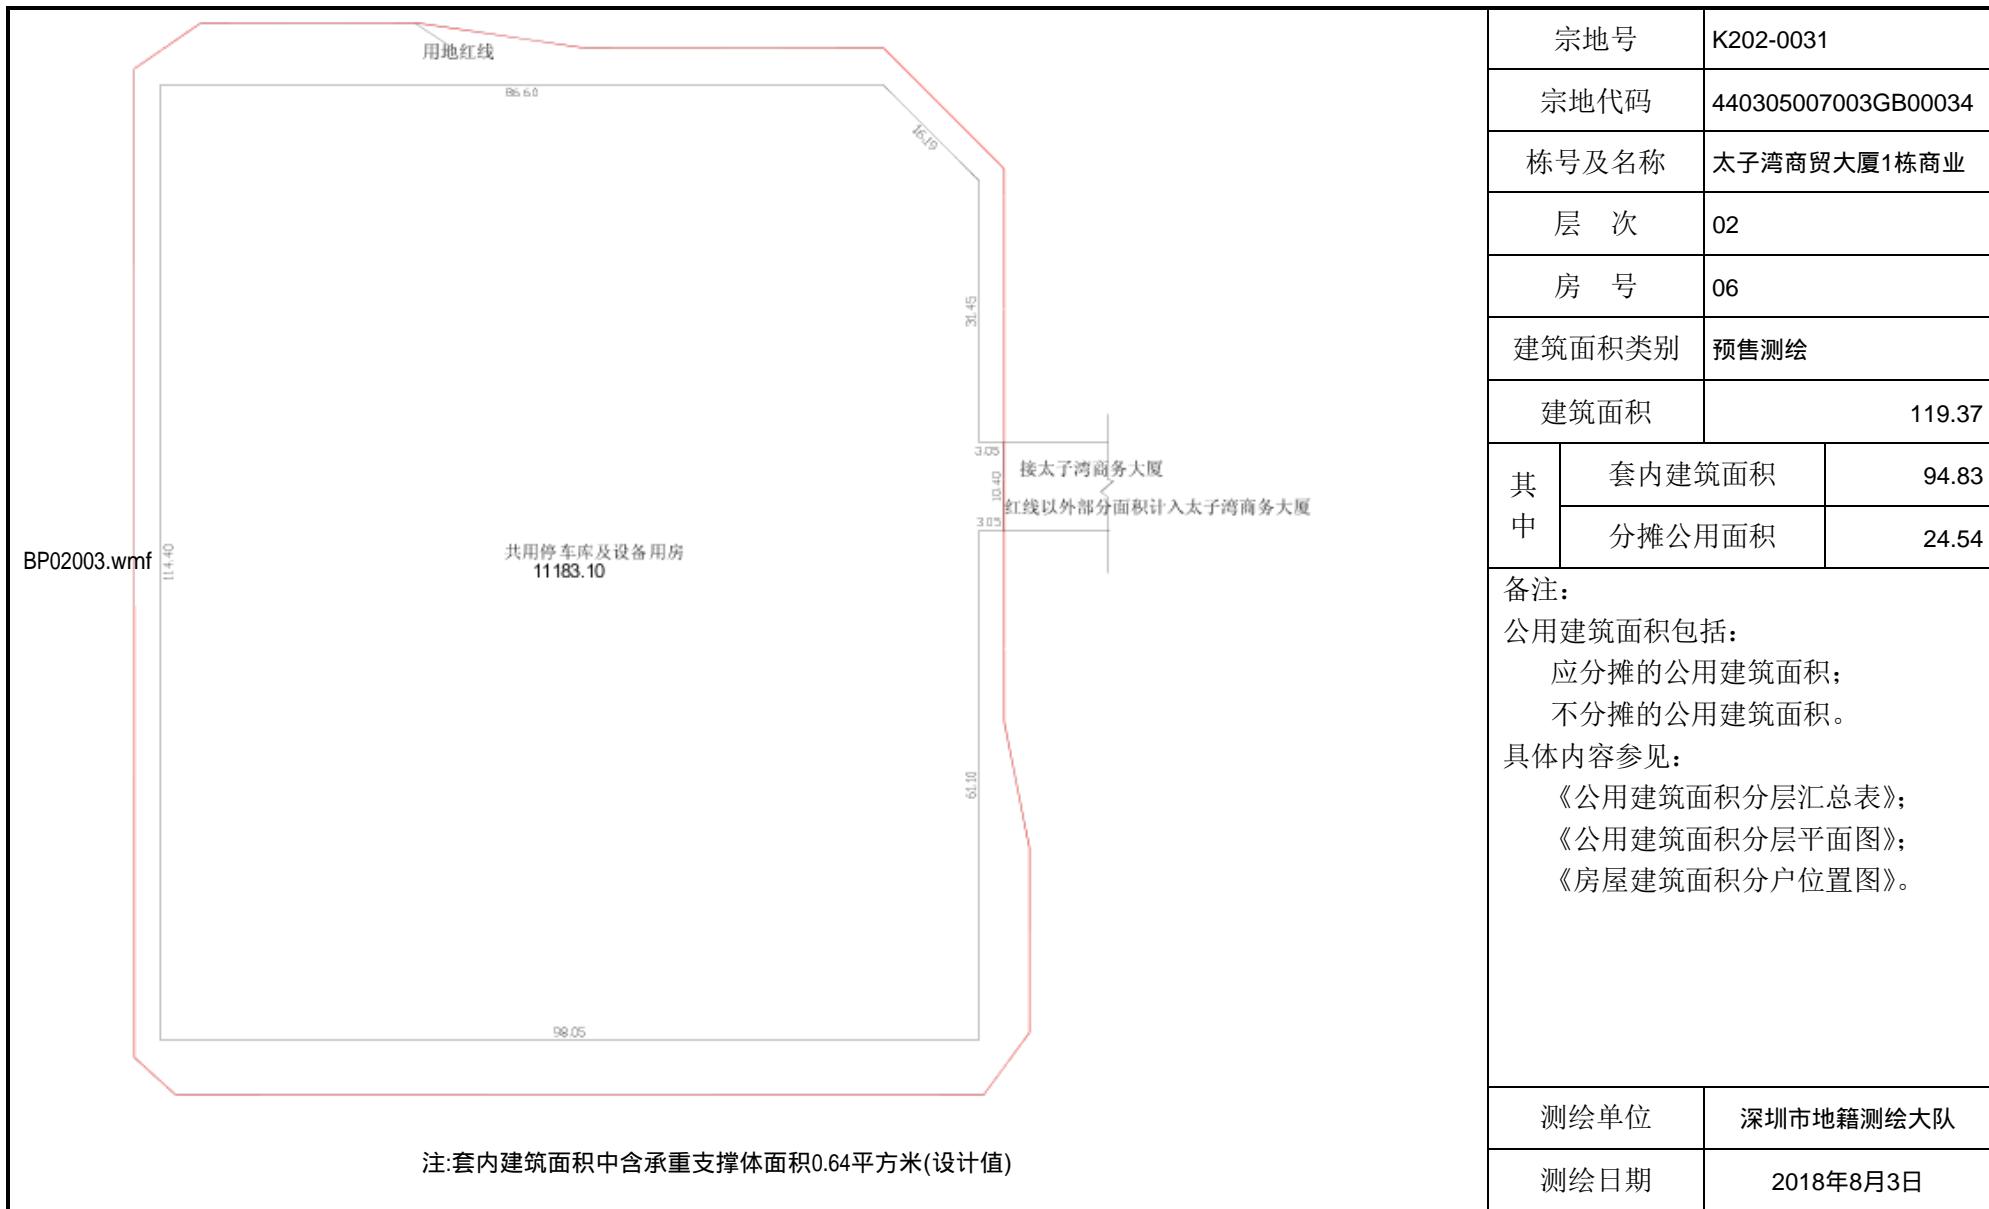


# 房屋建筑面积分户平面图

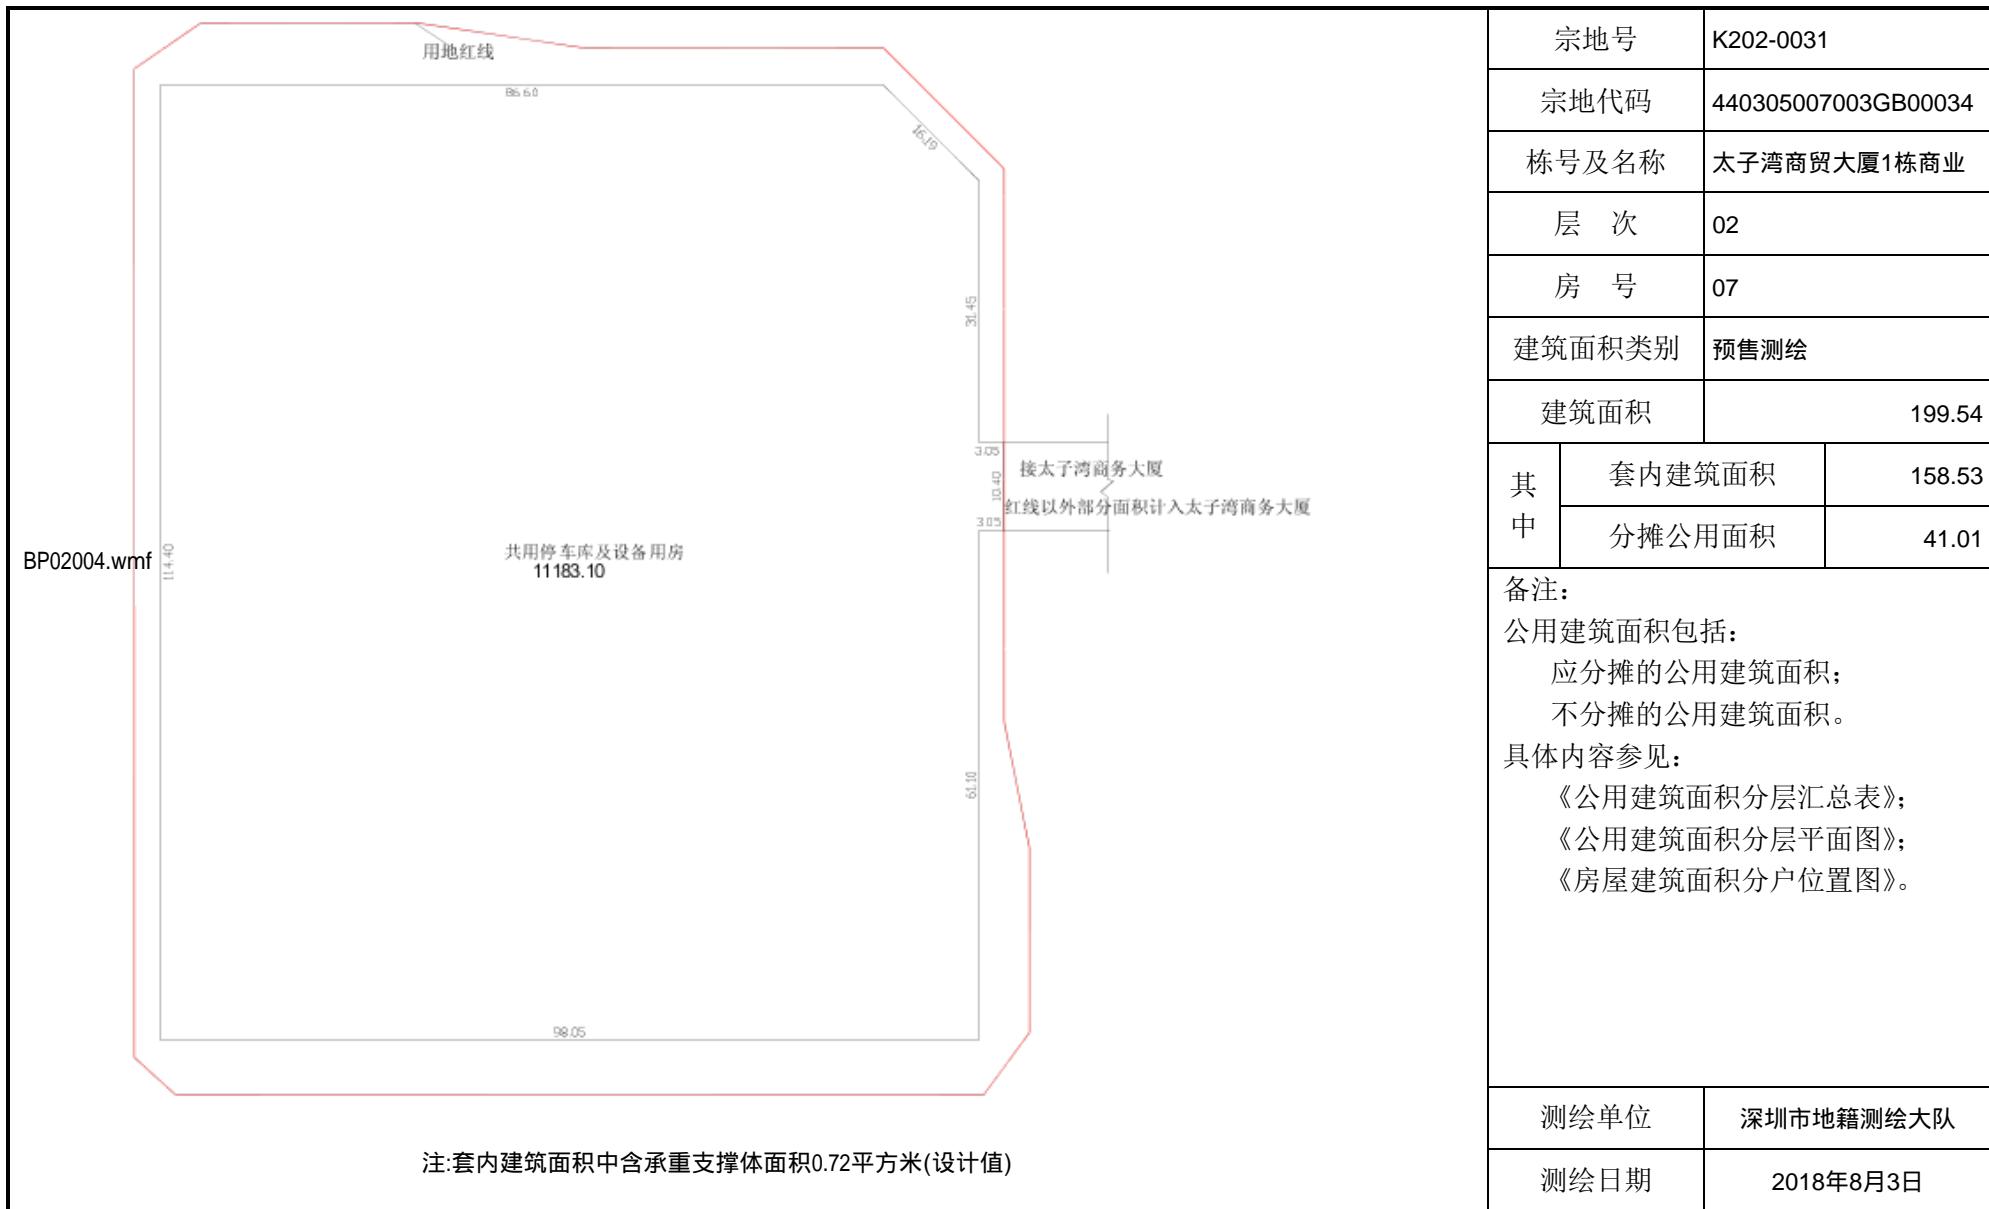


# 房屋建筑面积分户平面图

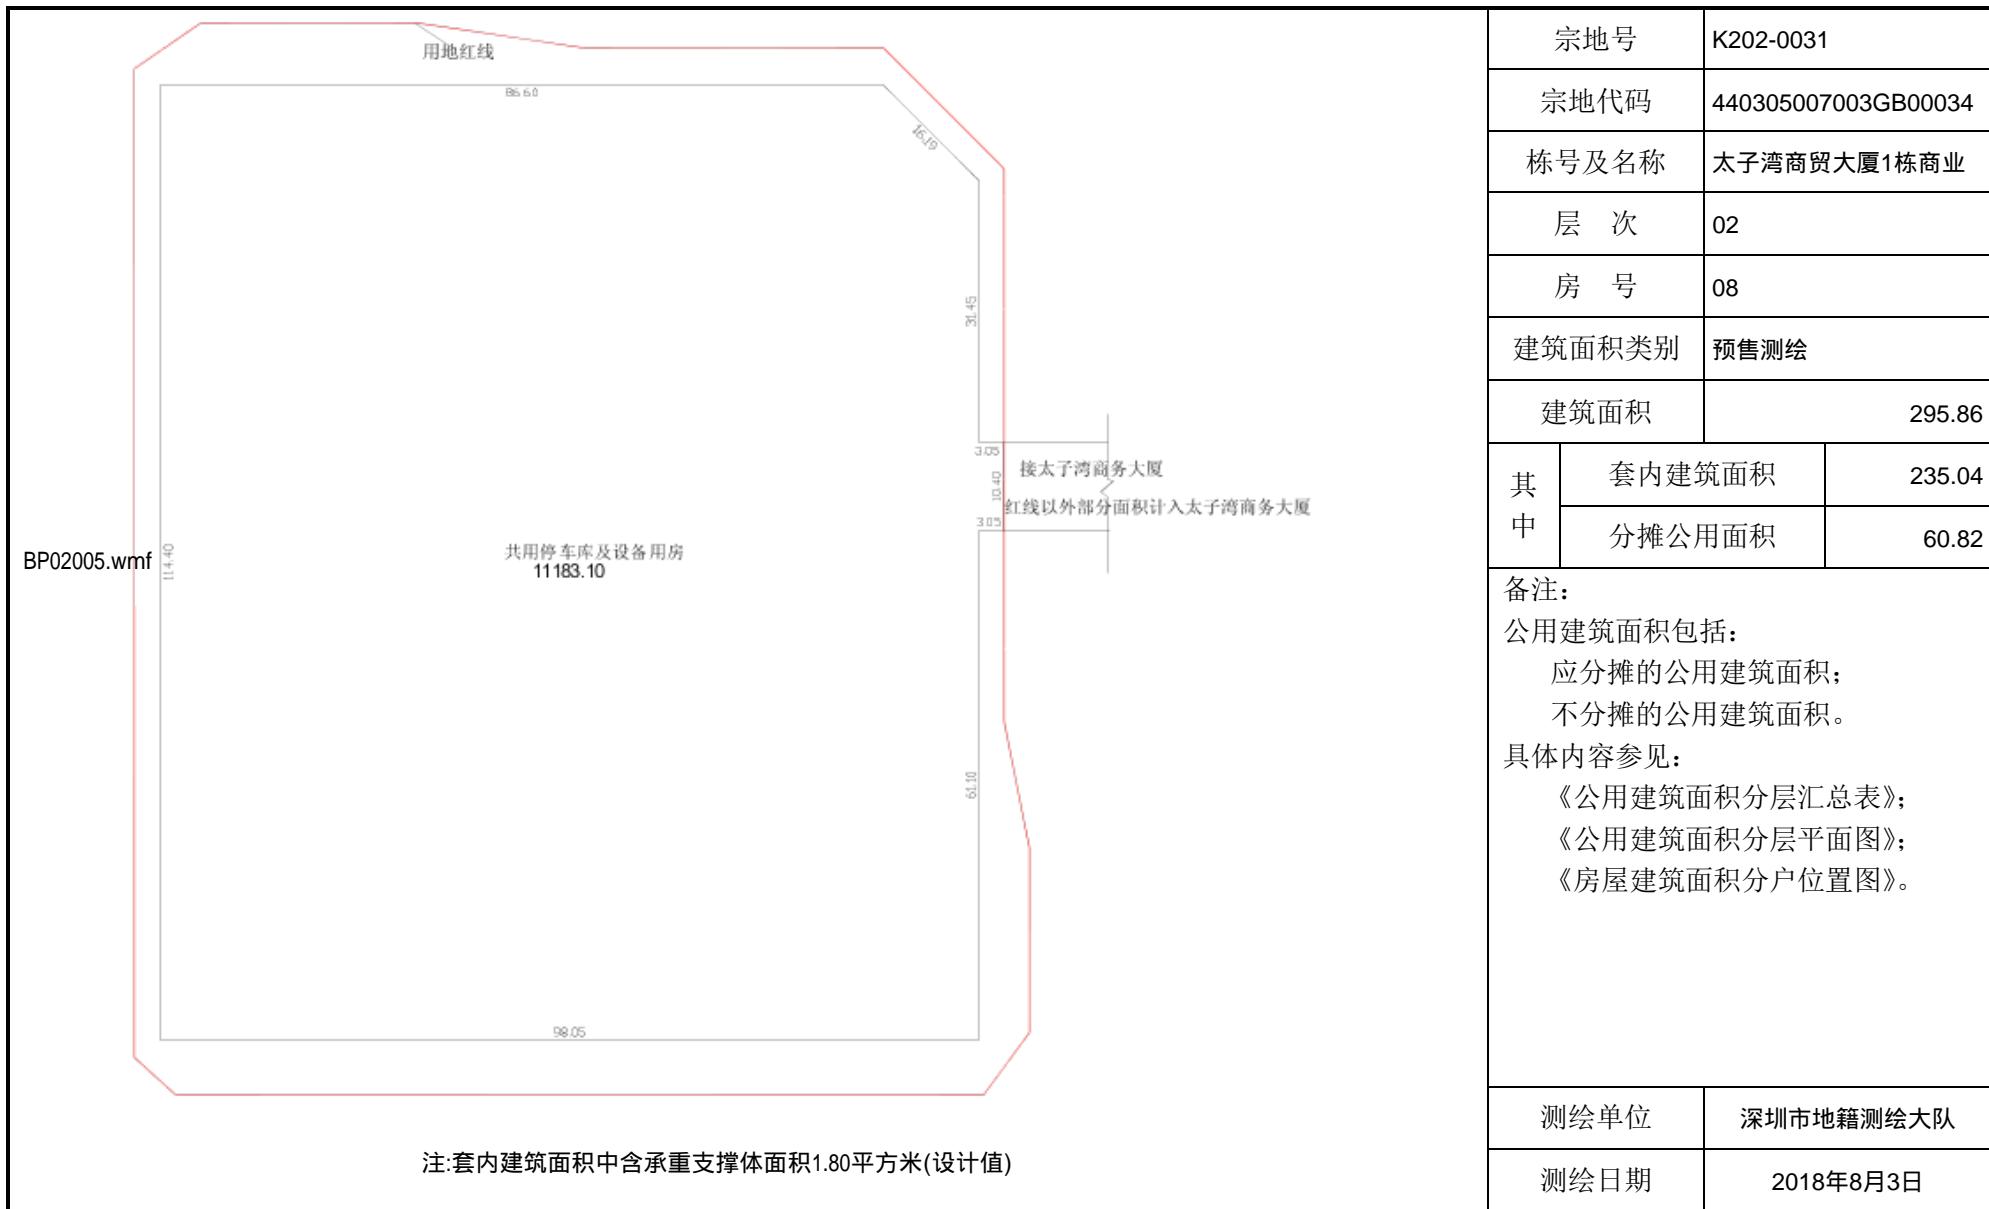


# 房屋建筑面积分户平面图

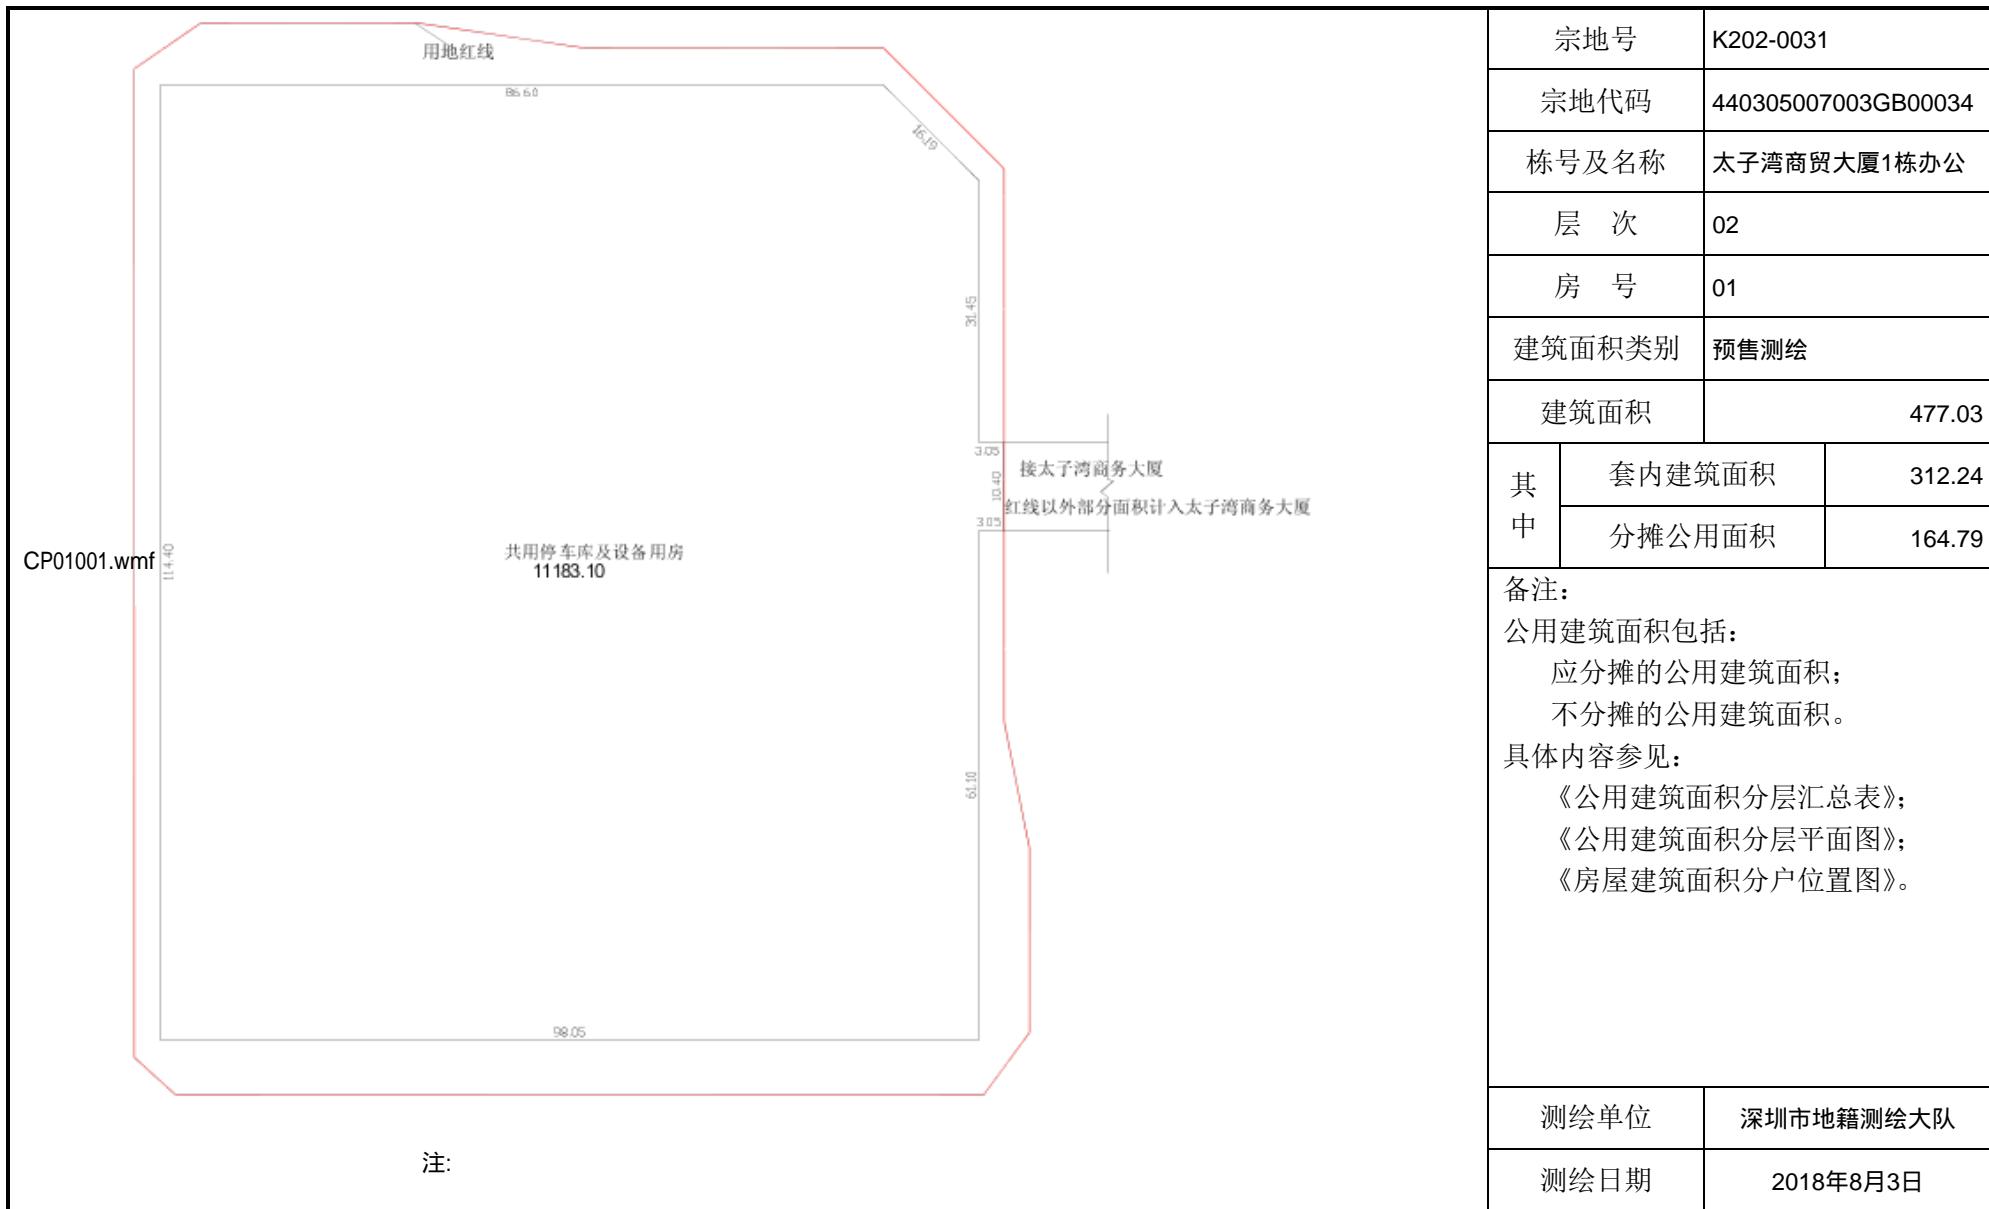

# 房屋建筑面积分户平面图

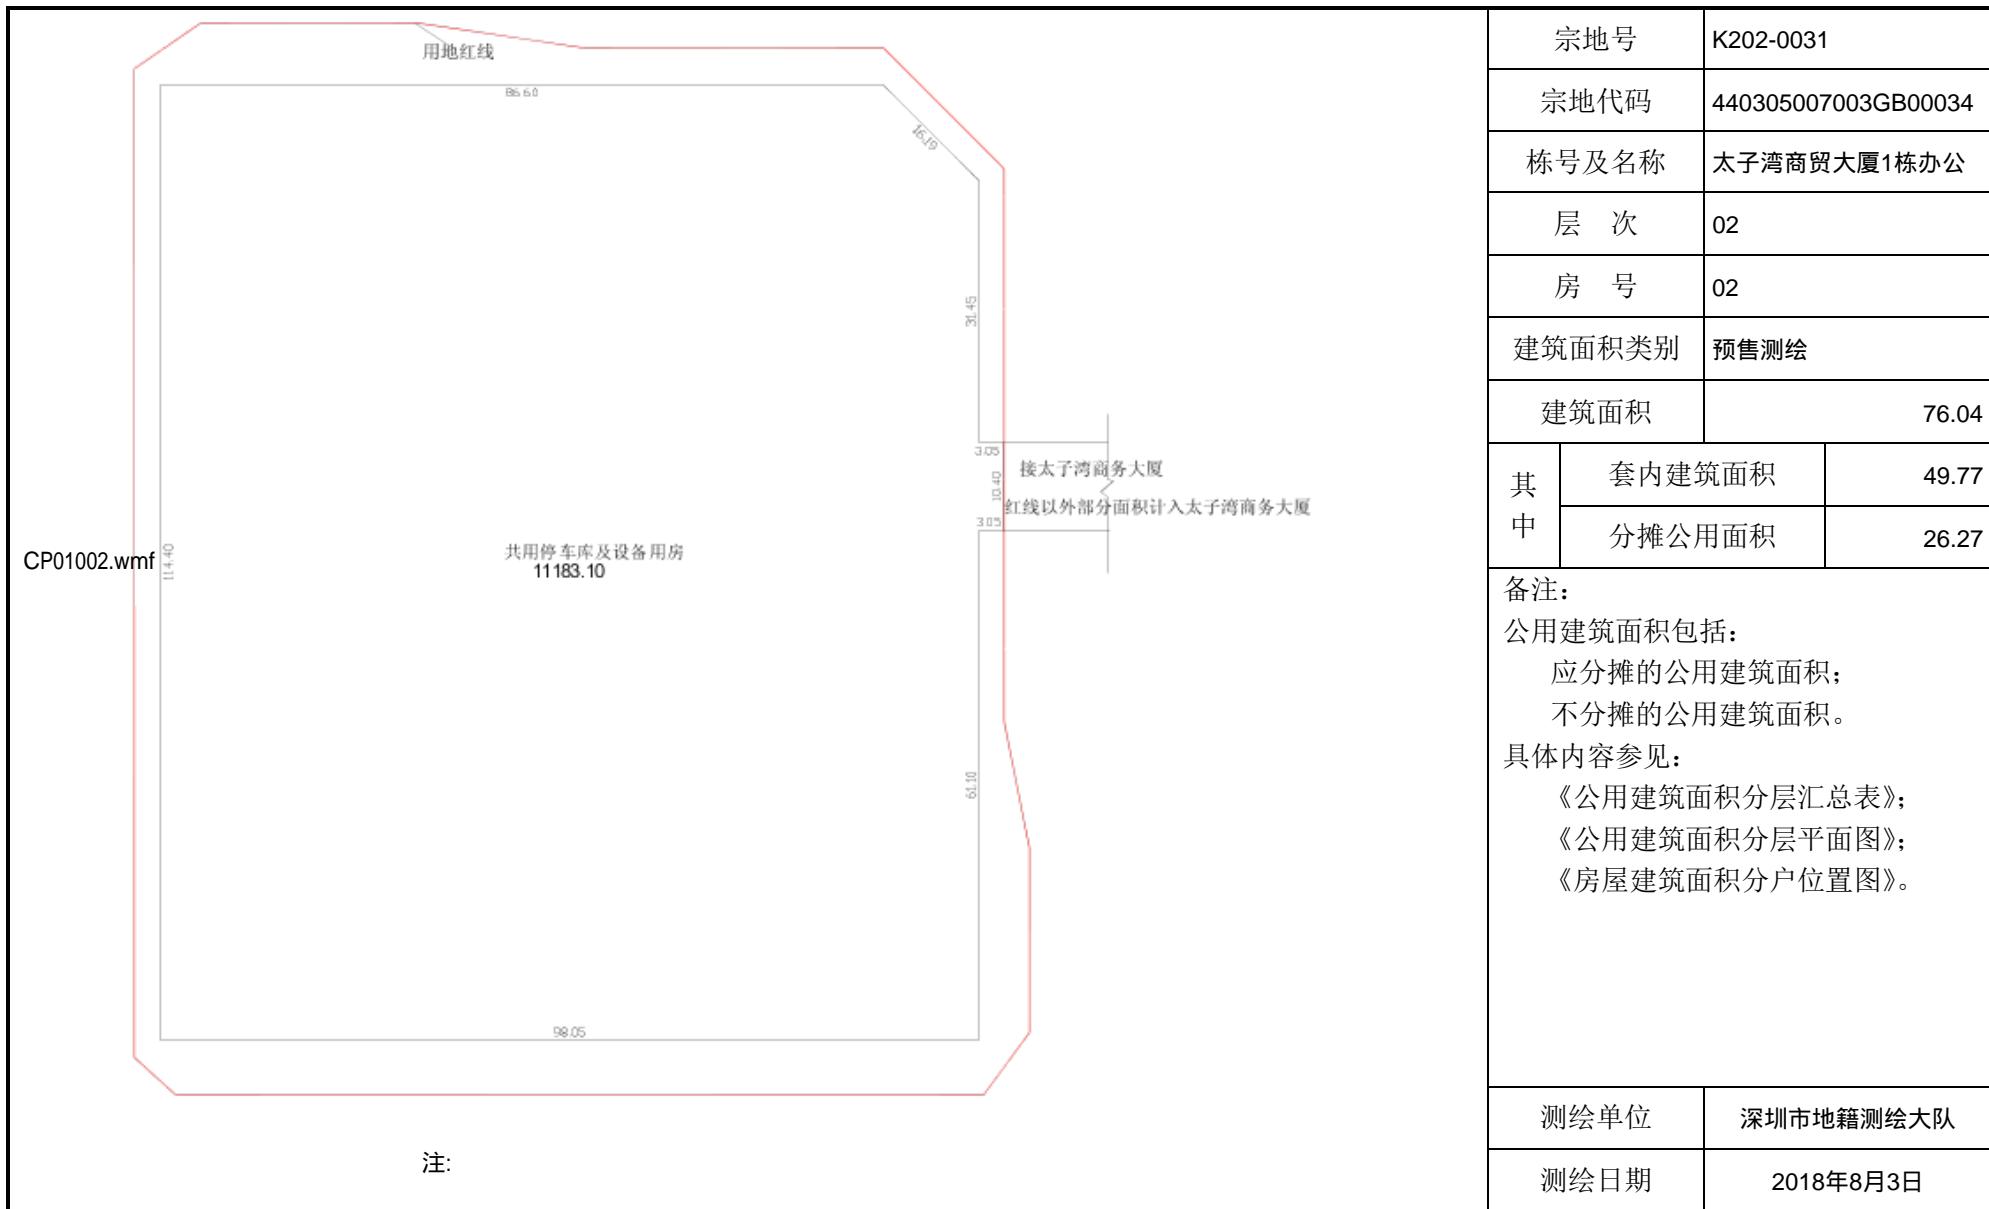


# 房屋建筑面积分户平面图

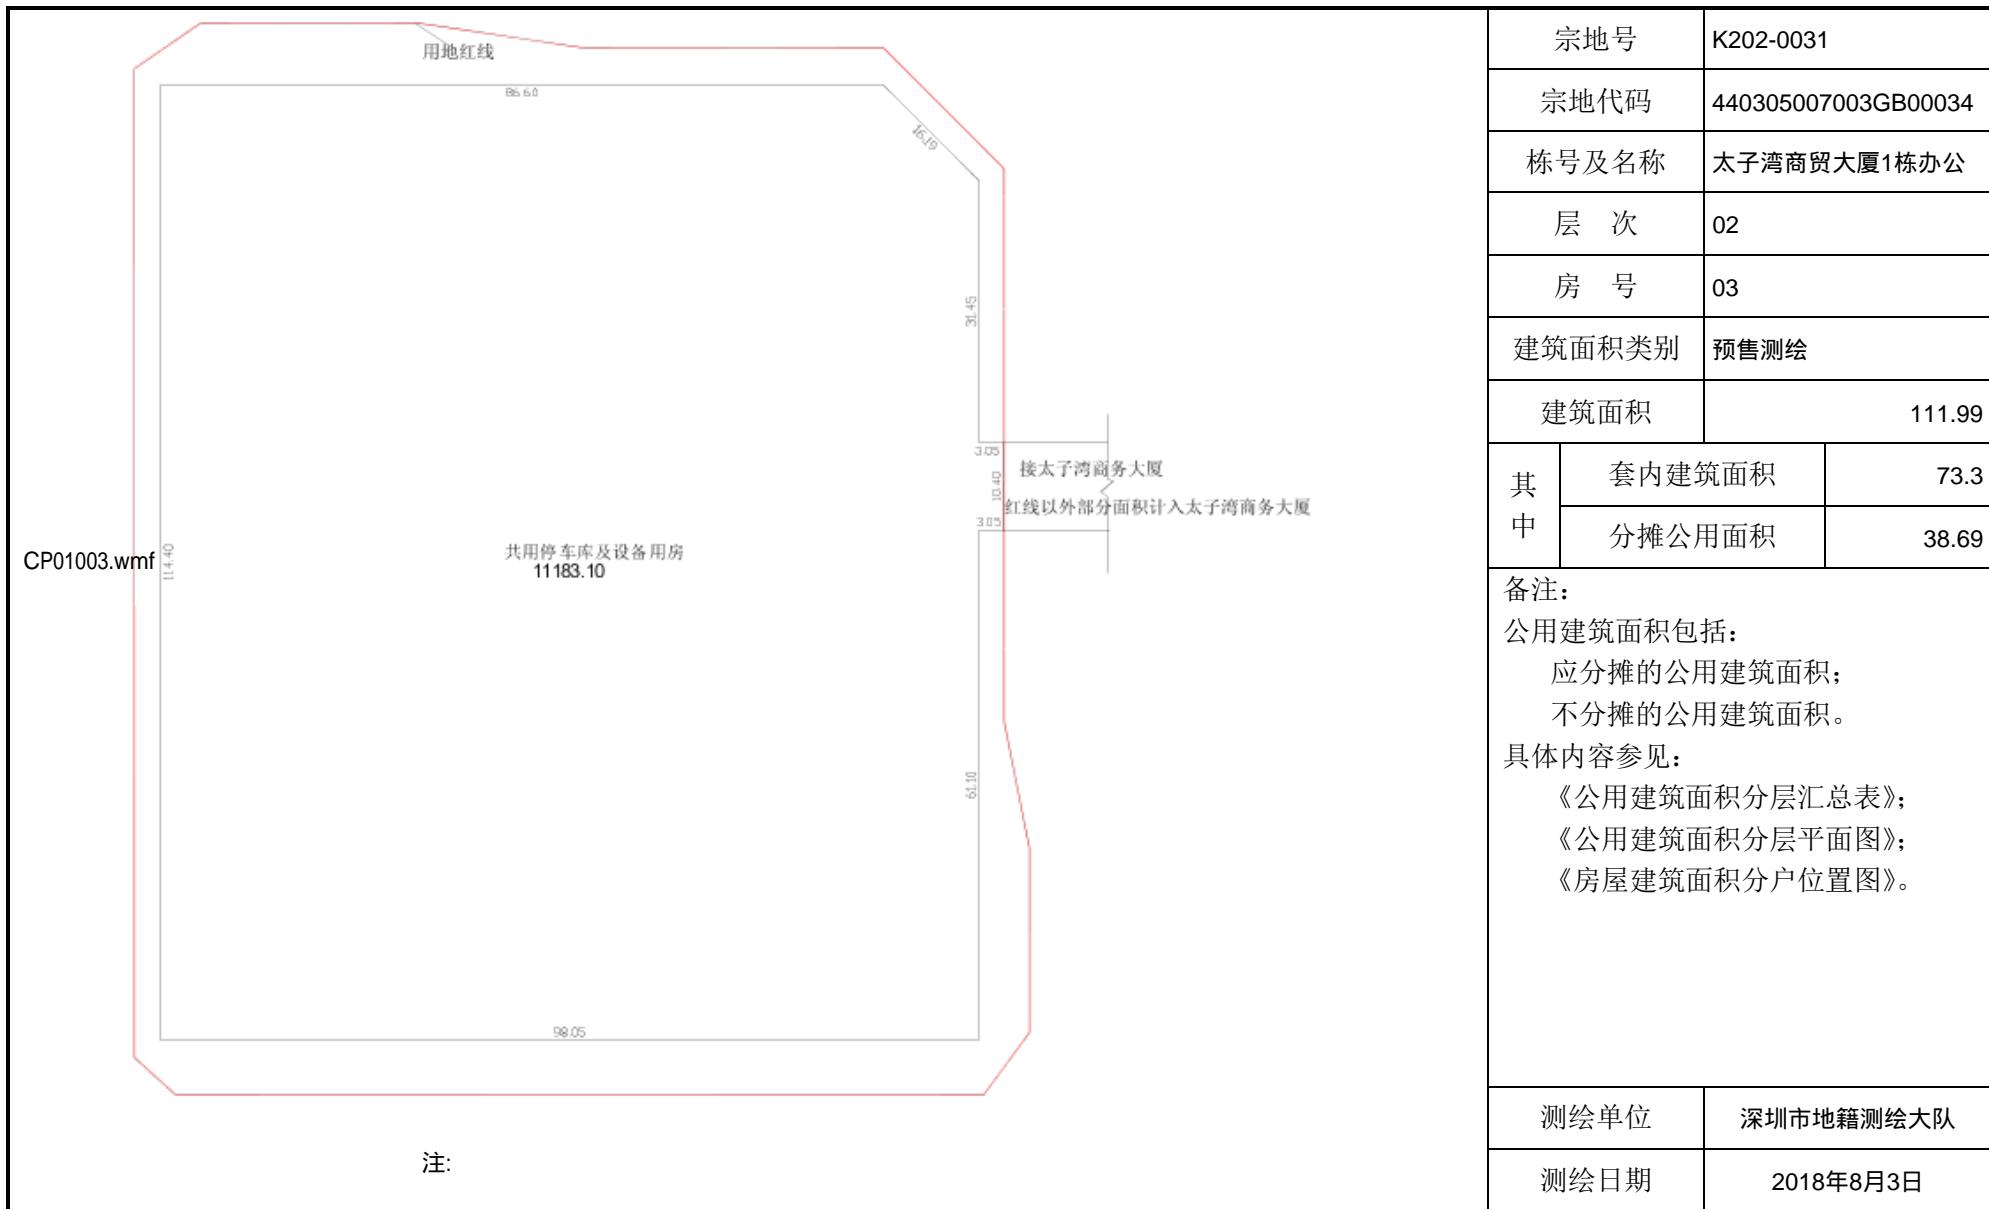


宗地号	K202-0031	
宗地代码	440305007003GB00034	
栋号及名称	太子湾商贸大厦1栋办公	
层 次	02	
房 号	03	
建筑面积类别	预售测绘	
建筑面 积	111.99	
其 中	套内建筑面积	73.3
	分摊公用面积	38.69
备注:		
公用建筑面积包括:		
应分摊的公用建筑面积;		
不分摊的公用建筑面积。		
具体内容参见:		
《公用建筑面积分层汇总表》;		
《公用建筑面积分层平面图》;		
《房屋建筑面积分户位置图》。		
测绘单位	深圳市地籍测绘大队	
测绘日期	2018年8月3日	

# 房屋建筑面积分户平面图

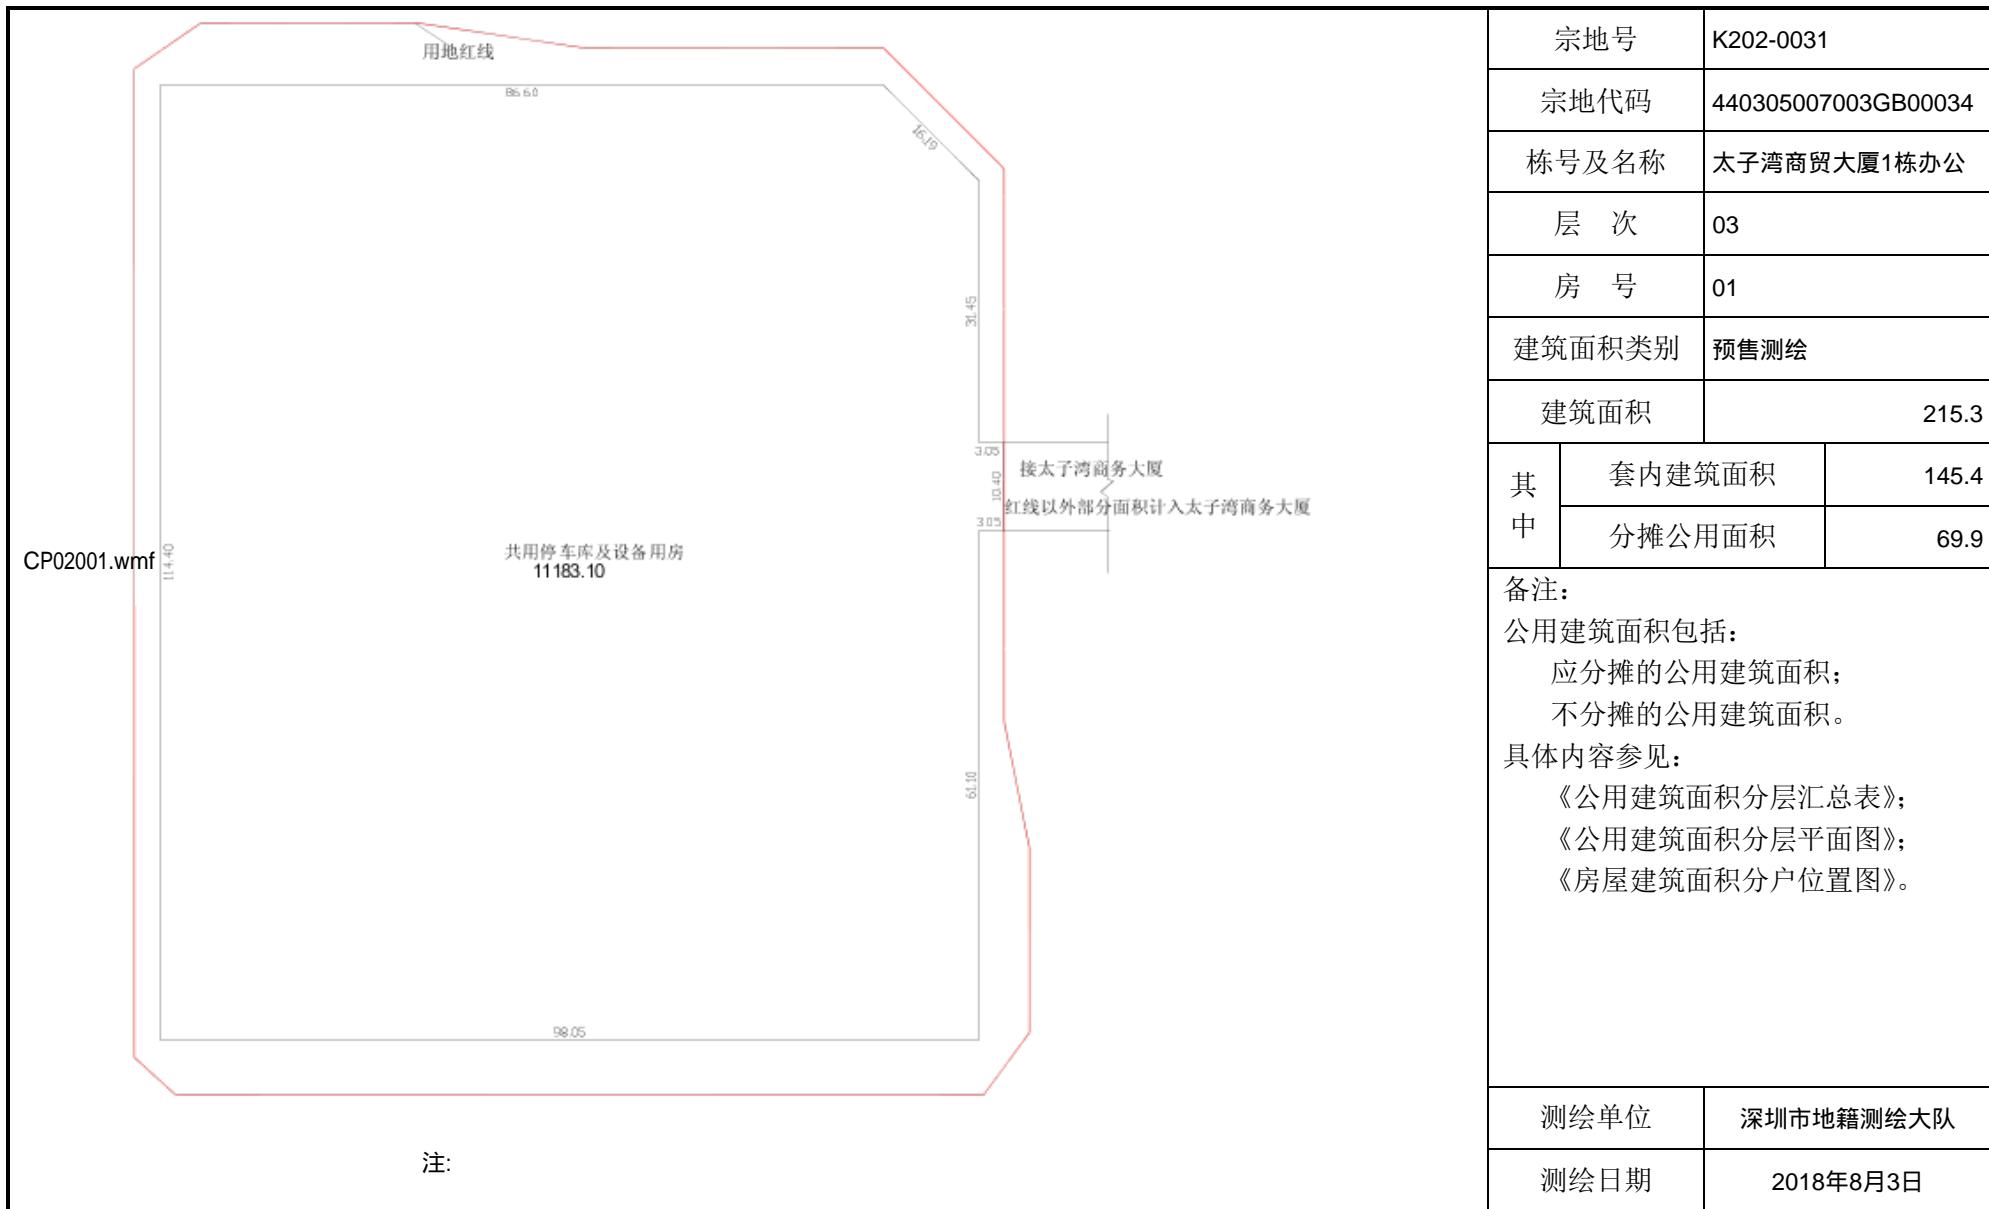


# 房屋建筑面积分户平面图

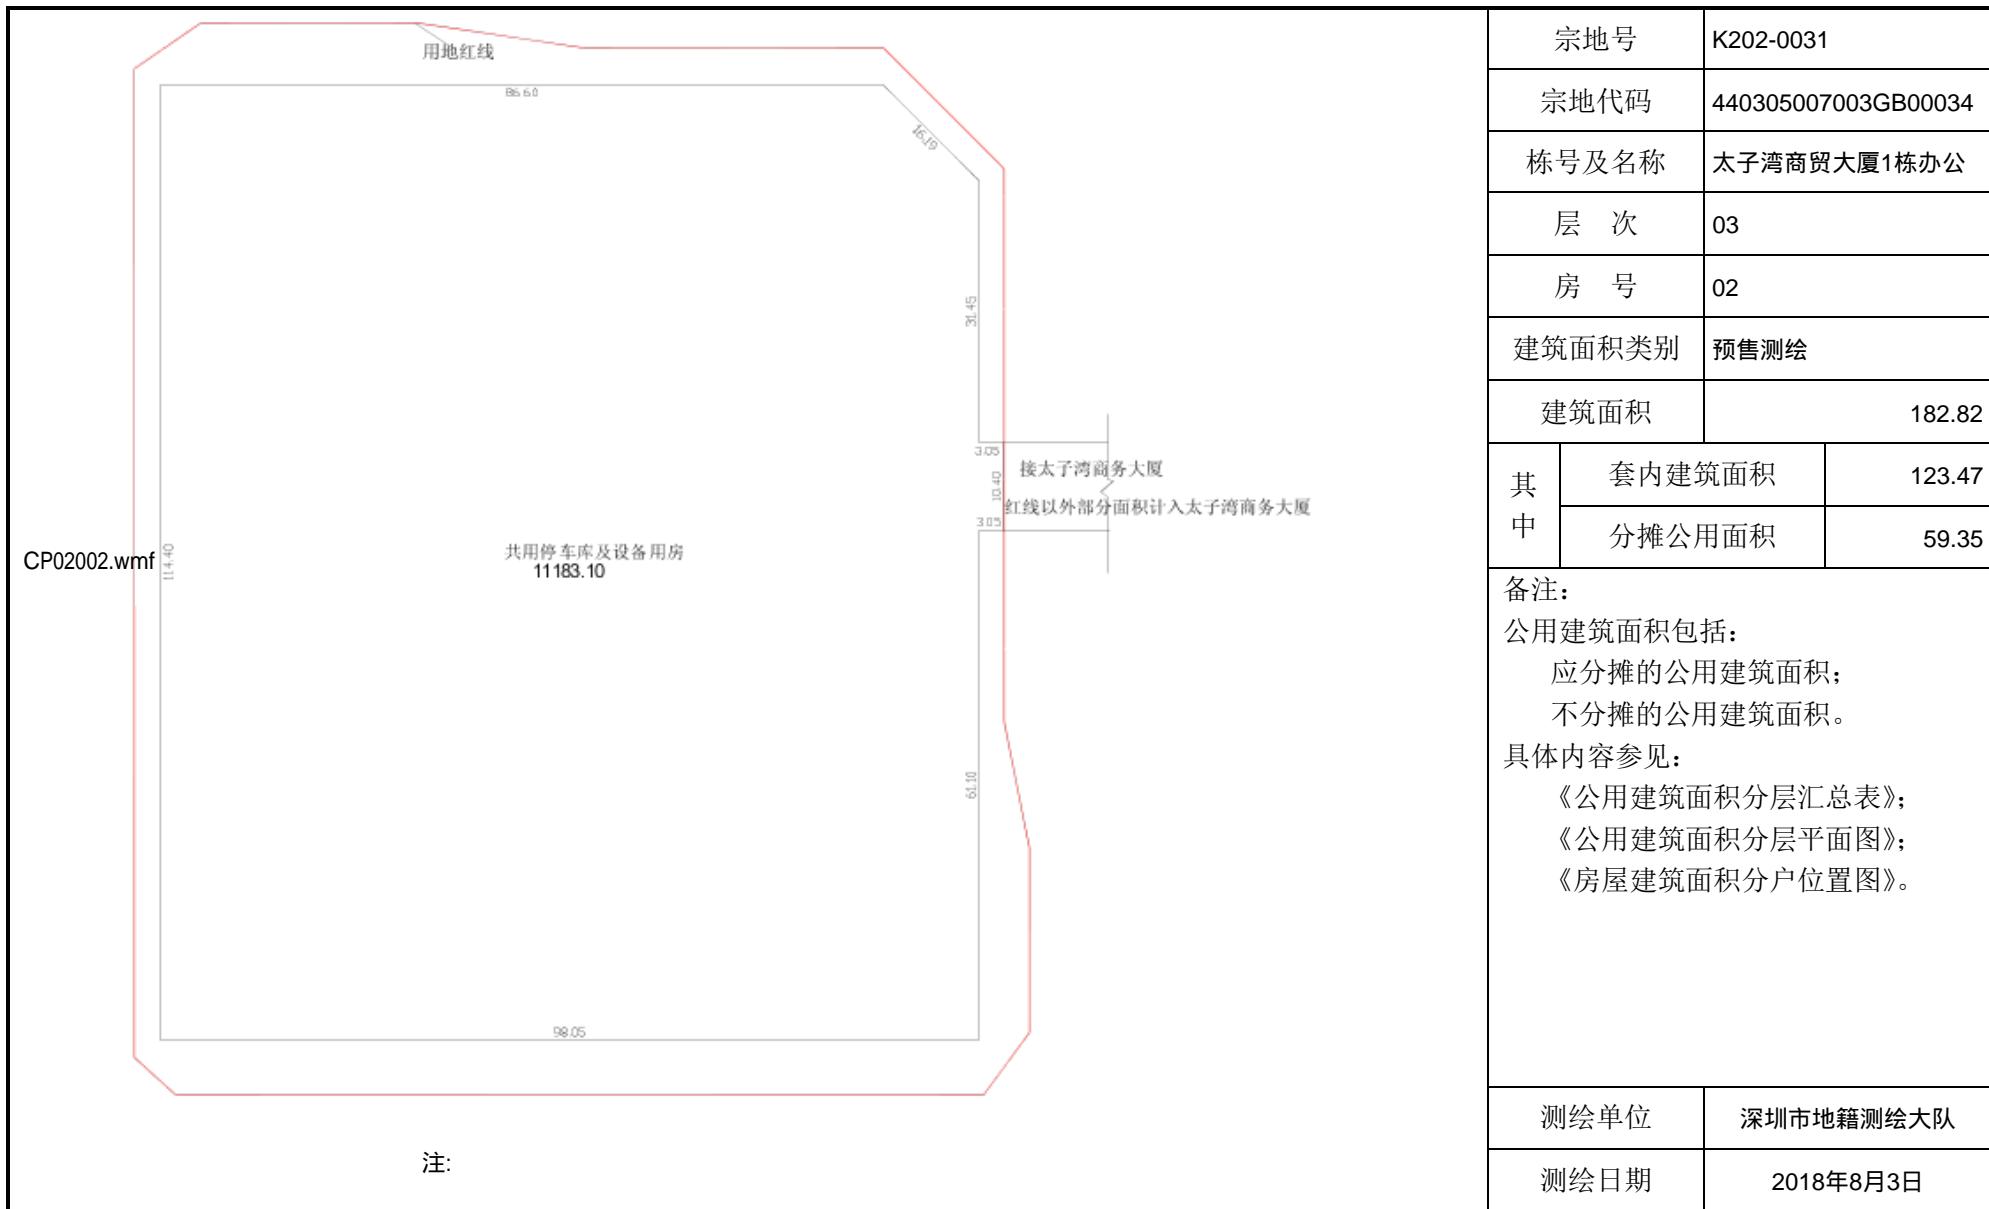


宗地号	K202-0031	
宗地代码	440305007003GB00034	
栋号及名称	太子湾商贸大厦1栋办公	
层 次	03	
房 号	02	
建筑面积类别	预售测绘	
建筑面 积	182.82	
其 中	套内建筑面积	123.47
	分摊公用面积	59.35
备注:		
公用建筑面积包括:		
应分摊的公用建筑面积;		
不分摊的公用建筑面积。		
具体内容参见:		
《公用建筑面积分层汇总表》;		
《公用建筑面积分层平面图》;		
《房屋建筑面积分户位置图》。		
测绘单位	深圳市地籍测绘大队	
测绘日期	2018年8月3日	

# 房屋建筑面积分户平面图

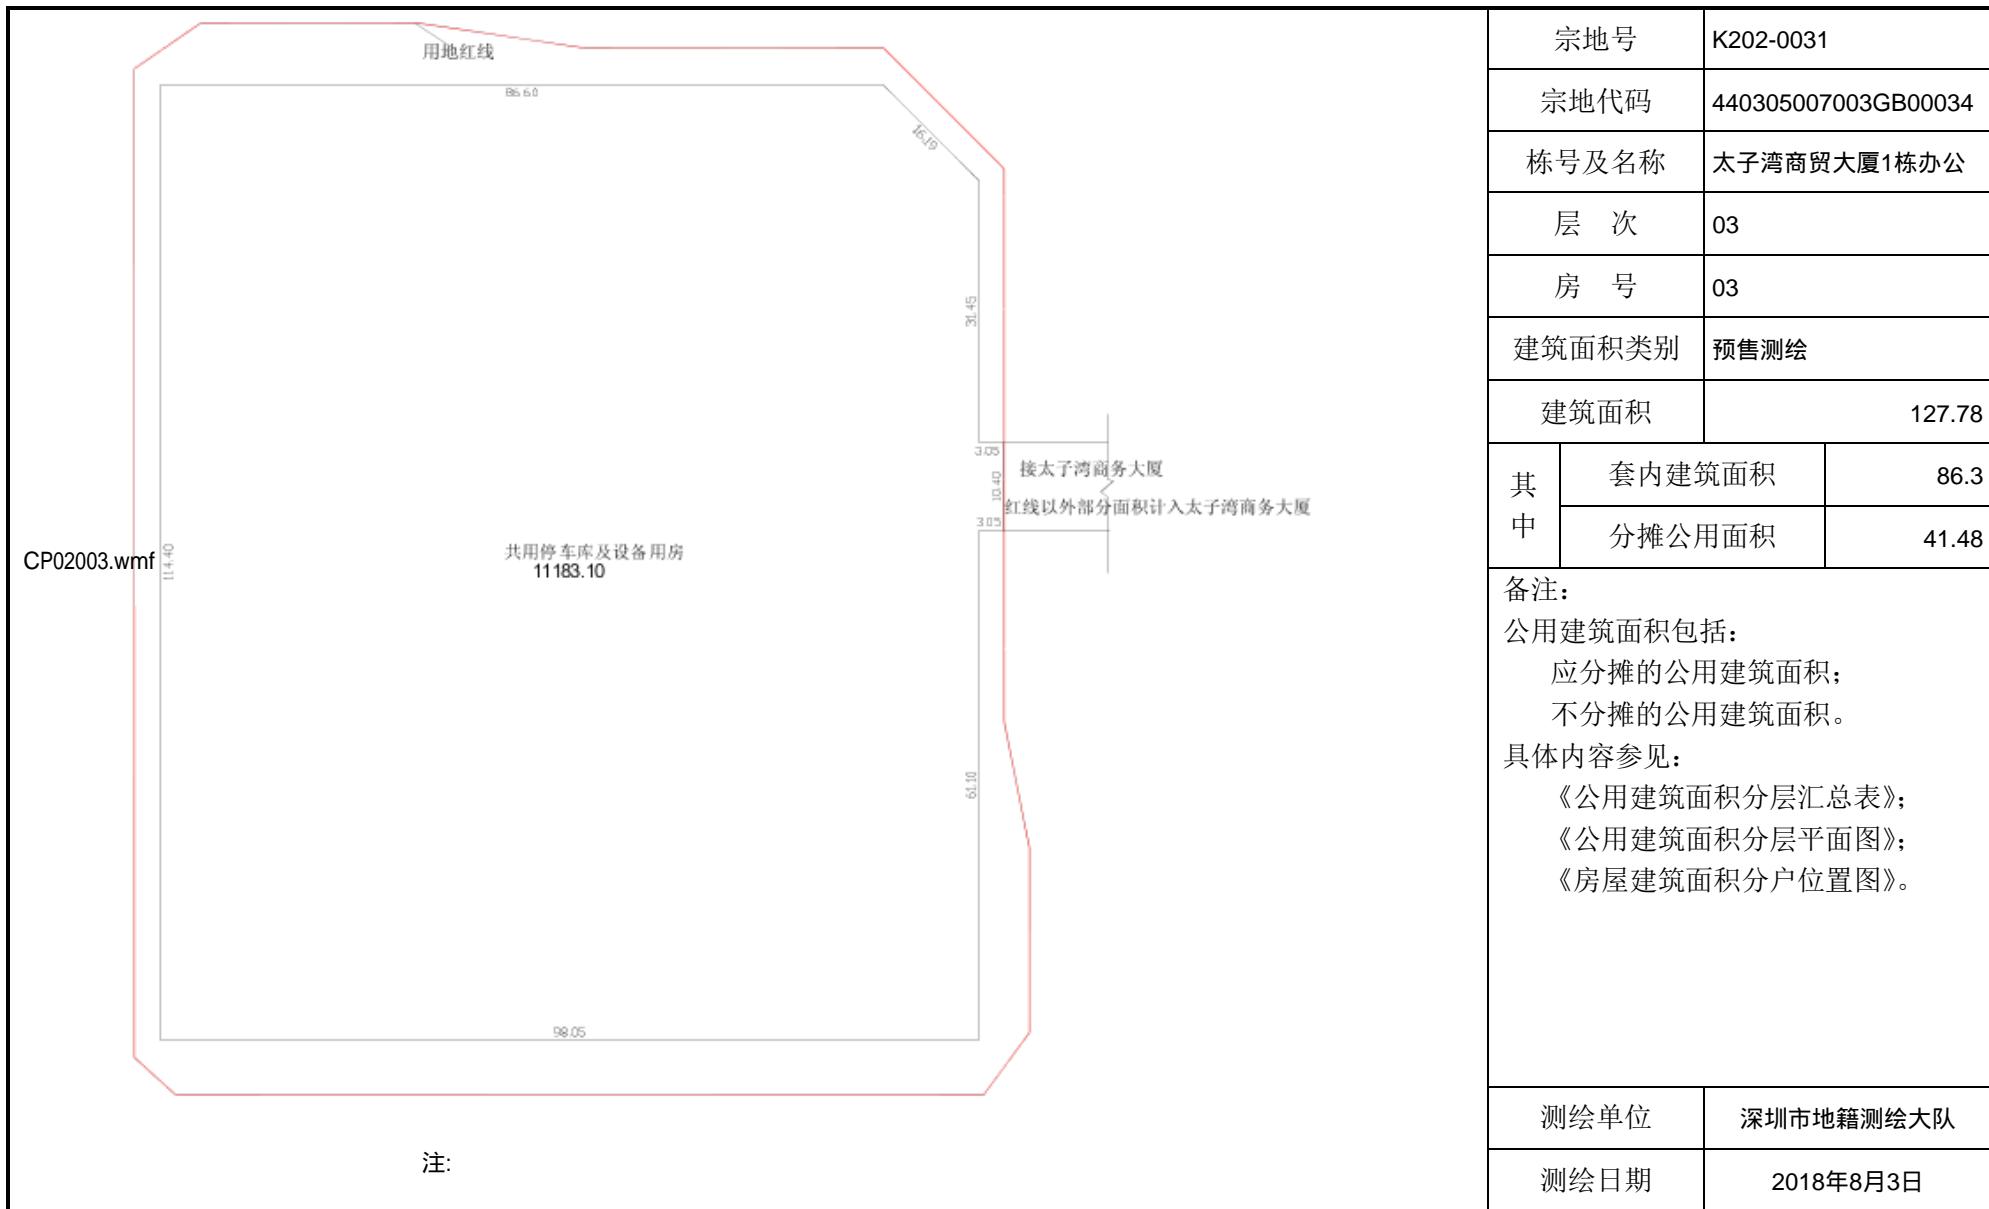


宗地号	K202-0031	
宗地代码	440305007003GB00034	
栋号及名称	太子湾商贸大厦1栋办公	
层 次	03	
房 号	03	
建筑面积类别	预售测绘	
建筑面 积	127.78	
其 中	套内建筑面积	86.3
	分摊公用面积	41.48
备注:		
公用建筑面积包括:		
应分摊的公用建筑面积;		
不分摊的公用建筑面积。		
具体内容参见:		
《公用建筑面积分层汇总表》;		
《公用建筑面积分层平面图》;		
《房屋建筑面积分户位置图》。		
测绘单位	深圳市地籍测绘大队	
测绘日期	2018年8月3日	

# 房屋建筑面积分户平面图

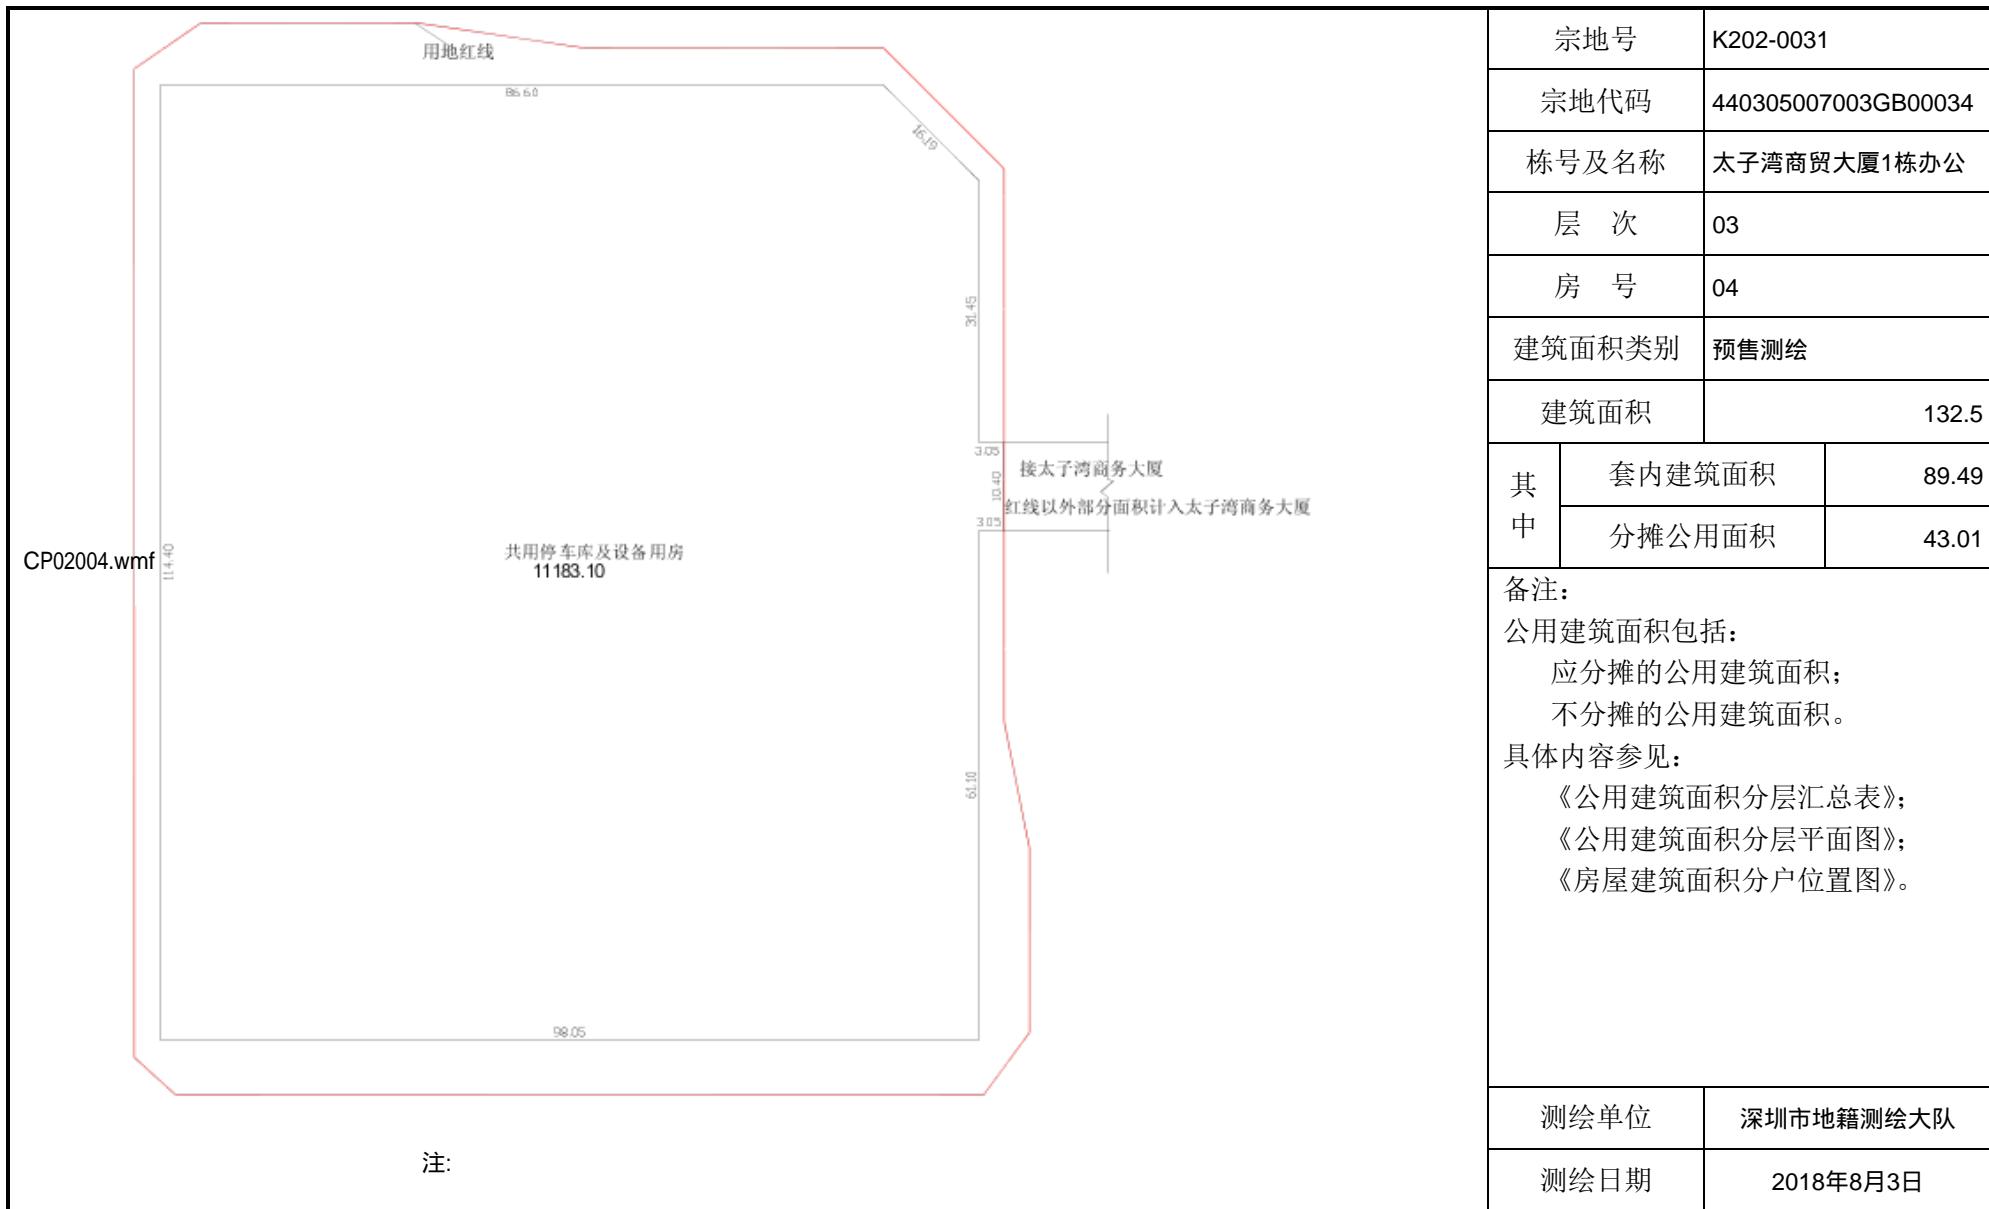


# 房屋建筑面积分户平面图

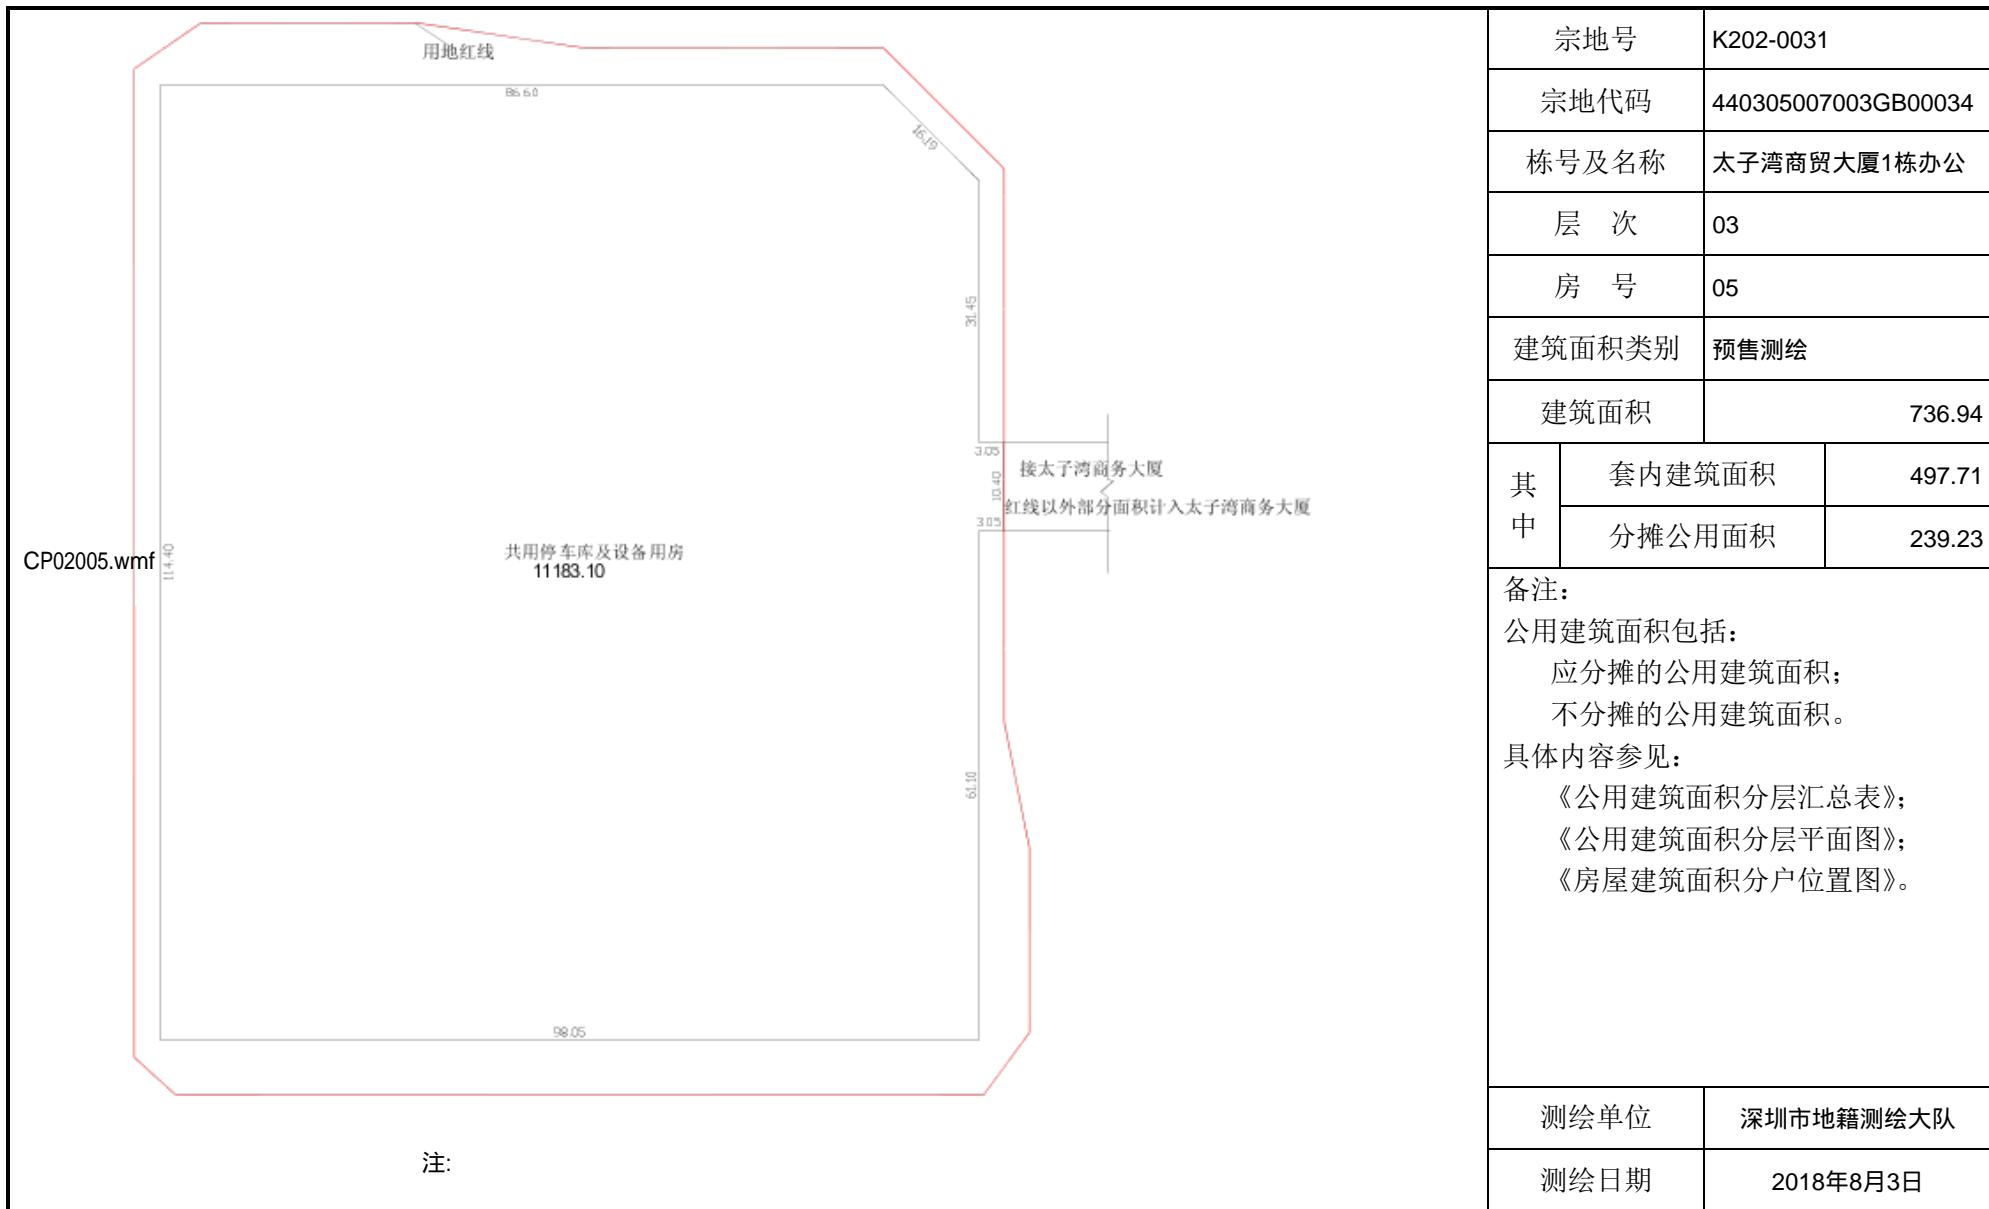


宗地号	K202-0031	
宗地代码	440305007003GB00034	
栋号及名称	太子湾商贸大厦1栋办公	
层 次	03	
房 号	05	
建筑面积类别	预售测绘	
建筑面 积	736.94	
其 中	套内建筑面积	497.71
	分摊公用面积	239.23
备注:		
公用建筑面积包括:		
应分摊的公用建筑面积;		
不分摊的公用建筑面积。		
具体内容参见:		
《公用建筑面积分层汇总表》;		
《公用建筑面积分层平面图》;		
《房屋建筑面积分户位置图》。		
测绘单位	深圳市地籍测绘大队	
测绘日期	2018年8月3日	

# 房屋建筑面积分户平面图

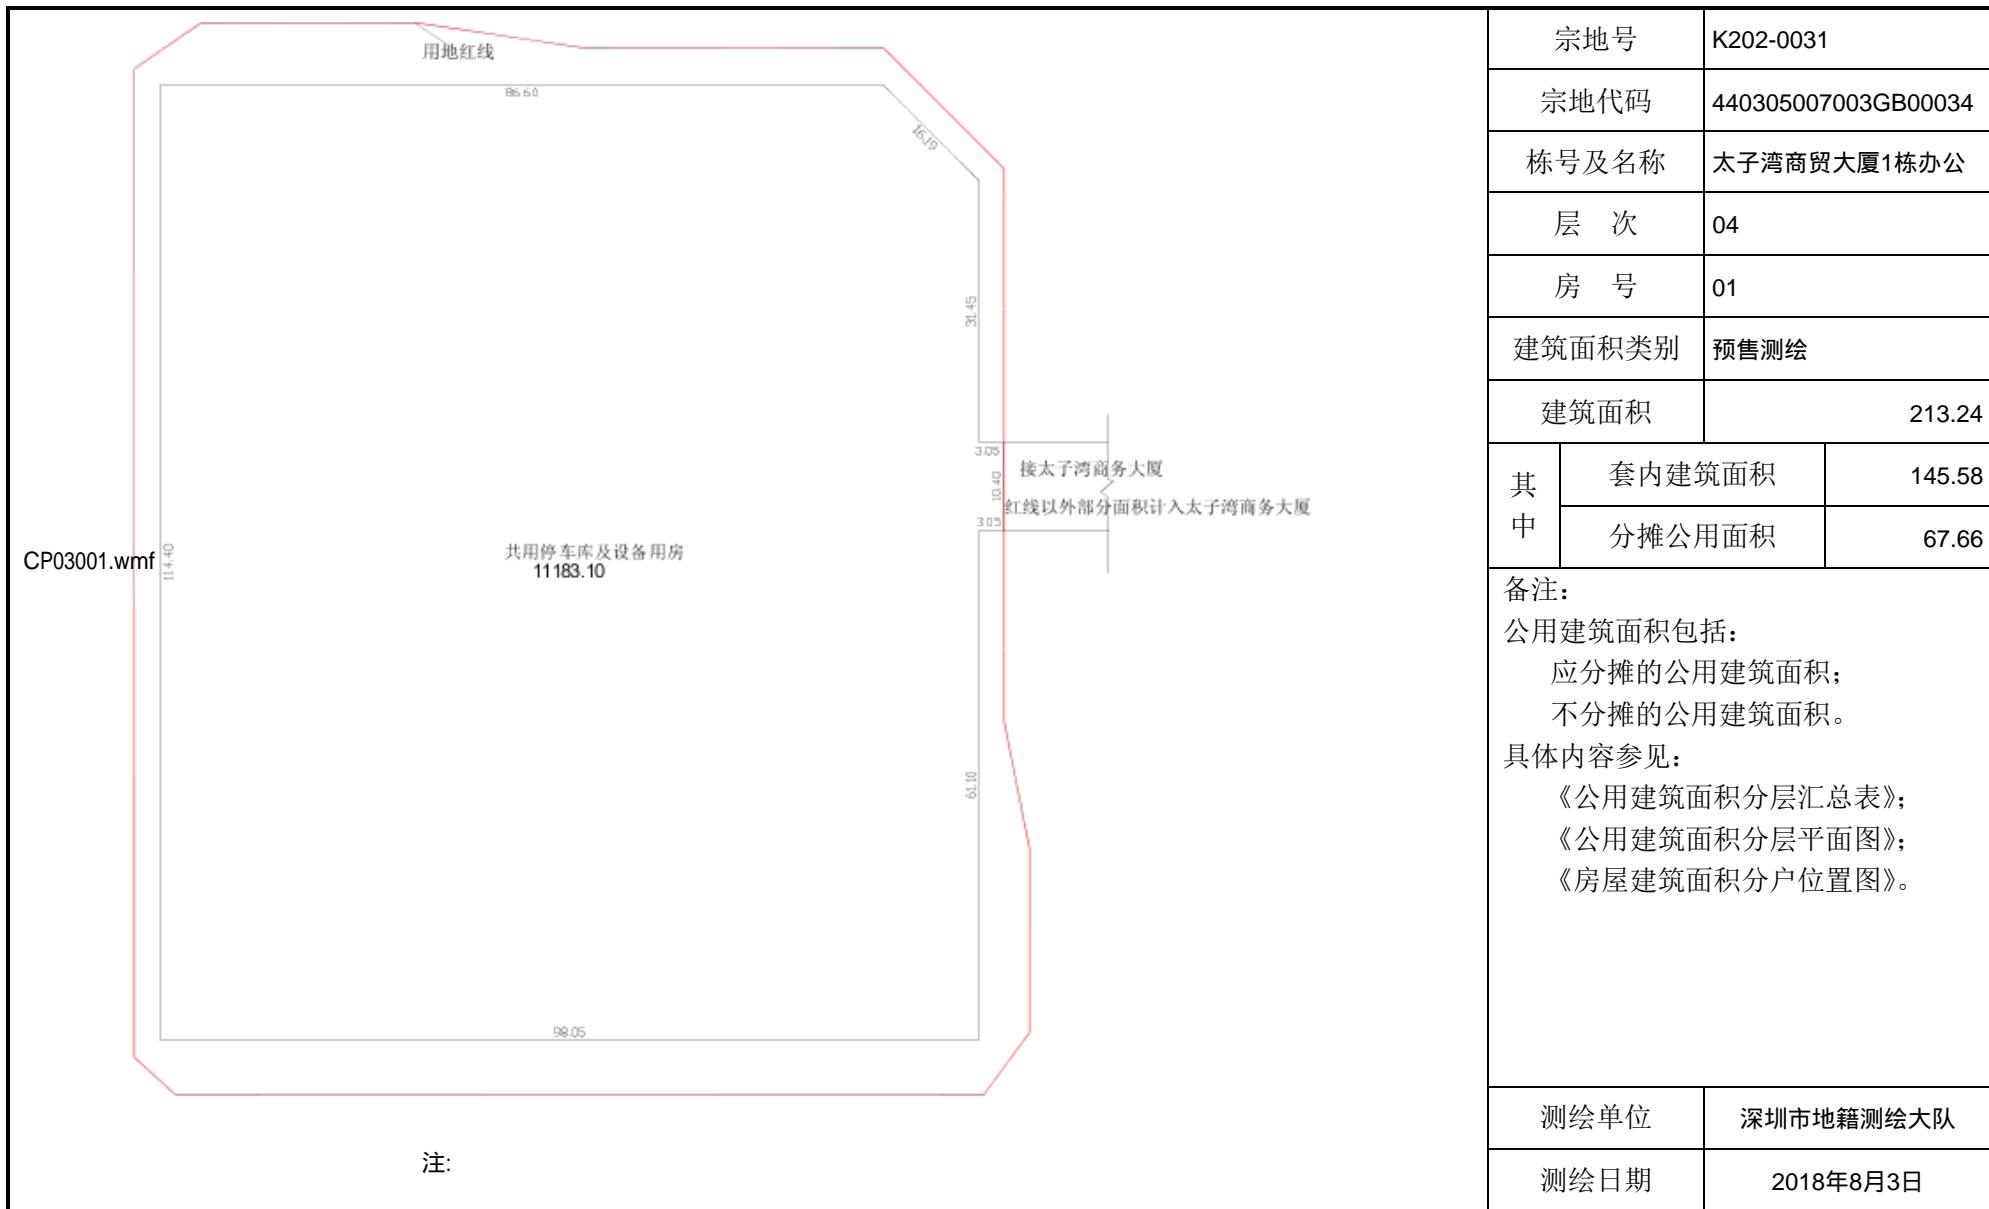


# 房屋建筑面积分户平面图

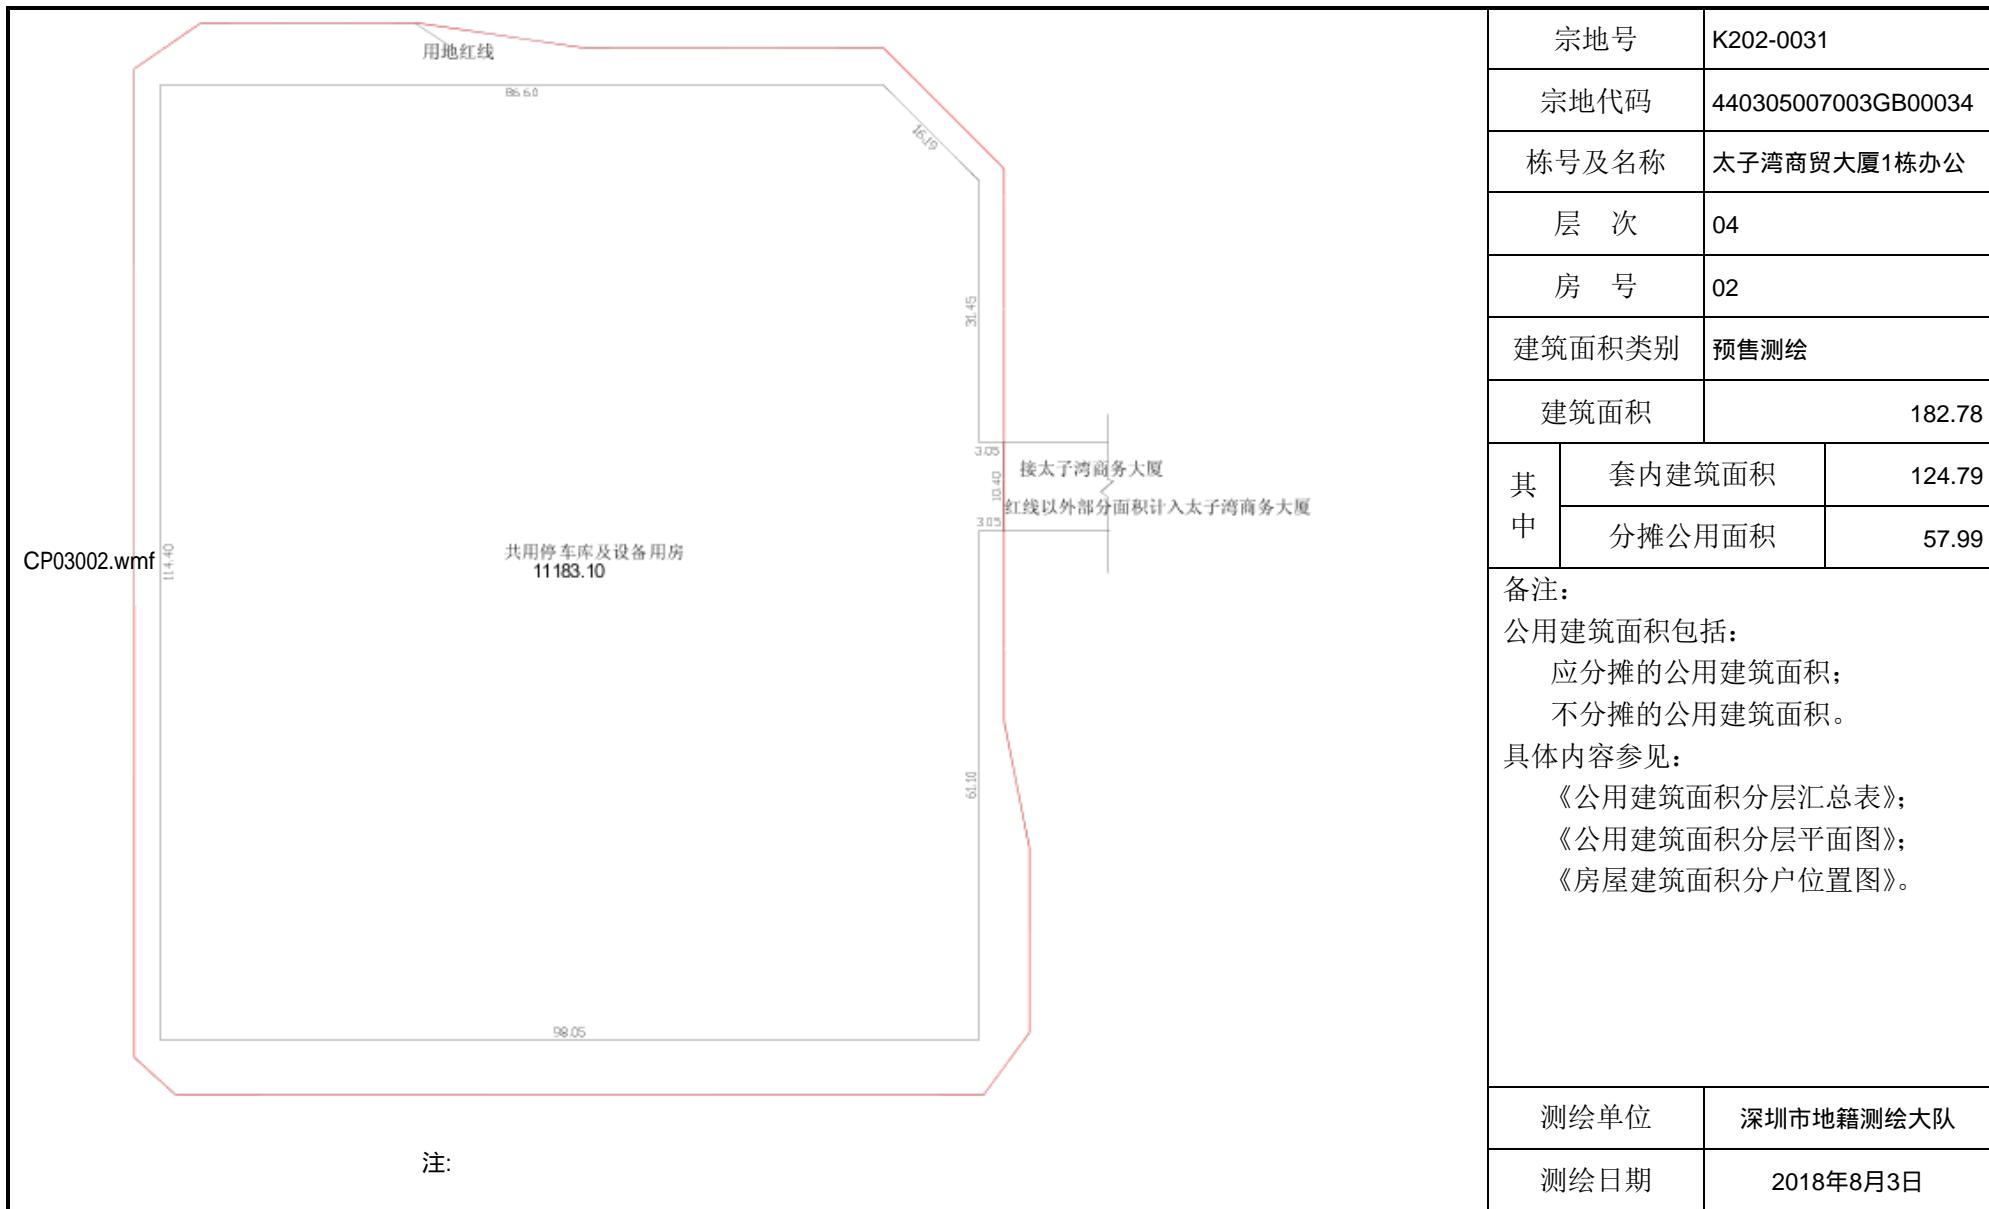


宗地号	K202-0031	
宗地代码	440305007003GB00034	
栋号及名称	太子湾商贸大厦1栋办公	
层 次	04	
房 号	02	
建筑面积类别	预售测绘	
建筑面 积	182.78	
其 中	套内建筑面积	124.79
	分摊公用面积	57.99
备注:		
公用建筑面积包括:		
应分摊的公用建筑面积;		
不分摊的公用建筑面积。		
具体内容参见:		
《公用建筑面积分层汇总表》;		
《公用建筑面积分层平面图》;		
《房屋建筑面积分户位置图》。		
测绘单位	深圳市地籍测绘大队	
测绘日期	2018年8月3日	


# 房屋建筑面积分户平面图

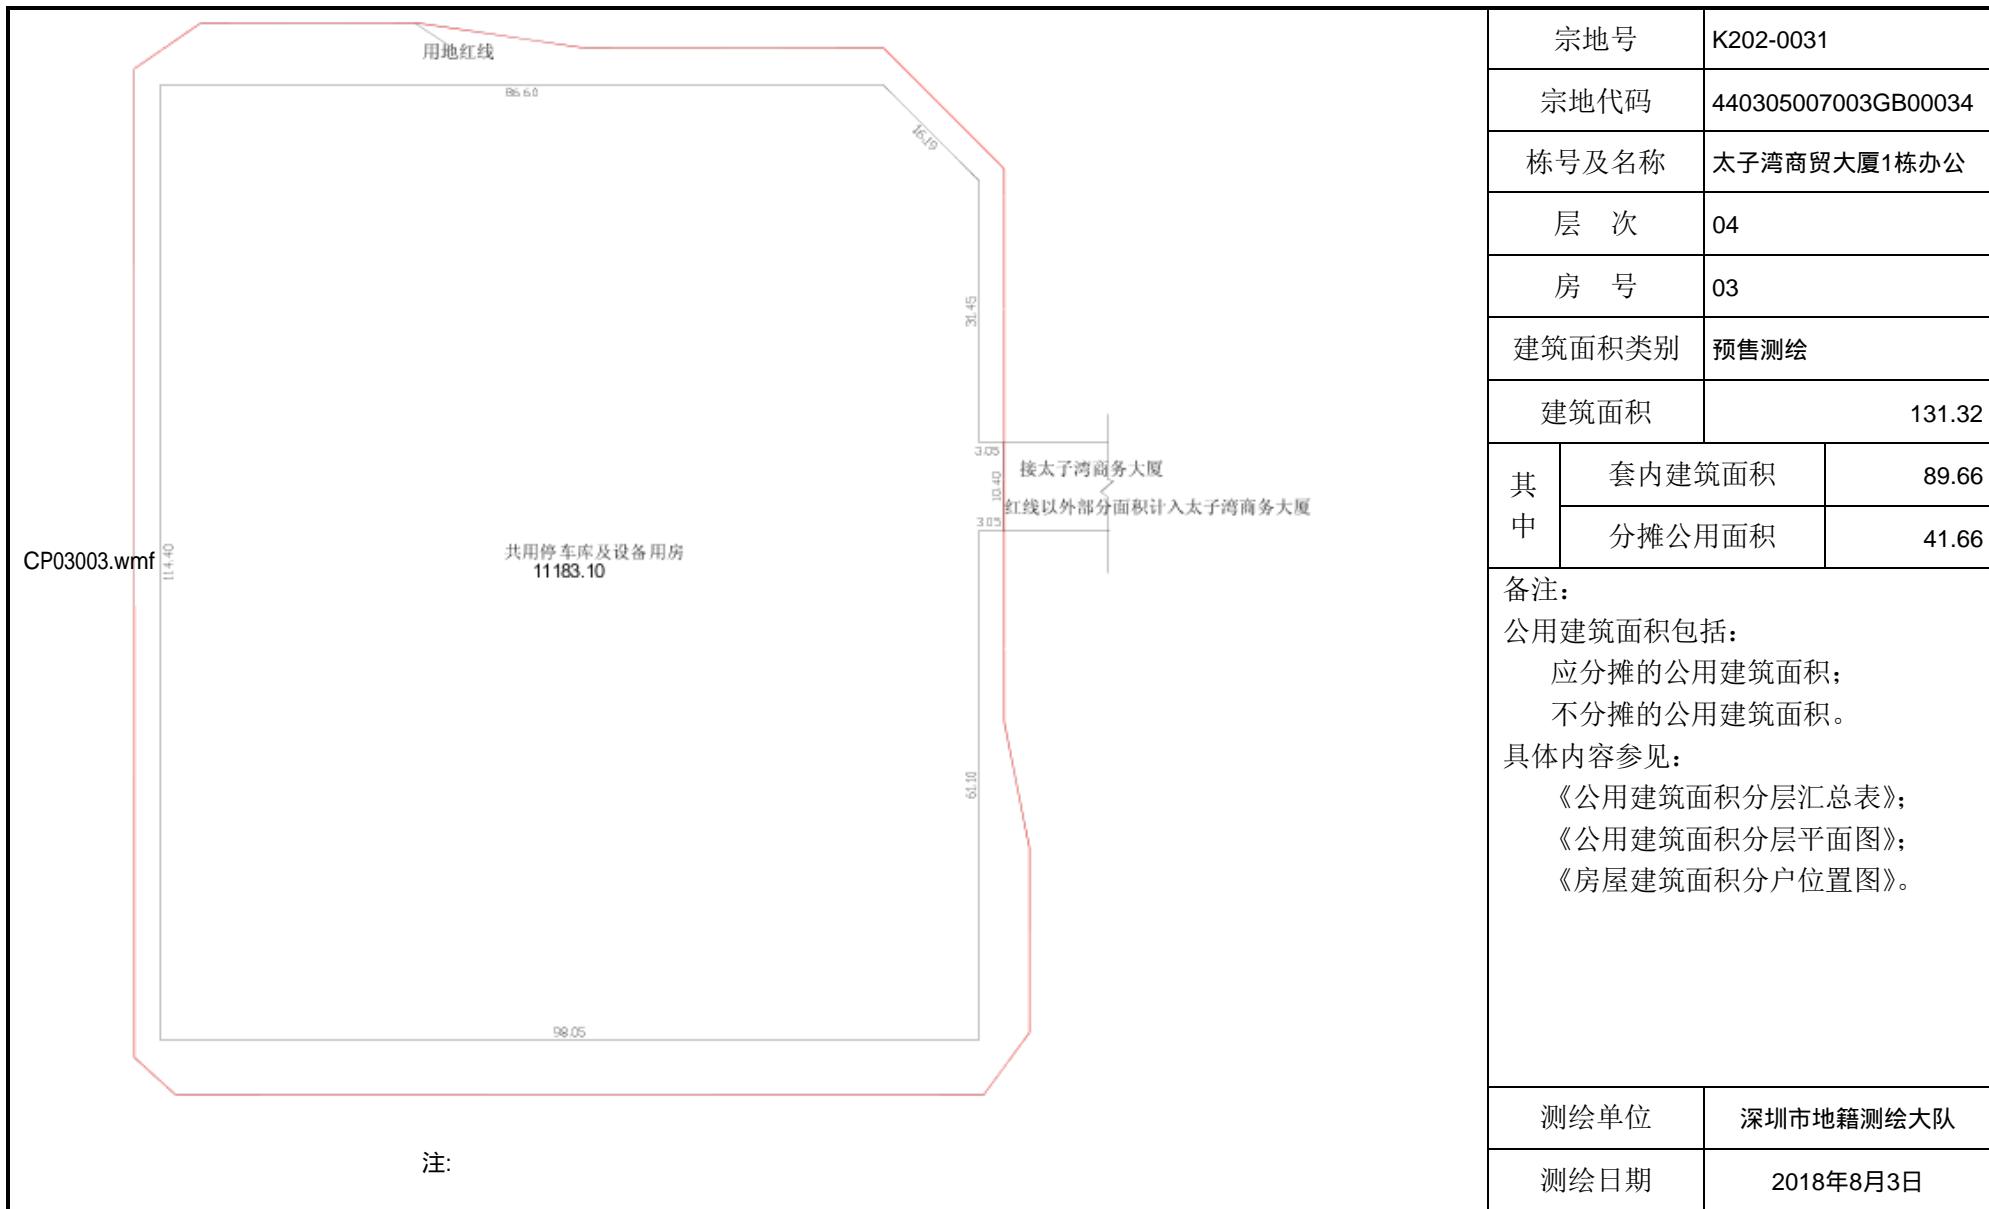


# 房屋建筑面积分户平面图

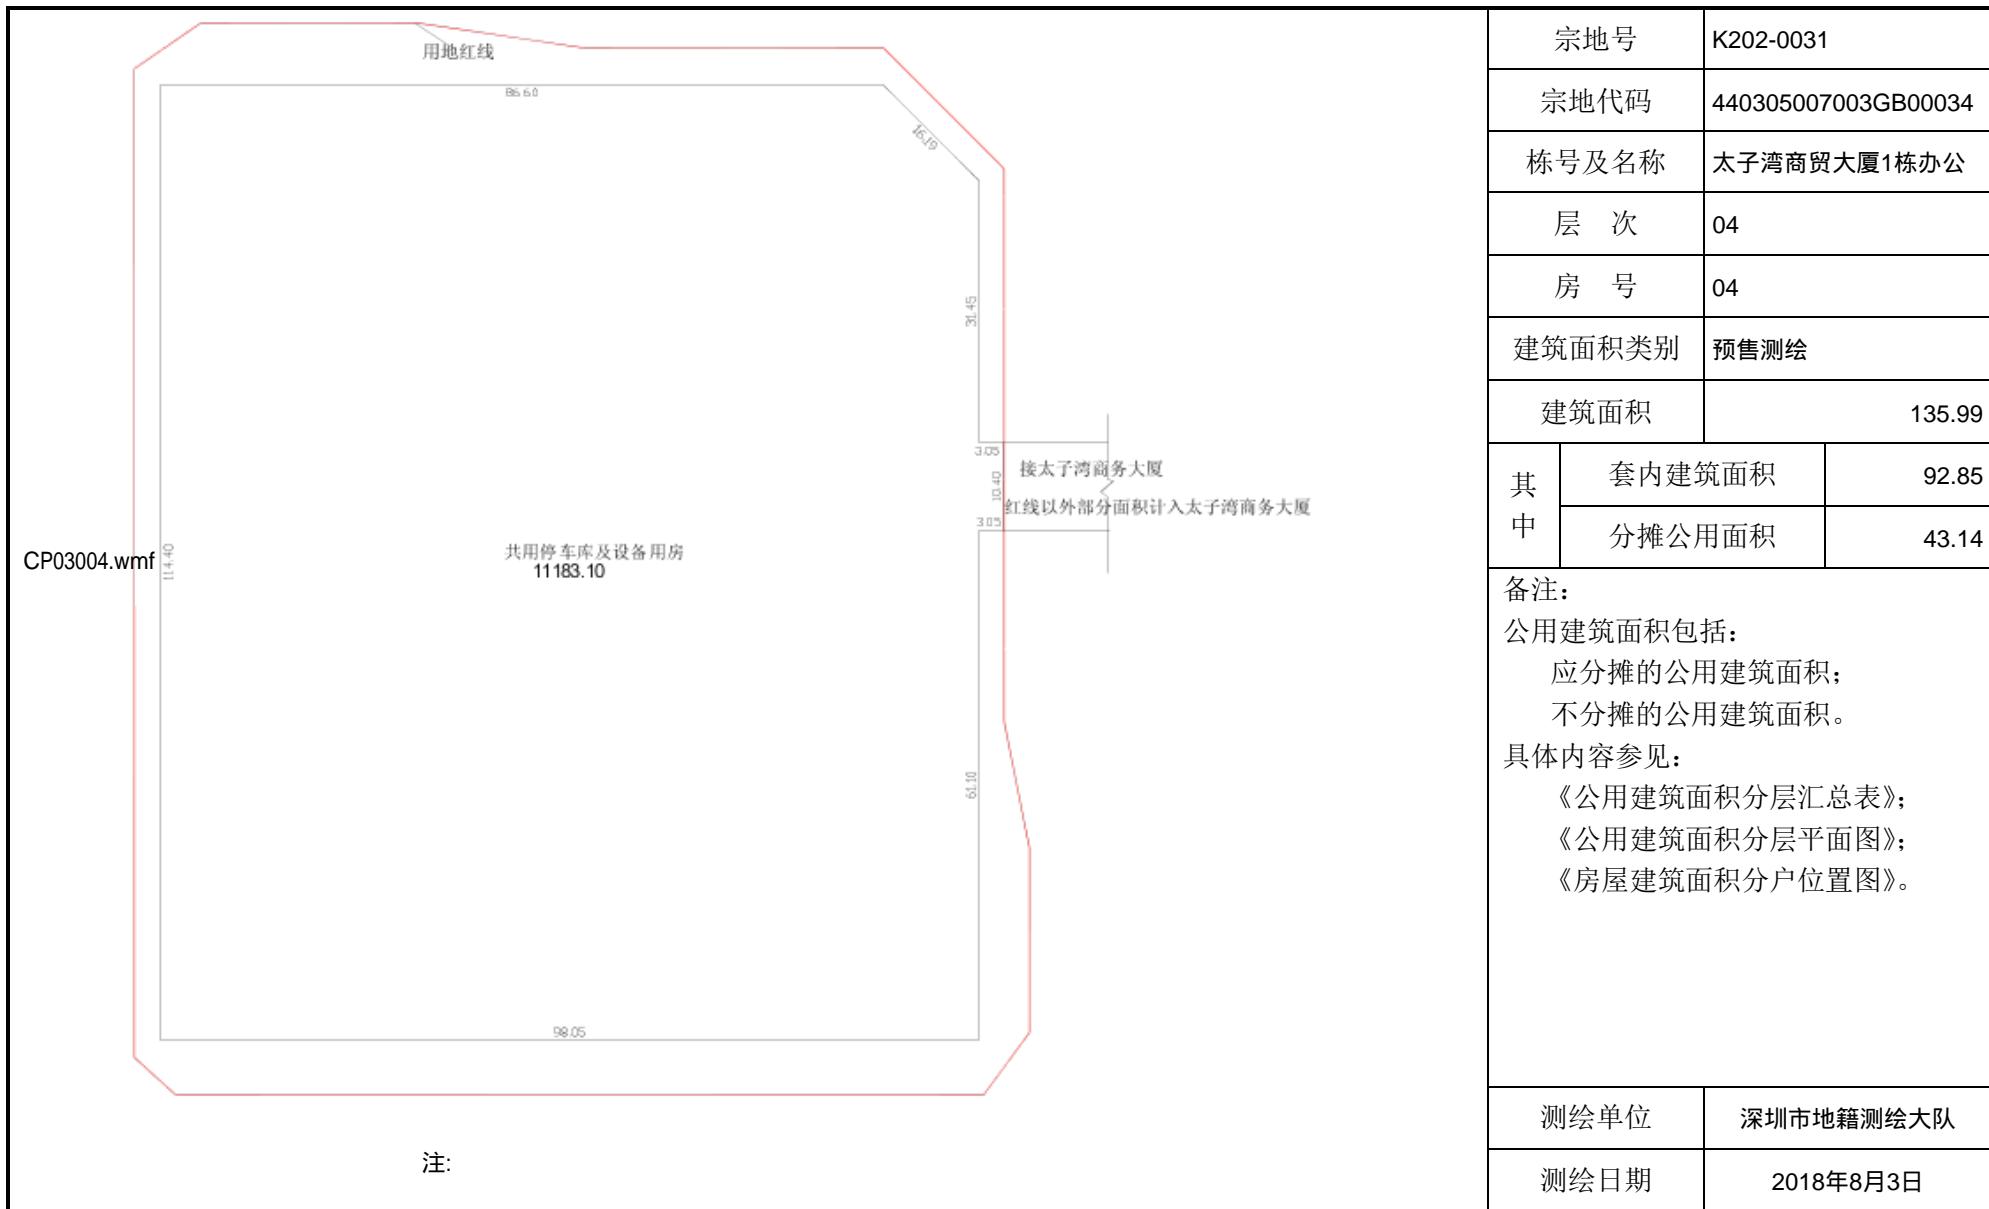


# 房屋建筑面积分户平面图

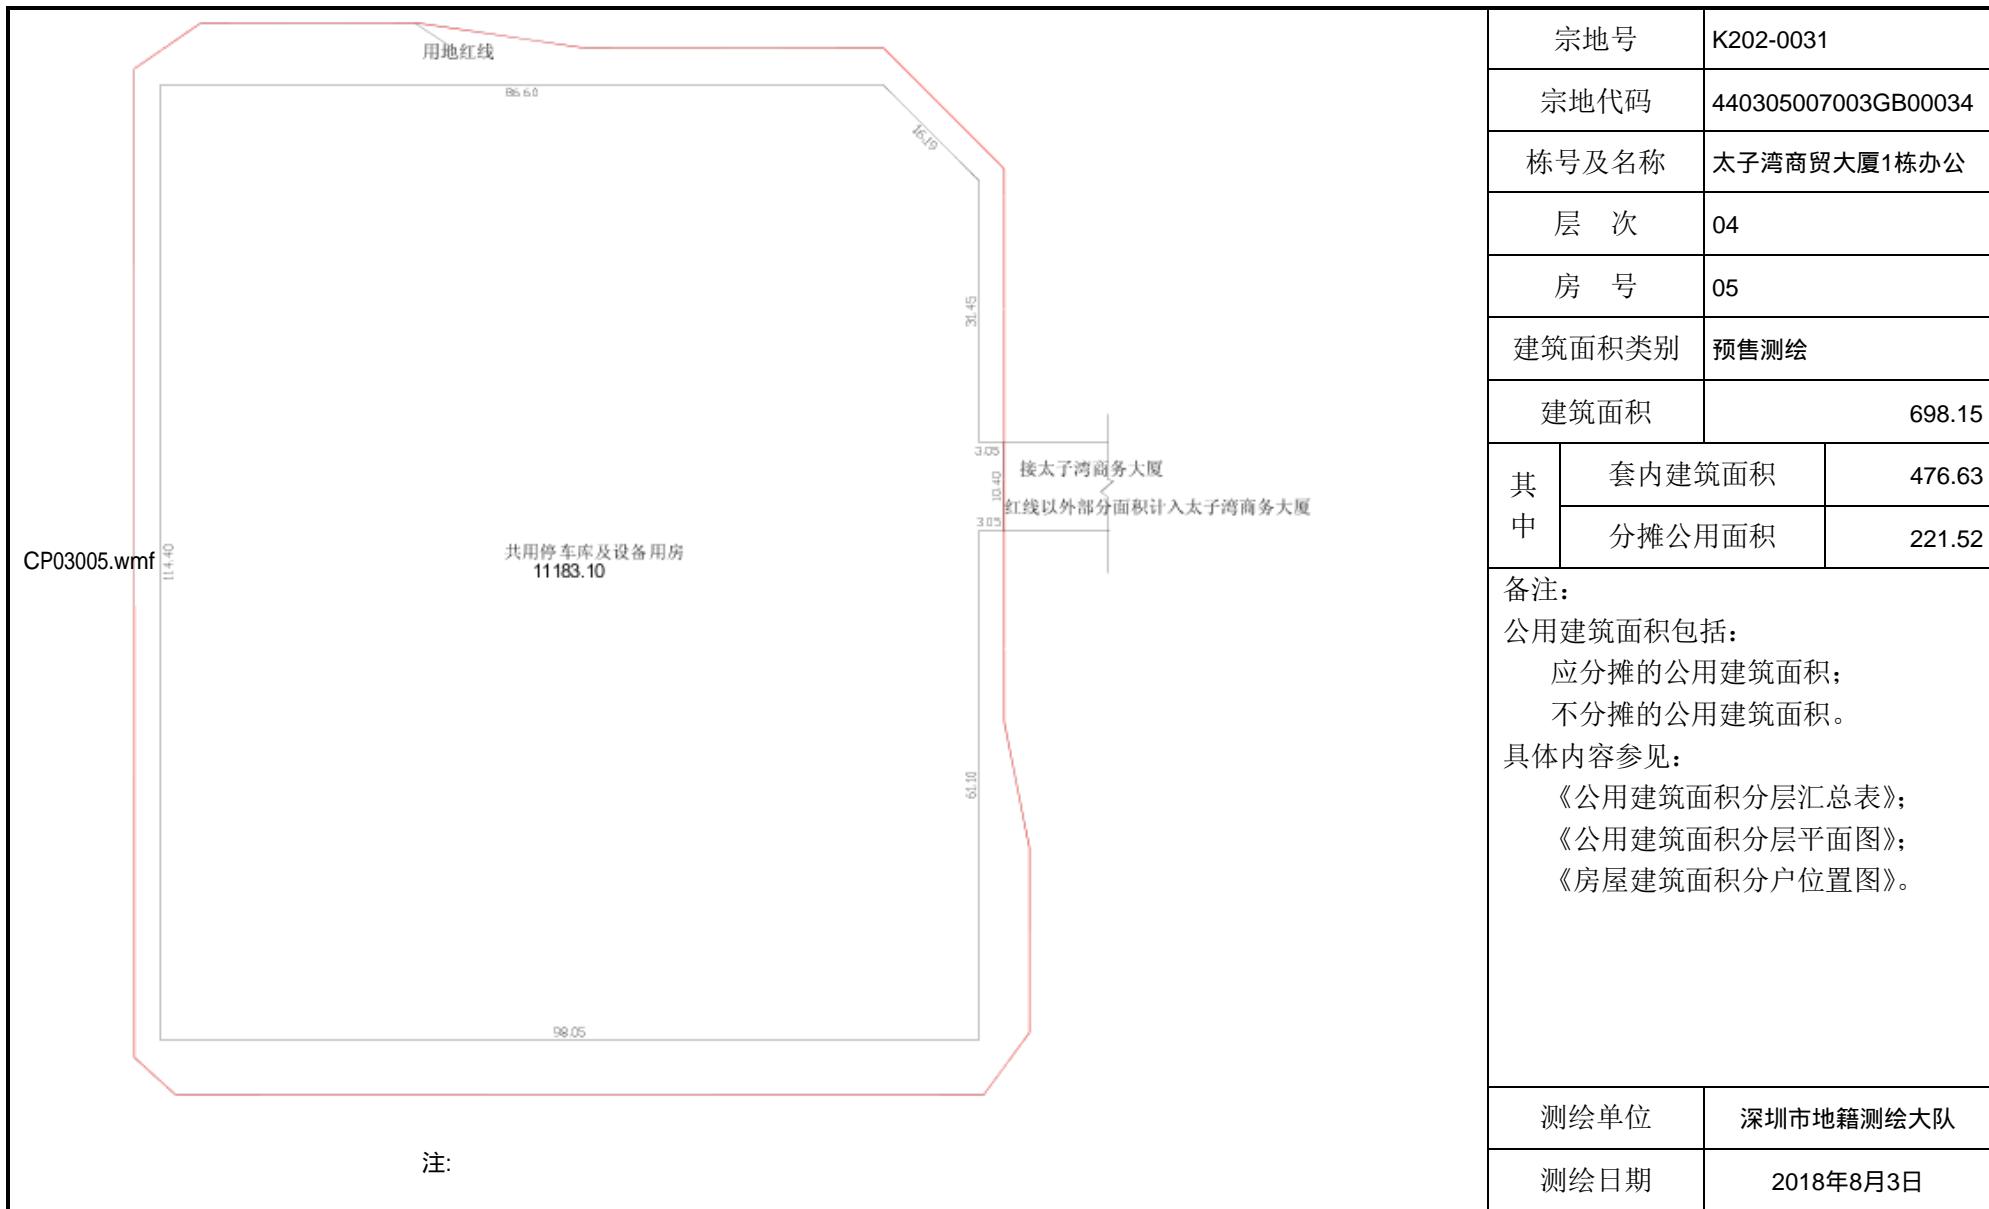


# 房屋建筑面积分户平面图

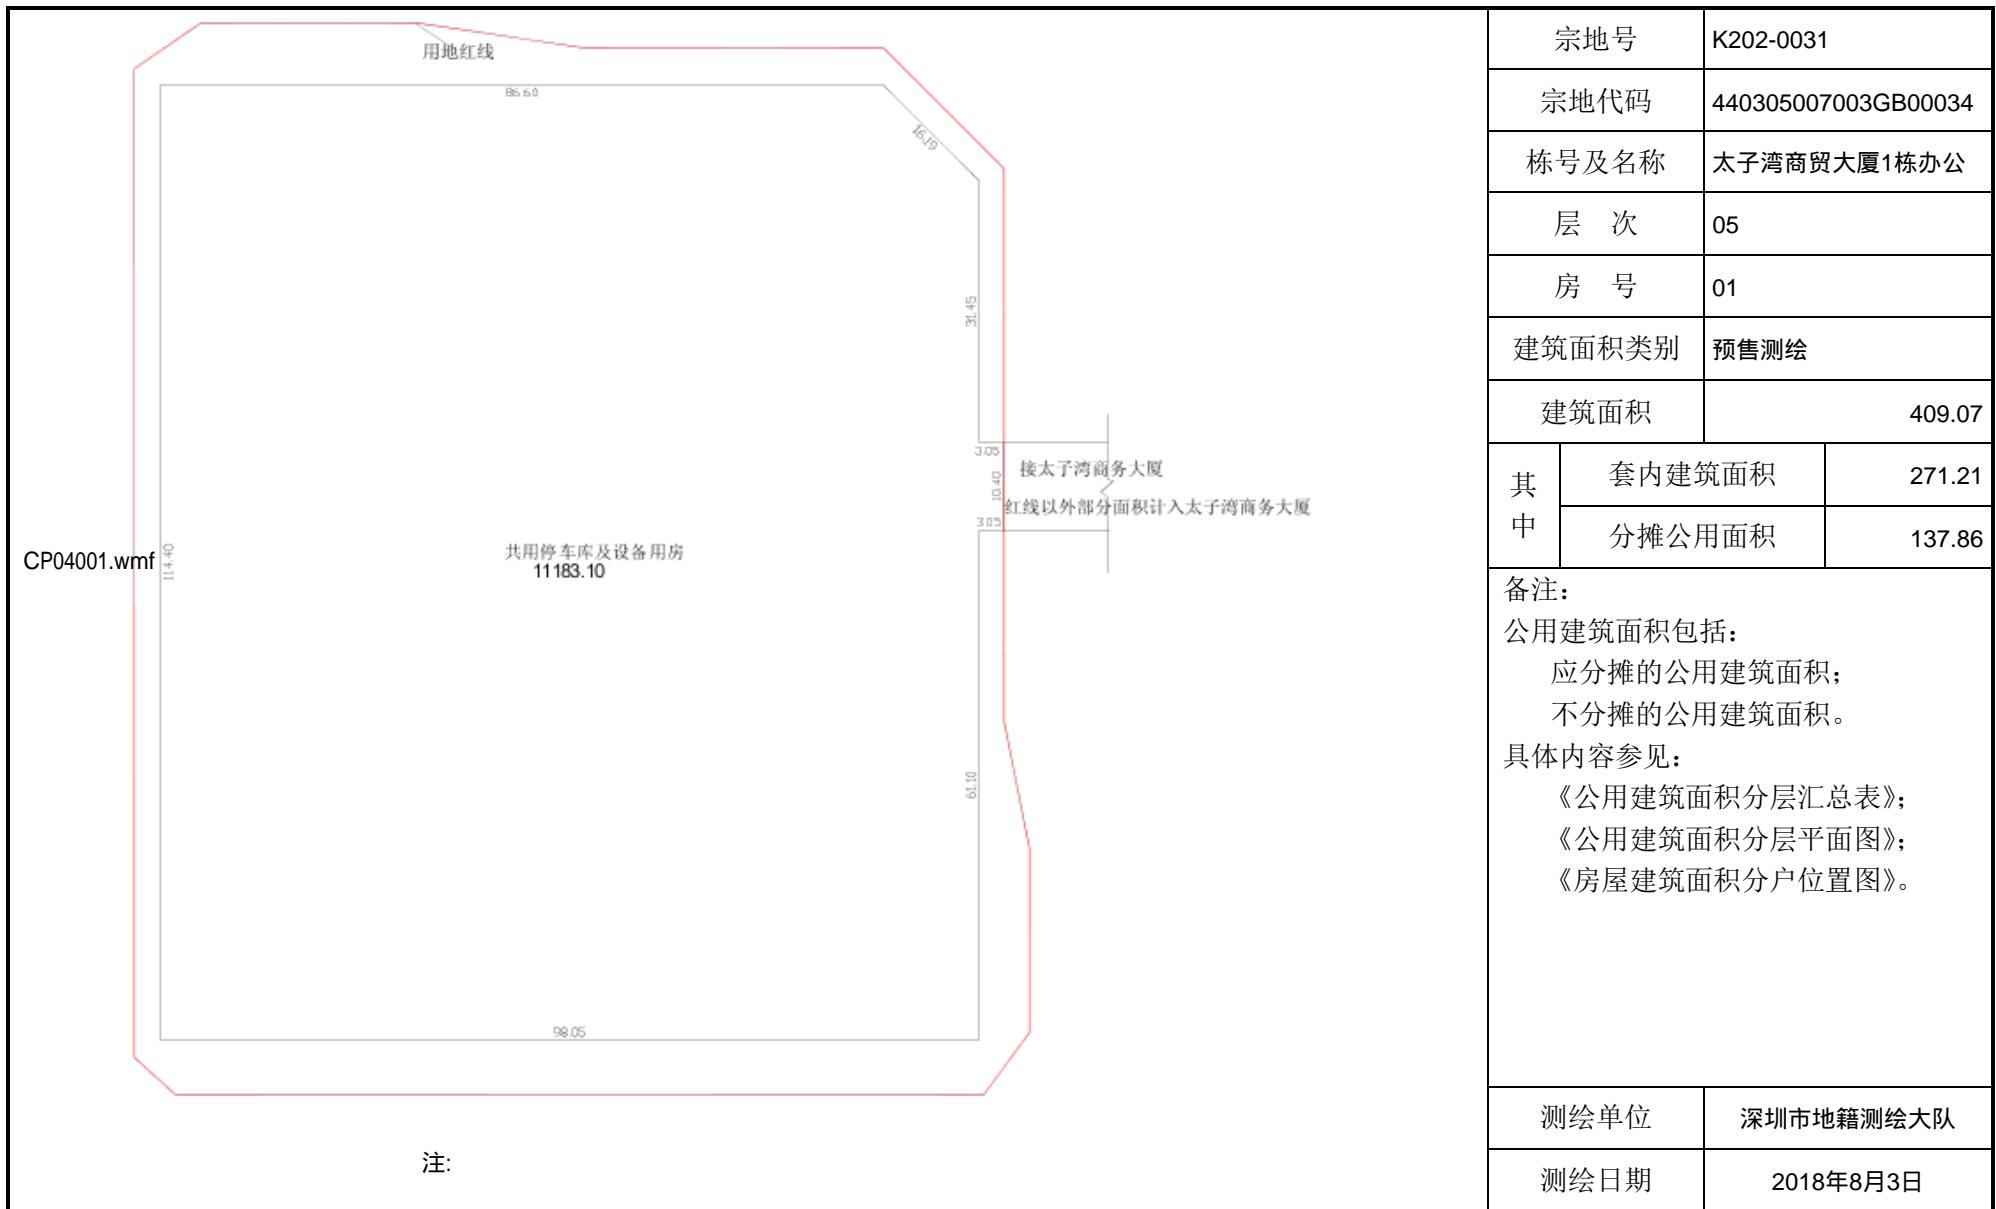


# 房屋建筑面积分户平面图

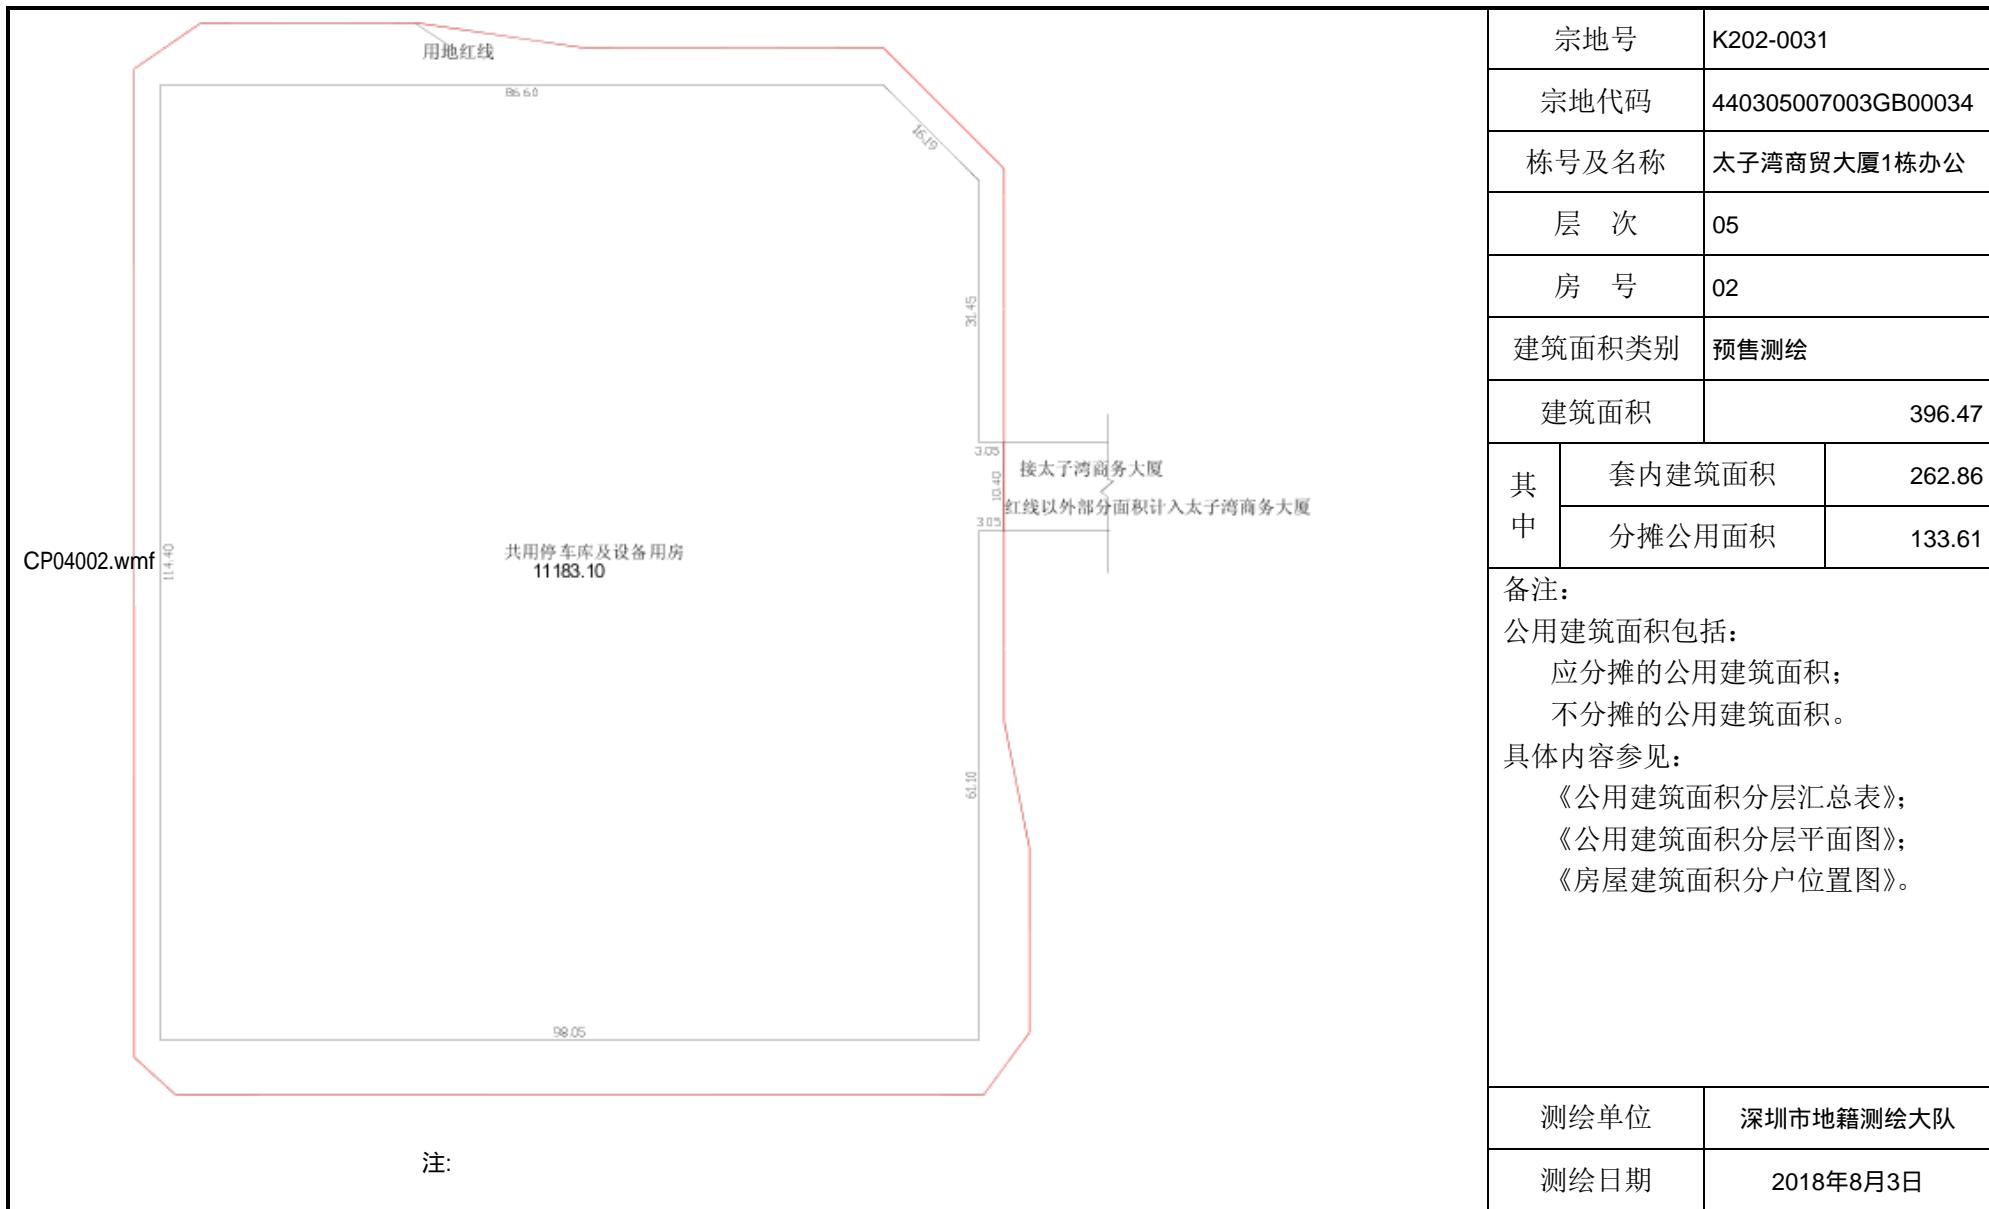

# 房屋建筑面积分户平面图

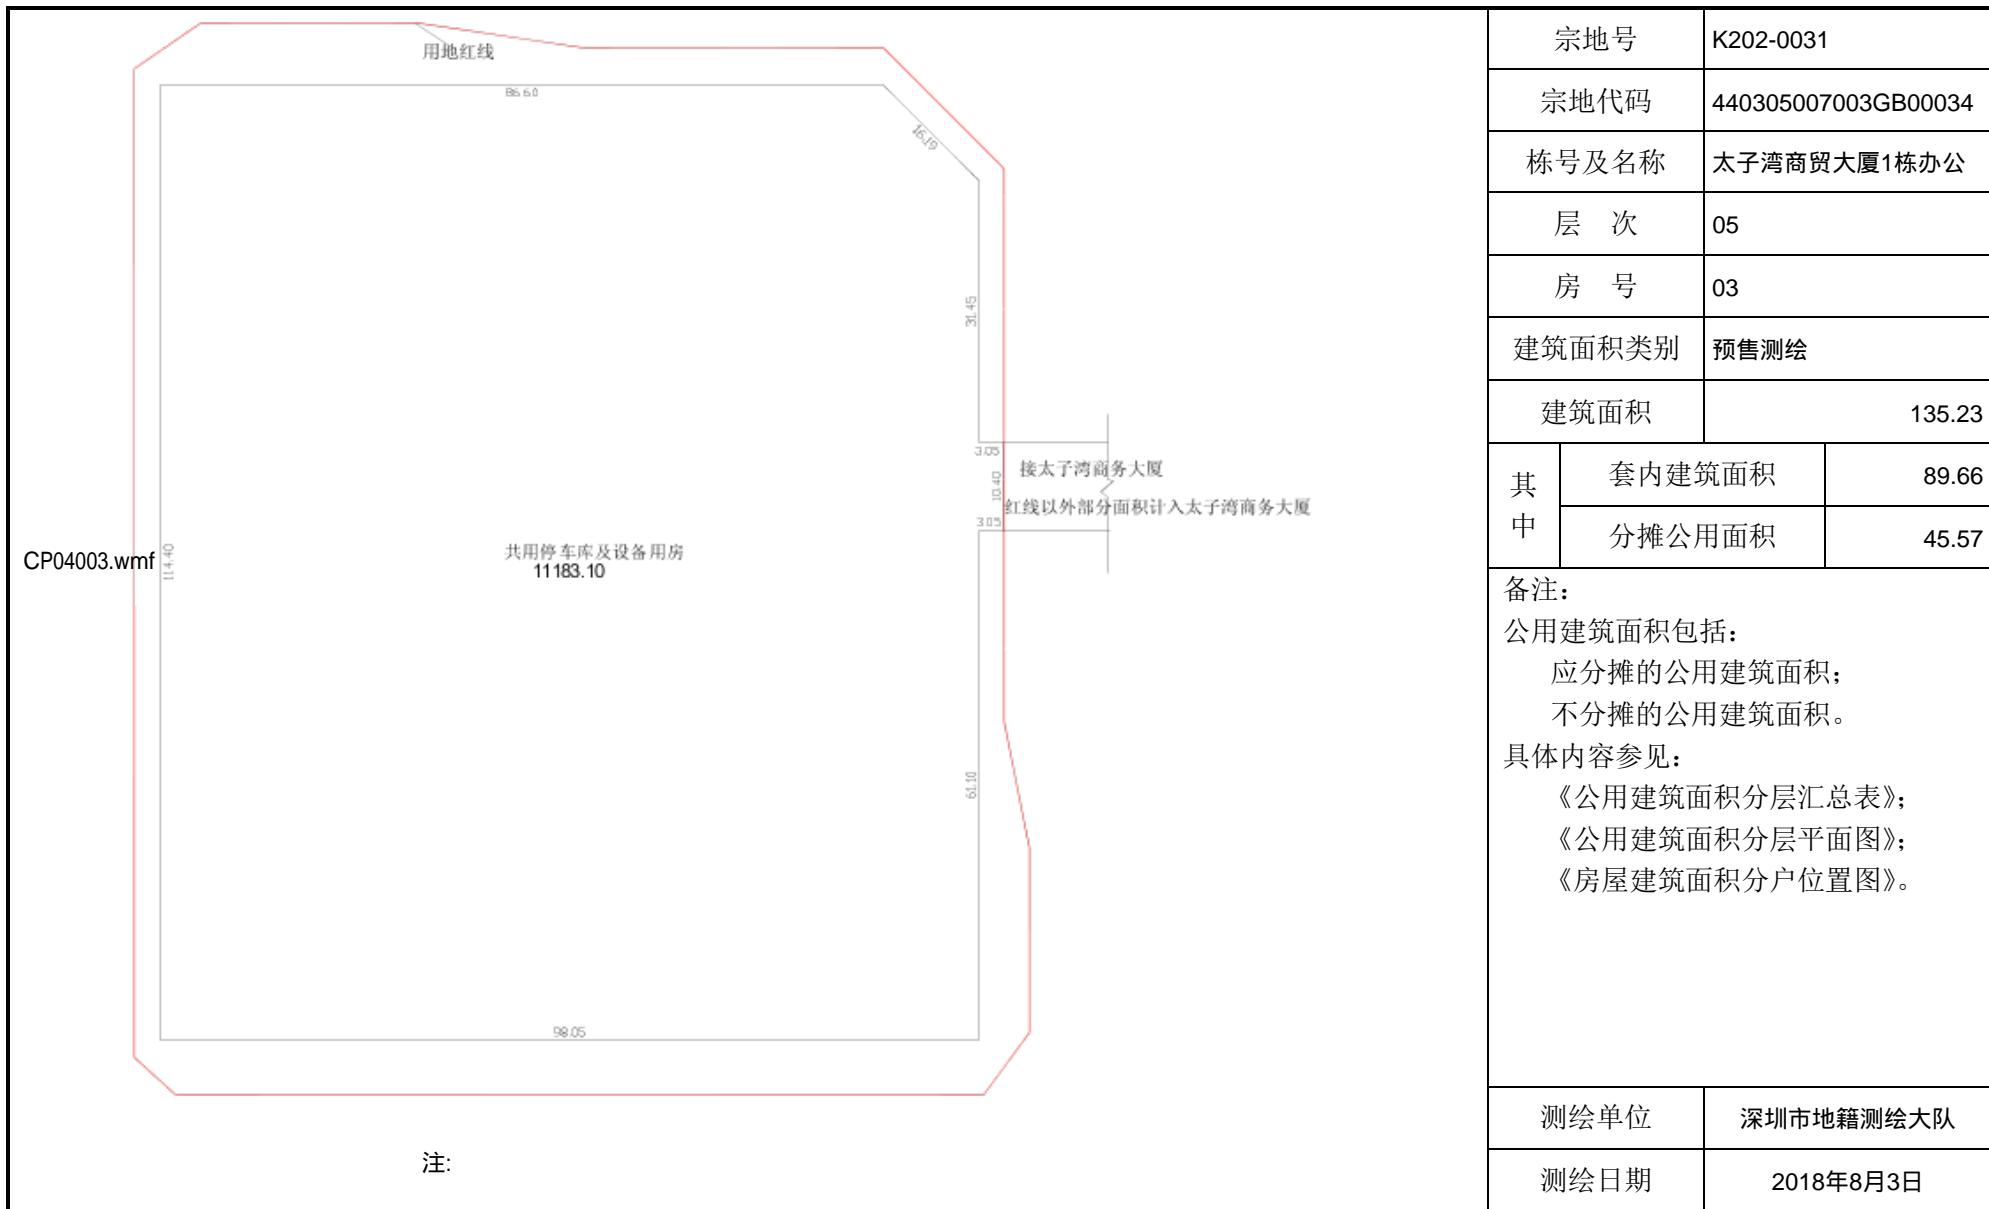


# 房屋建筑面积分户平面图

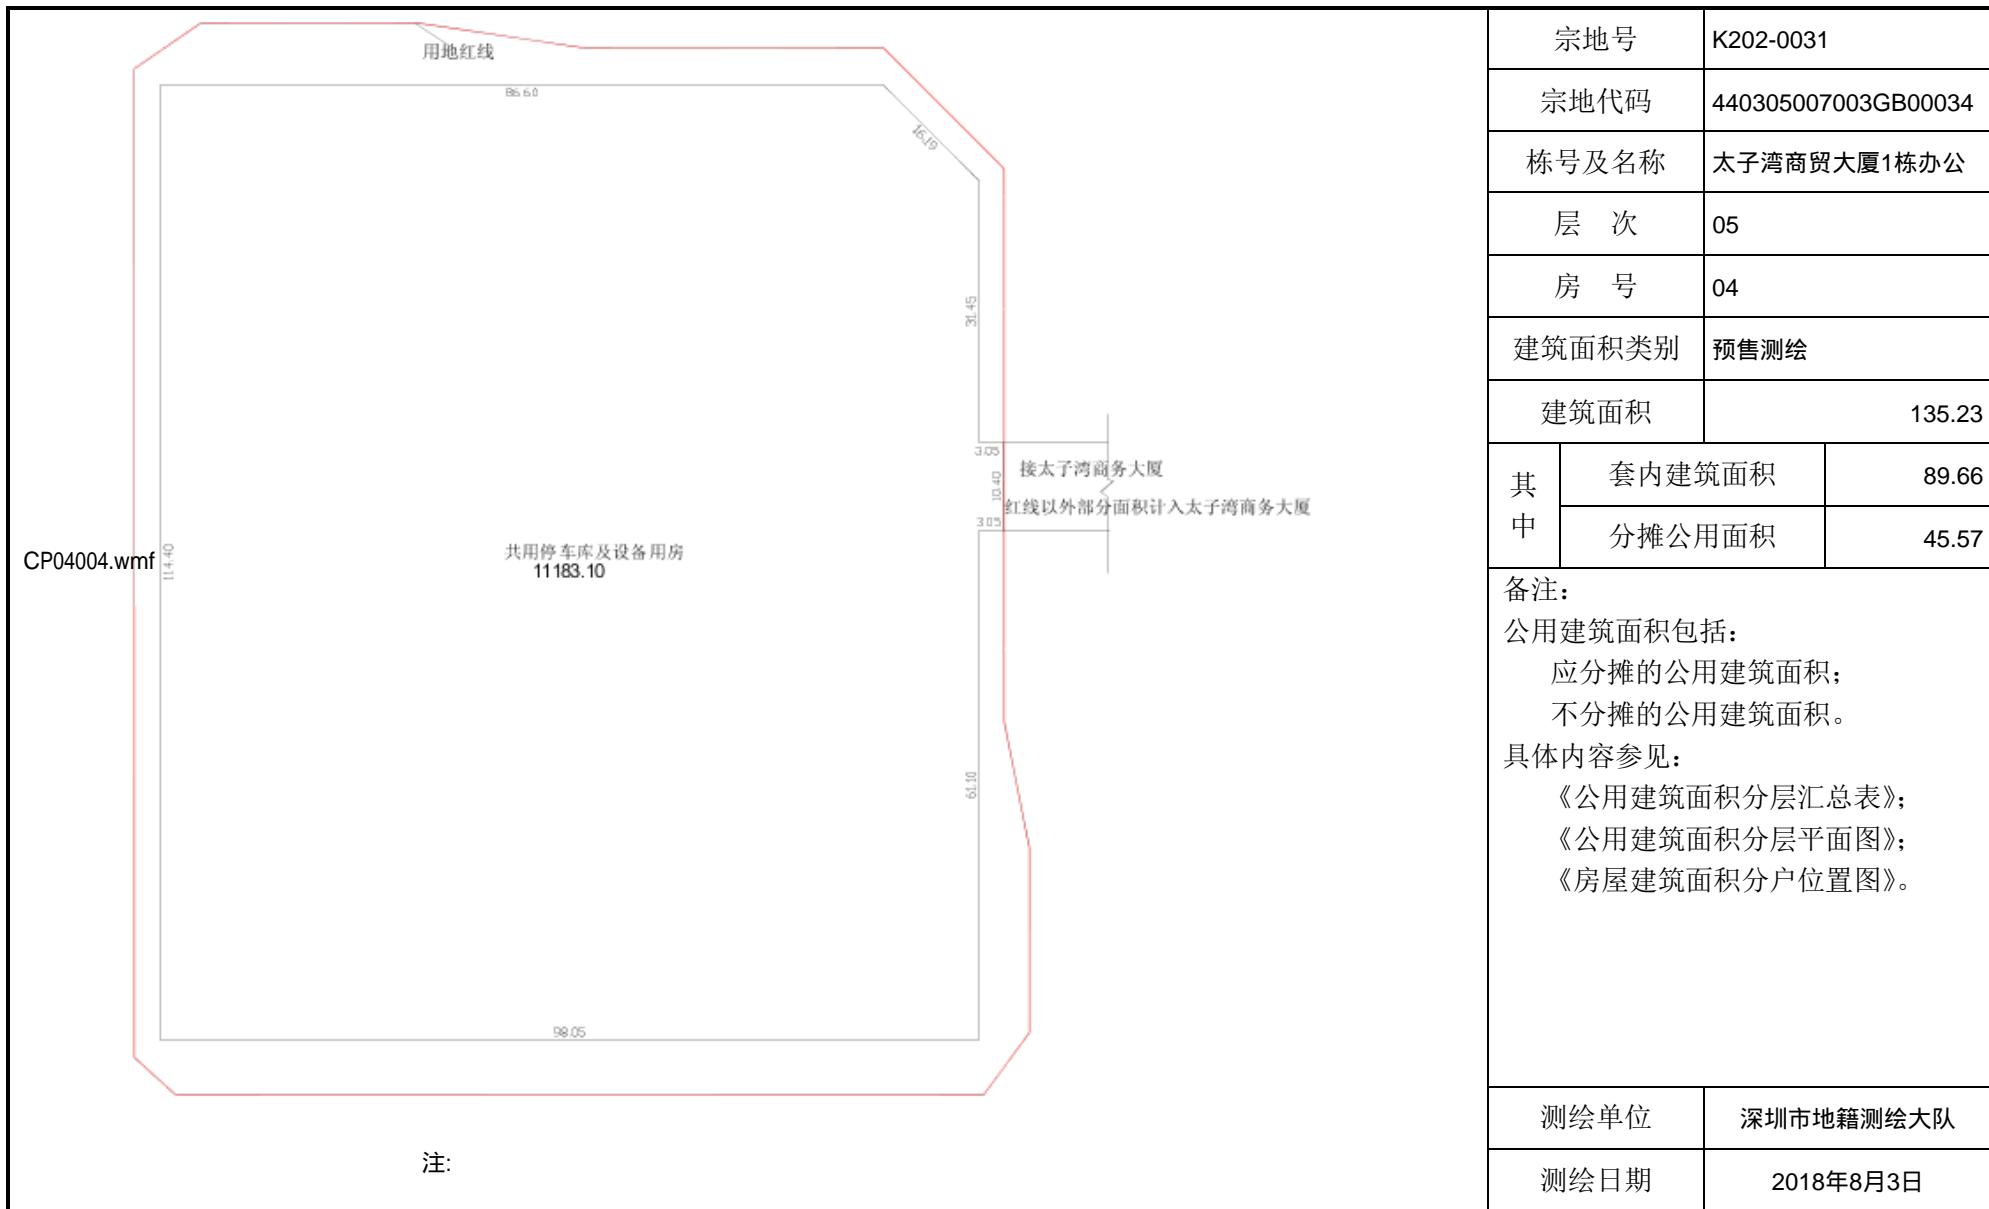


宗地号	K202-0031	
宗地代码	440305007003GB00034	
栋号及名称	太子湾商贸大厦1栋办公	
层 次	05	
房 号	04	
建筑面积类别	预售测绘	
建筑面 积	135.23	
其 中	套内建筑面积	89.66
	分摊公用面积	45.57
备注:		
公用建筑面积包括:		
应分摊的公用建筑面积;		
不分摊的公用建筑面积。		
具体内容参见:		
《公用建筑面积分层汇总表》;		
《公用建筑面积分层平面图》;		
《房屋建筑面积分户位置图》。		
测绘单位	深圳市地籍测绘大队	
测绘日期	2018年8月3日	

# 房屋建筑面积分户平面图

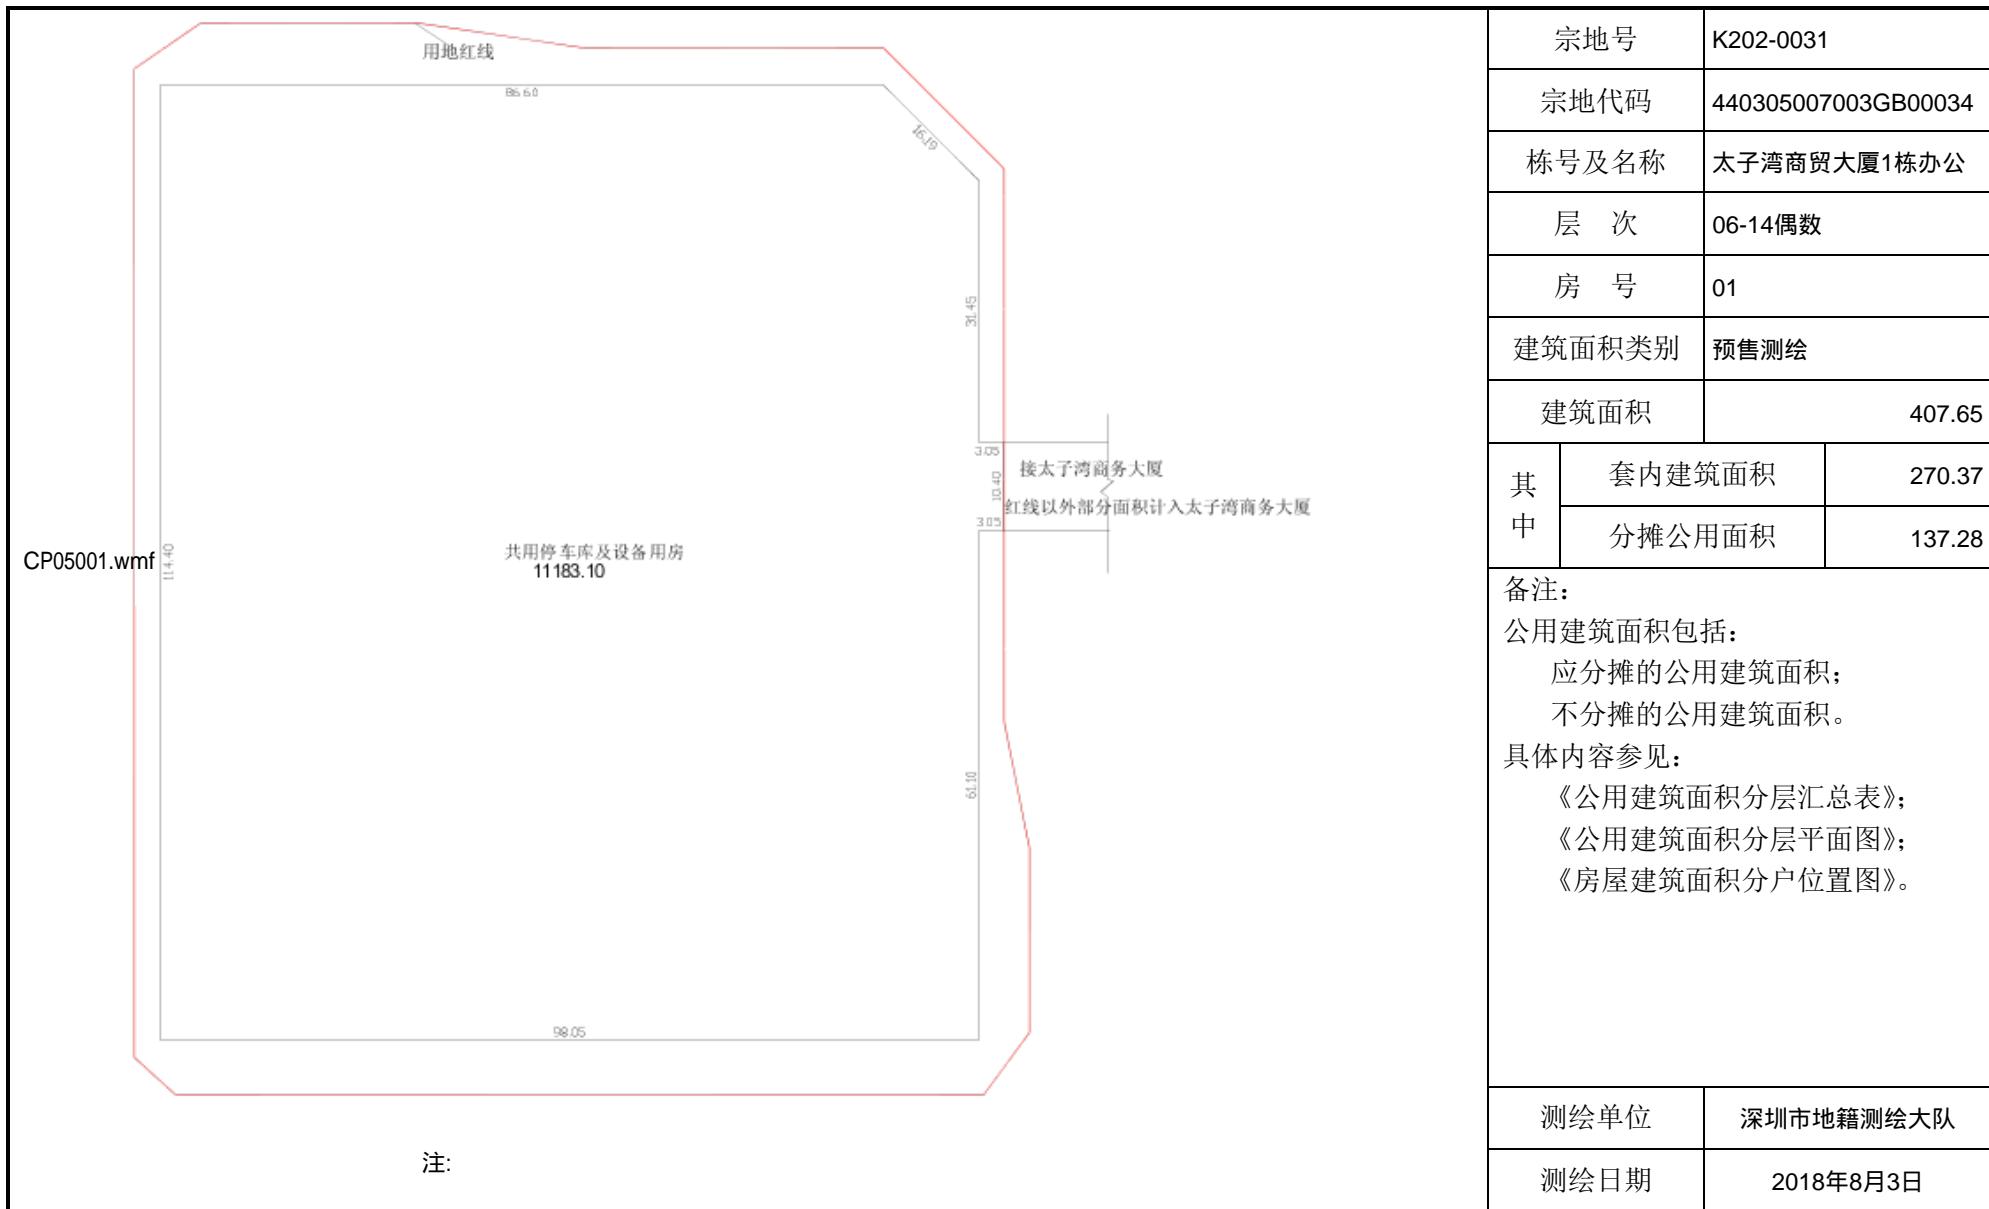


# 房屋建筑面积分户平面图

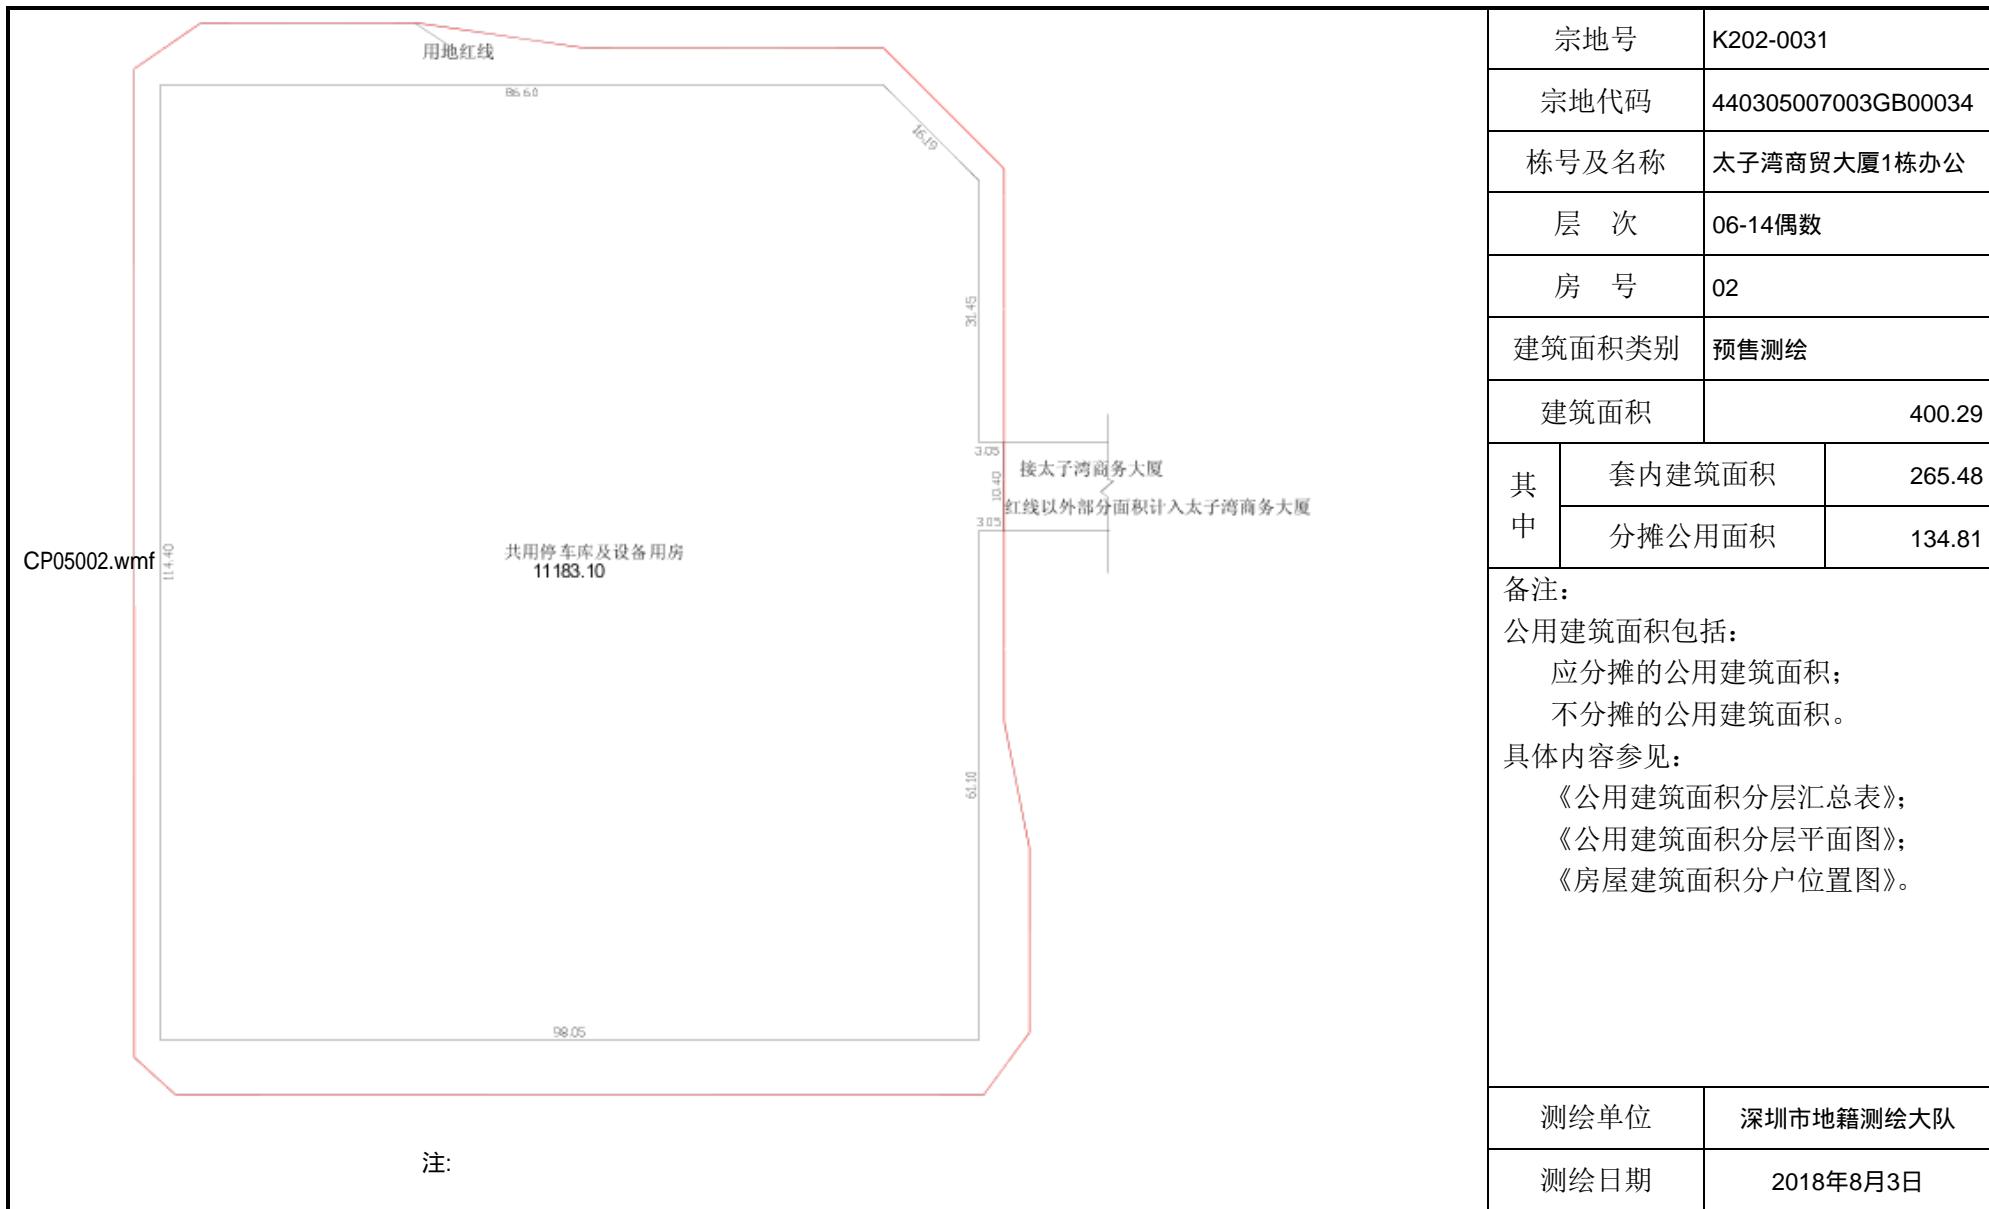


宗地号	K202-0031	
宗地代码	440305007003GB00034	
栋号及名称	太子湾商贸大厦1栋办公	
层 次	06-14偶数	
房 号	02	
建筑面积类别	预售测绘	
建筑面 积	400.29	
其 中	套内建筑面积	265.48
	分摊公用面积	134.81
备注:		
公用建筑面积包括:		
应分摊的公用建筑面积;		
不分摊的公用建筑面积。		
具体内容参见:		
《公用建筑面积分层汇总表》;		
《公用建筑面积分层平面图》;		
《房屋建筑面积分户位置图》。		
测绘单位	深圳市地籍测绘大队	
测绘日期	2018年8月3日	

## 房屋建筑面积分户平面图

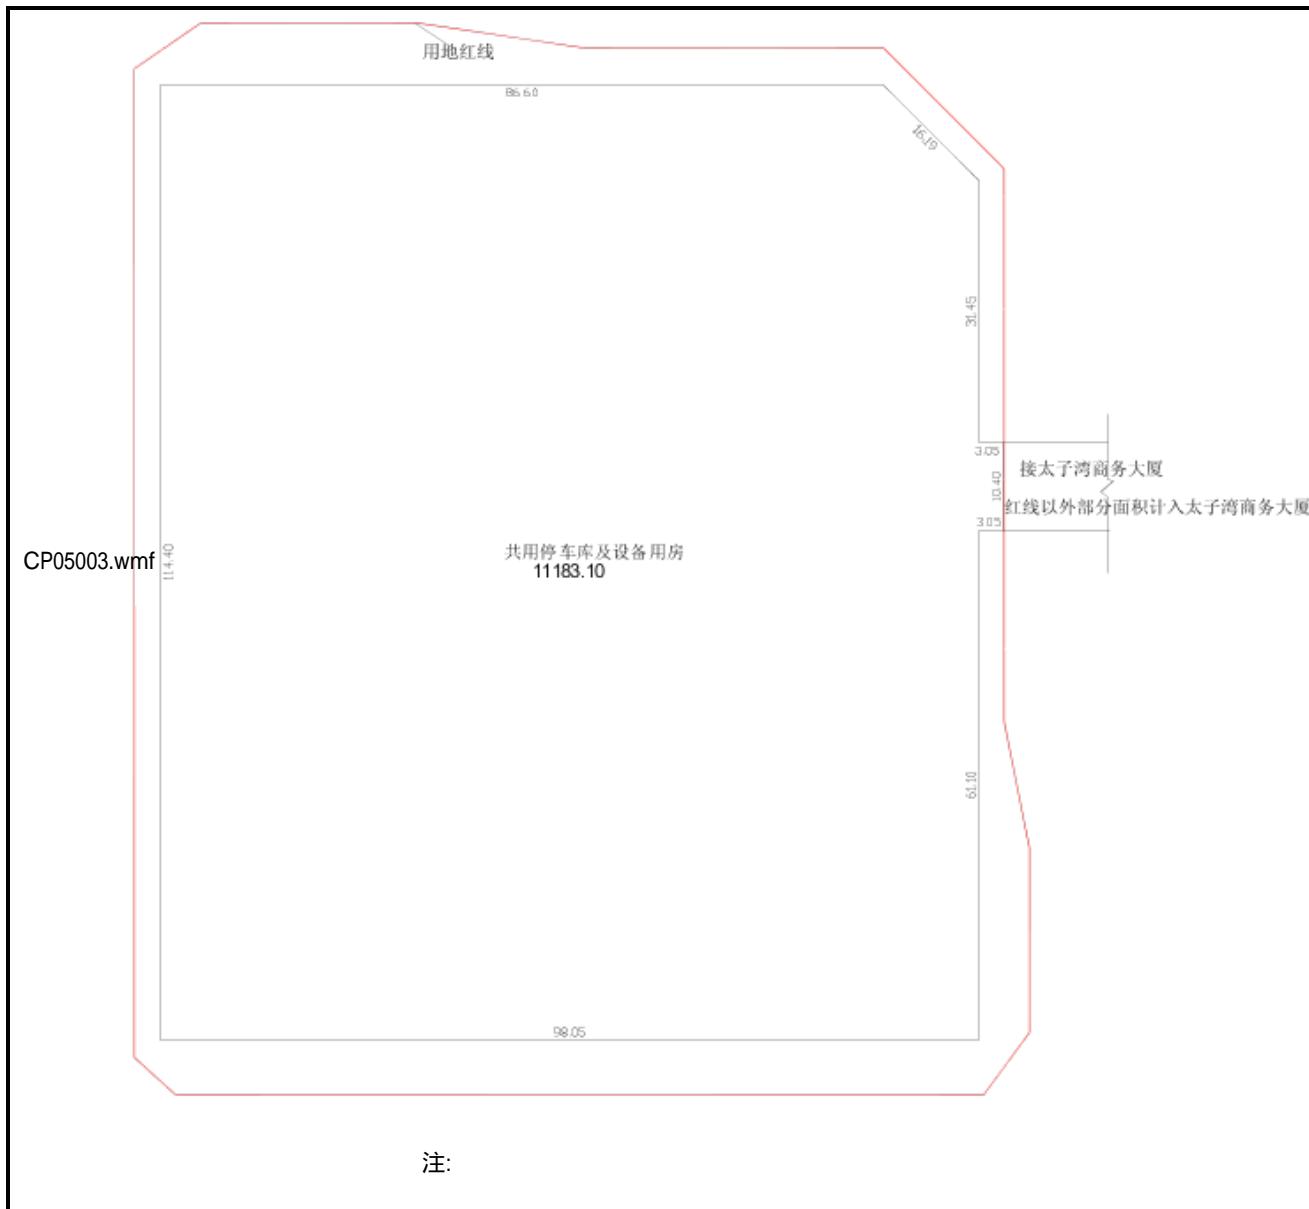


宗地号	K202-0031	
宗地代码	440305007003GB00034	
栋号及名称	太子湾商贸大厦1栋办公	
层 次	06-14偶数	
房 号	03	
建筑面积类别	预售测绘	
建筑面积	135.18	
其 中	套内建筑面积	89.66
	分摊公用面积	45.52
备注： 公用建筑面积包括： 应分摊的公用建筑面积； 不分摊的公用建筑面积。 具体内容参见： 《公用建筑面积分层汇总表》； 《公用建筑面积分层平面图》； 《房屋建筑面积分户位置图》。		

## 房屋建筑面积分户平面图

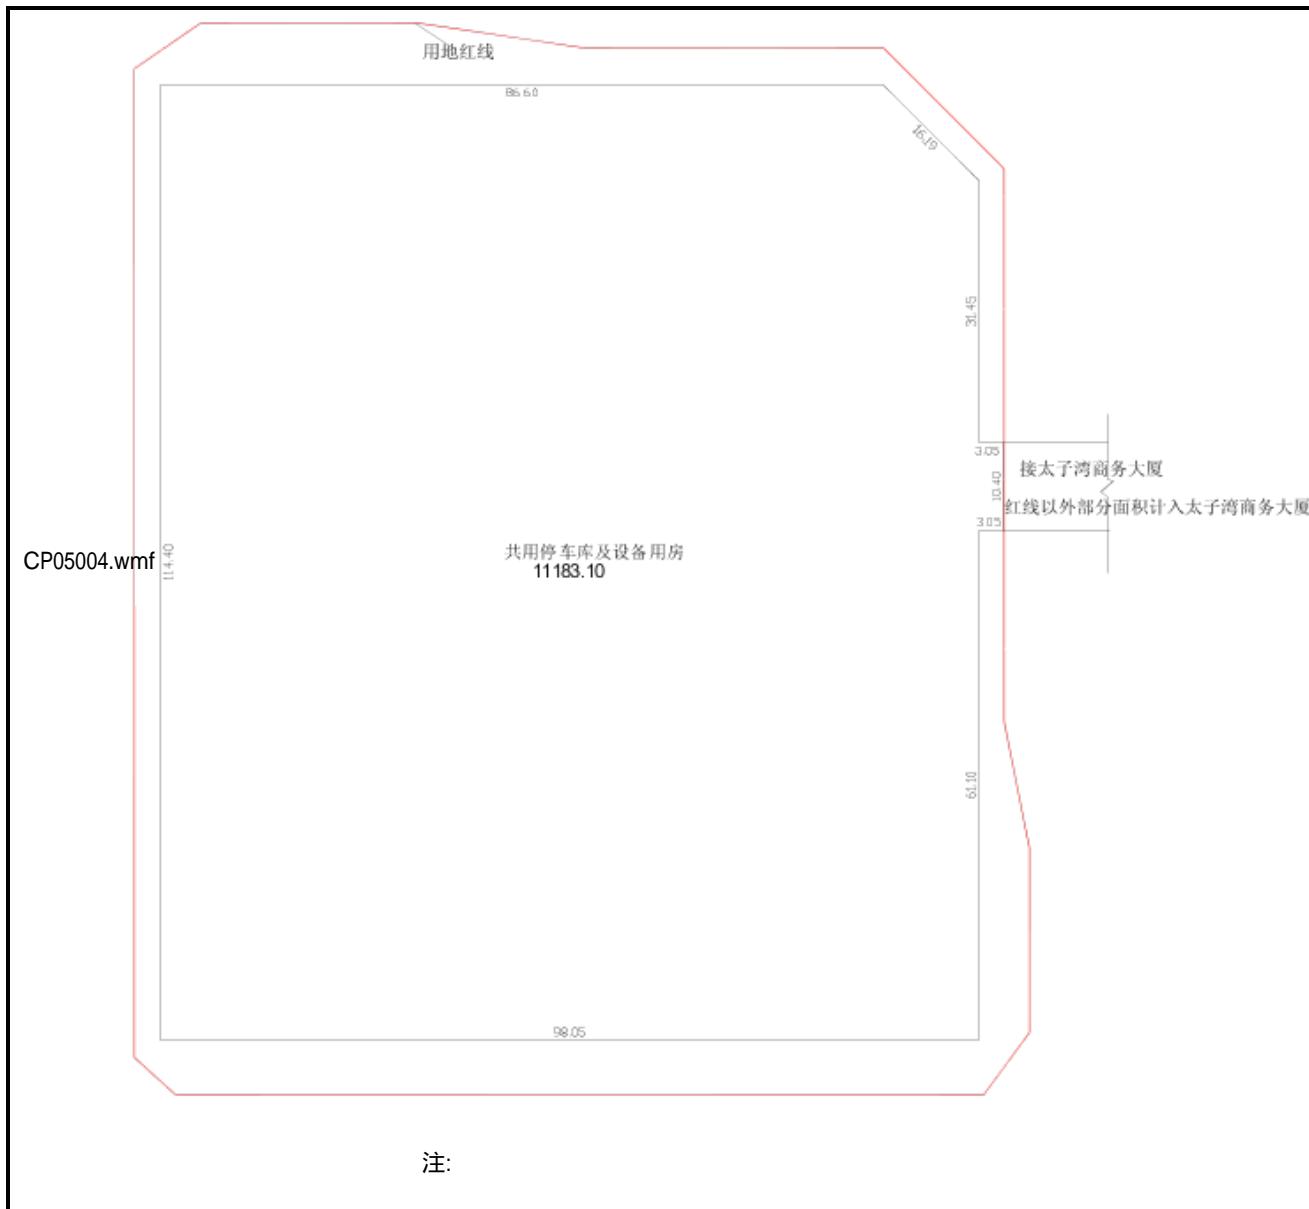


宗地号	K202-0031	
宗地代码	440305007003GB00034	
栋号及名称	太子湾商贸大厦1栋办公	
层 次	06-14偶数	
房 号	04	
建筑面积类别	预售测绘	
建筑面积	135.18	
其 中	套内建筑面积	89.66
	分摊公用面积	45.52
备注：		
公用建筑面积包括：		
应分摊的公用建筑面积；		
不分摊的公用建筑面积。		
具体内容参见：		
《公用建筑面积分层汇总表》；		
《公用建筑面积分层平面图》；		
《房屋建筑面积分户位置图》。		
测绘单位	深圳市地籍测绘大队	
测绘日期	2018年8月3日	

## 房屋建筑面积分户平面图

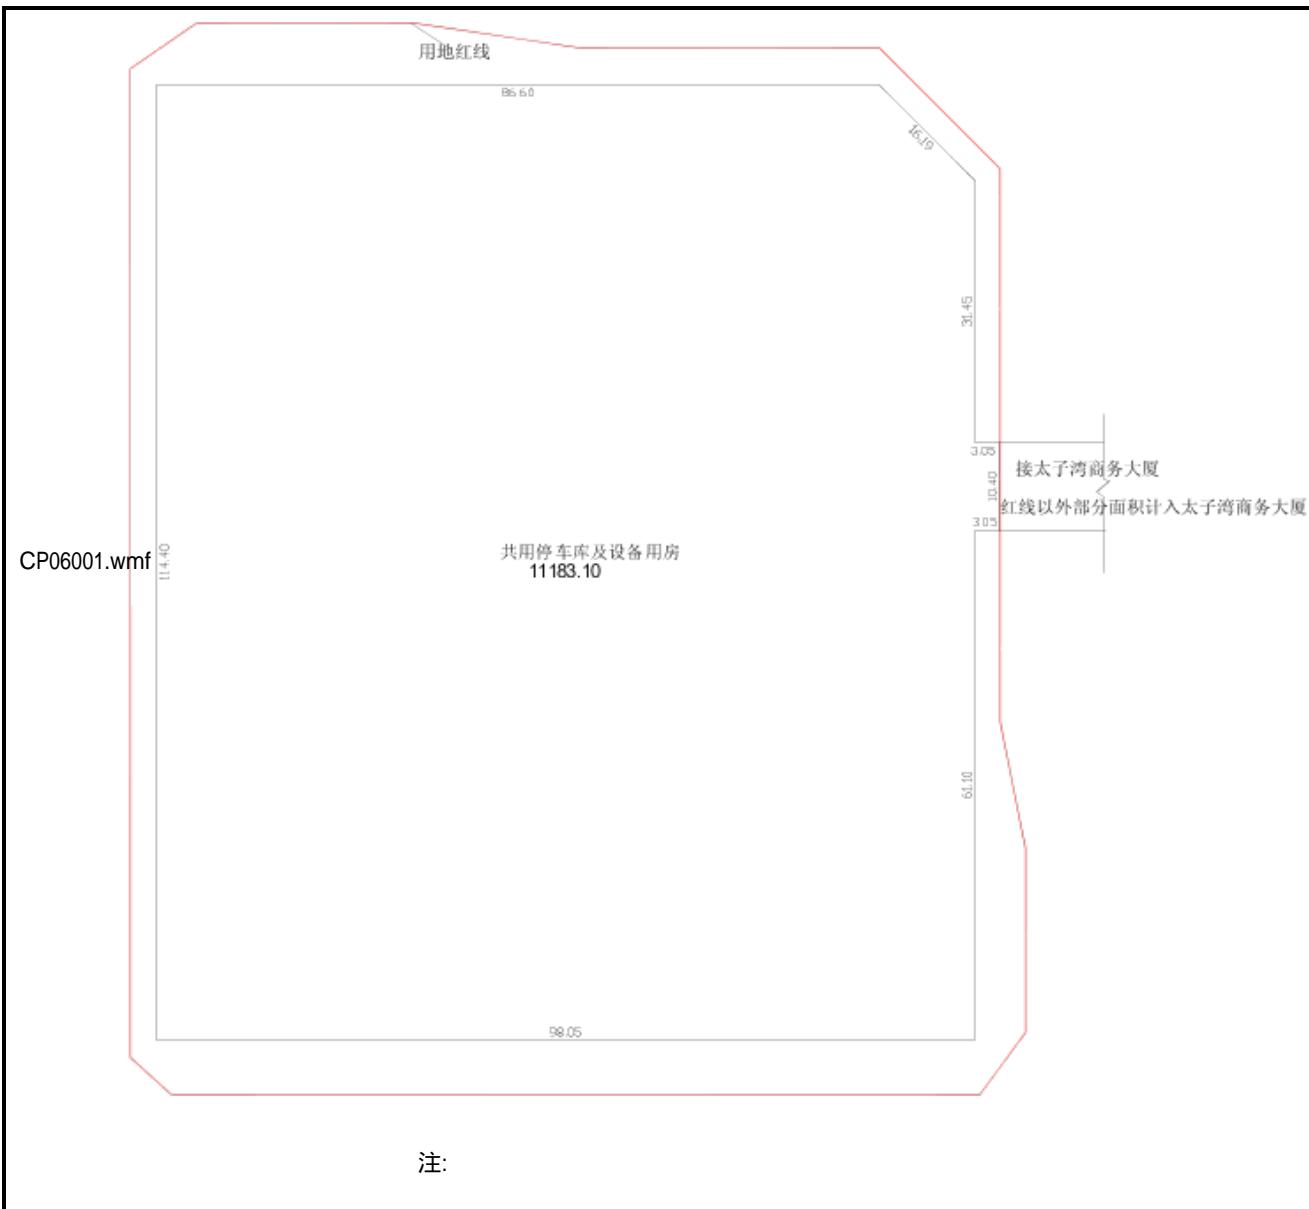


宗地号	K202-0031	
宗地代码	440305007003GB00034	
栋号及名称	太子湾商贸大厦1栋办公	
层 次	07-15奇数	
房 号	01	
建筑面积类别	预售测绘	
建筑面 积	408.9	
其 中	套内建筑面积	271.25
	分摊公用面积	137.65
备注:		
公用建筑面积包括:		
应分摊的公用建筑面积;		
不分摊的公用建筑面积。		
具体内容参见:		
《公用建筑面积分层汇总表》;		
《公用建筑面积分层平面图》;		
《房屋建筑面积分户位置图》。		

## 房屋建筑面积分户平面图

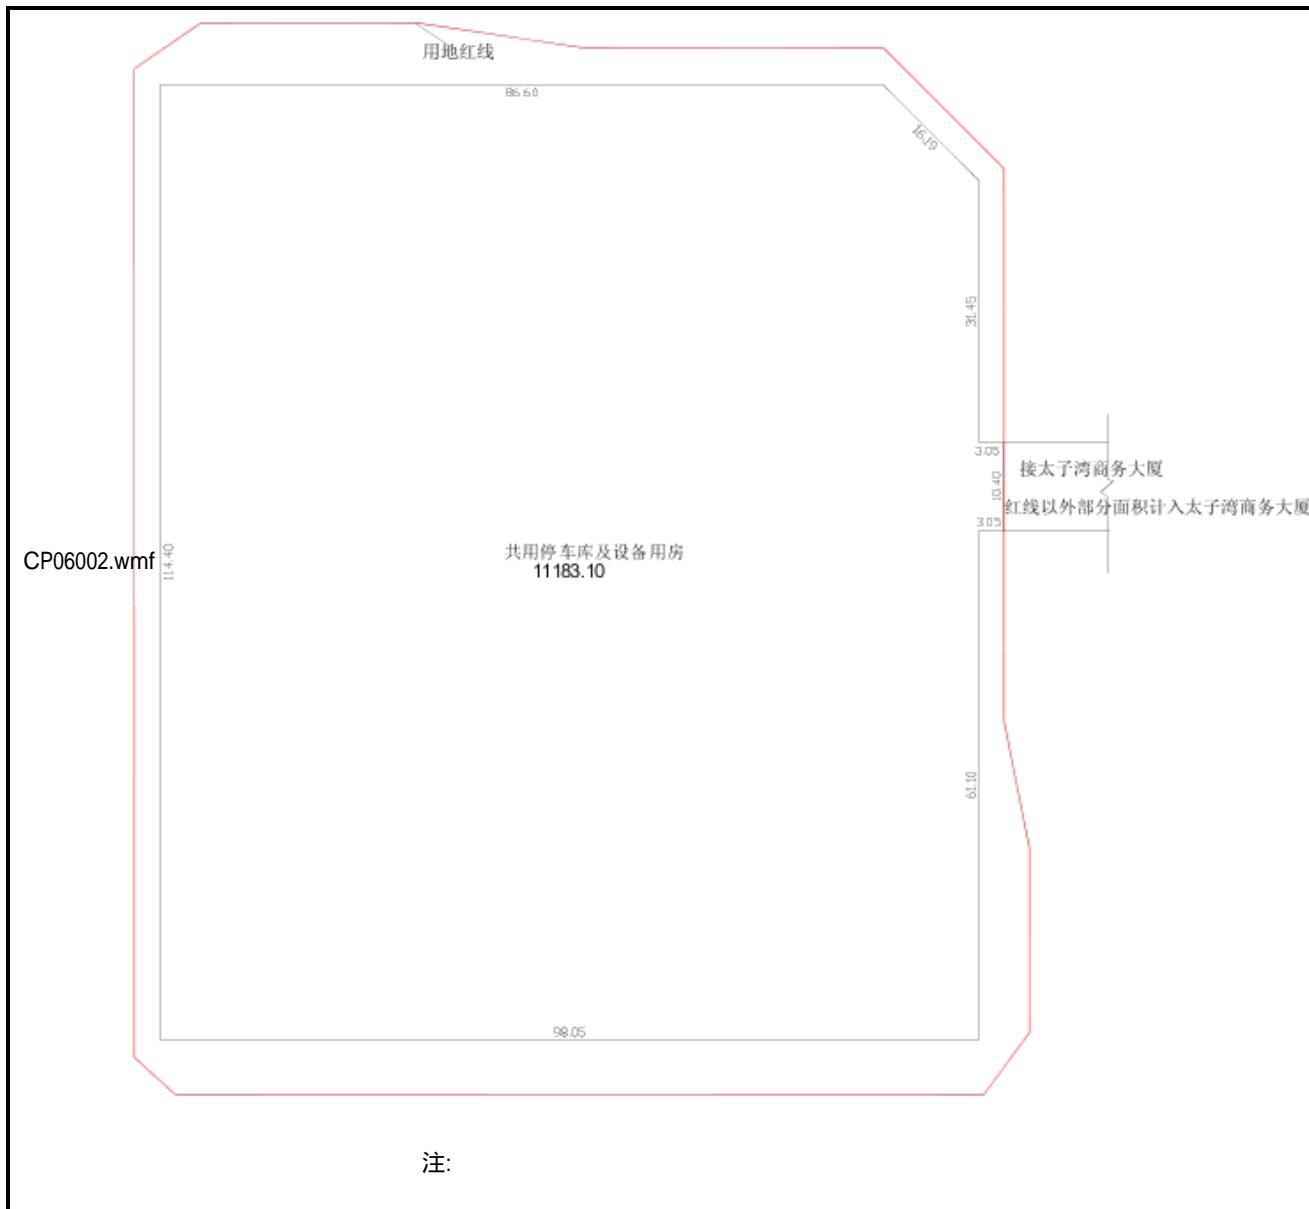


宗地号	K202-0031	
宗地代码	440305007003GB00034	
栋号及名称	太子湾商贸大厦1栋办公	
层 次	07-15奇数	
房 号	02	
建筑面积类别	预售测绘	
建筑面 积	400.26	
其 中	套内建筑面积	265.51
	分摊公用面积	134.75
备注：		
公用建筑面积包括：		
应分摊的公用建筑面积；		
不分摊的公用建筑面积。		
具体内容参见：		
《公用建筑面积分层汇总表》；		
《公用建筑面积分层平面图》；		
《房屋建筑面积分户位置图》。		
测绘单位	深圳市地籍测绘大队	
测绘日期	2018年8月3日	


# 房屋建筑面积分户平面图

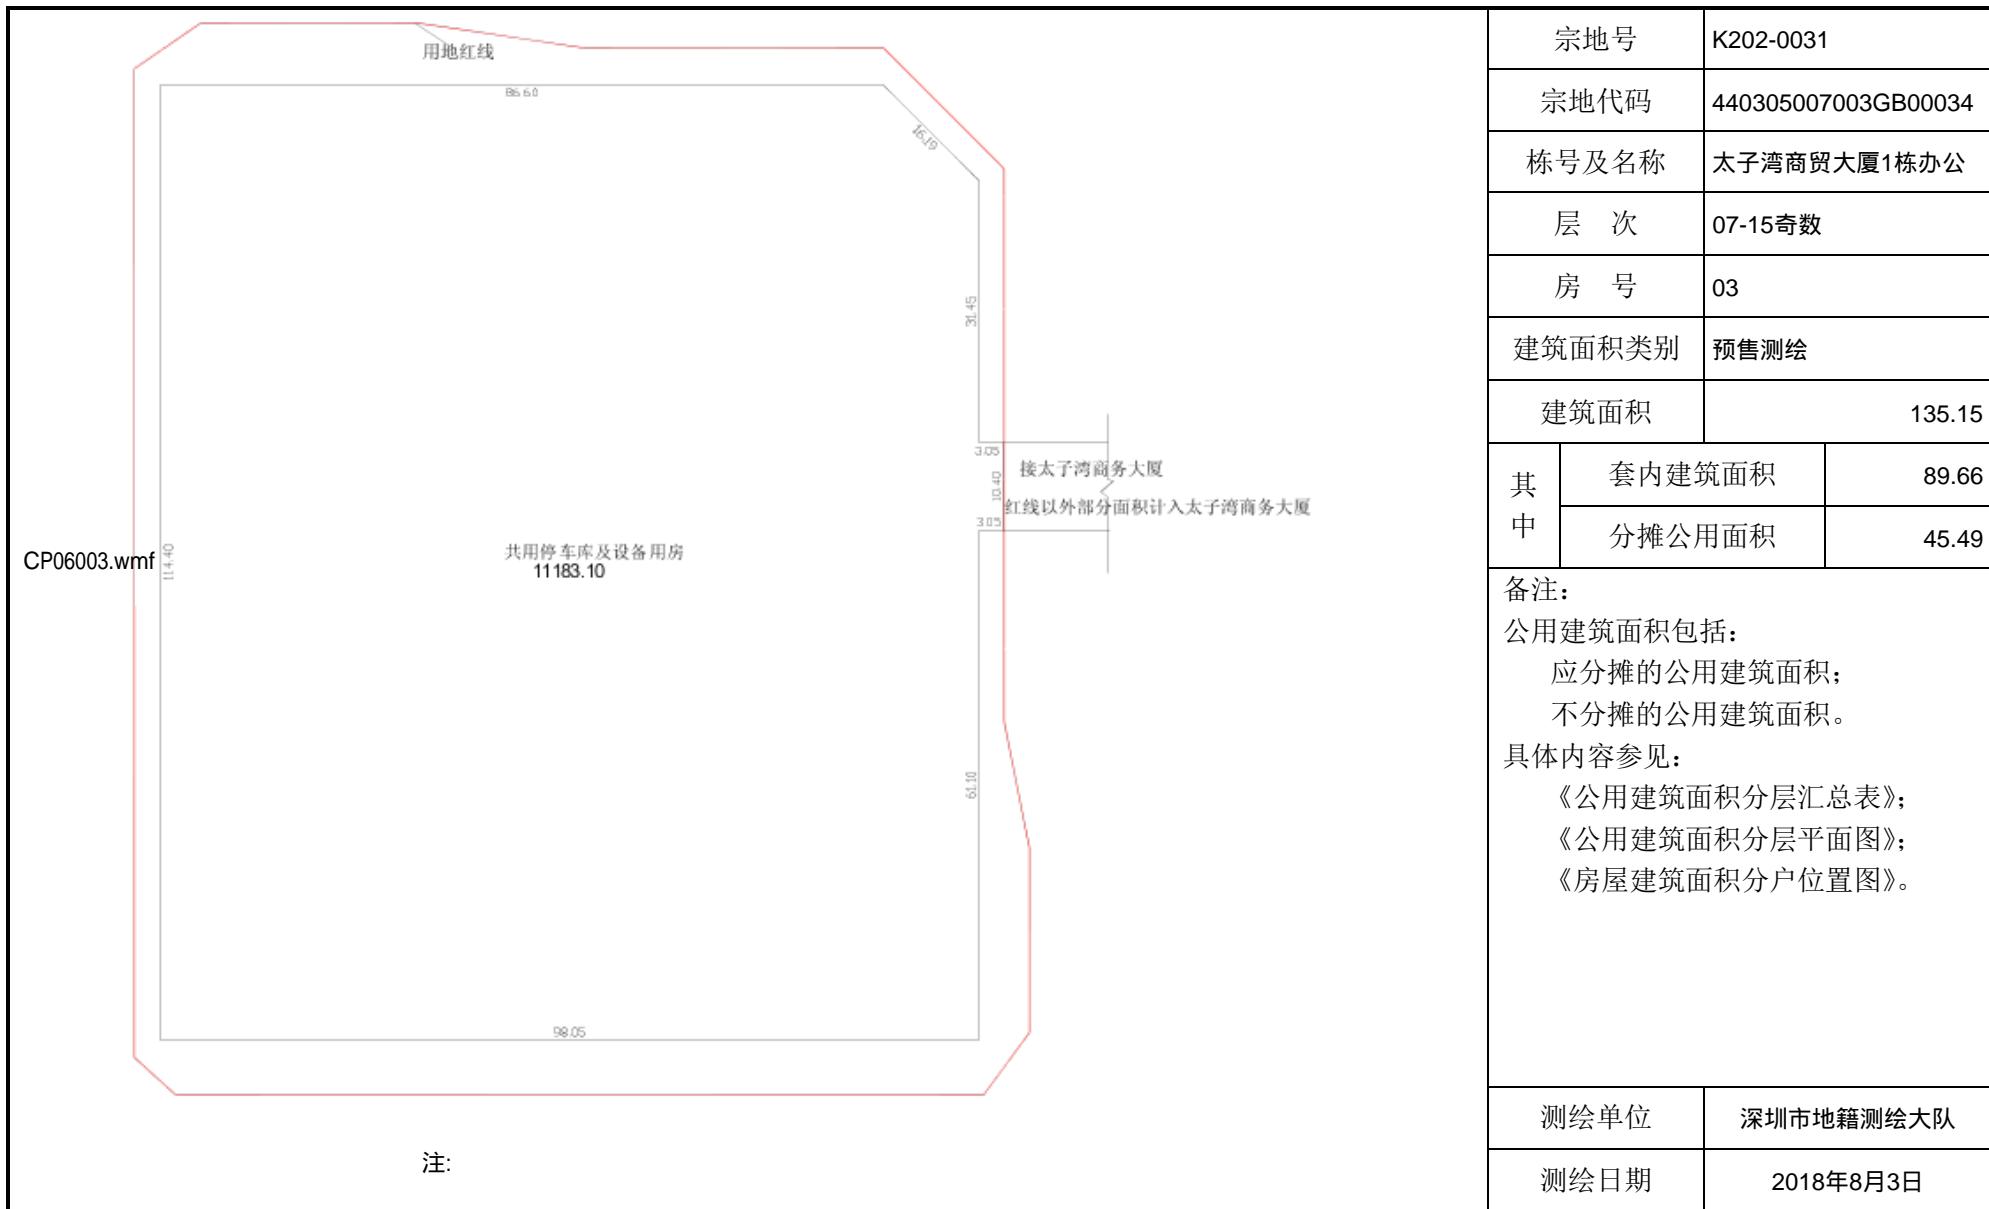

# 房屋建筑面积分户平面图

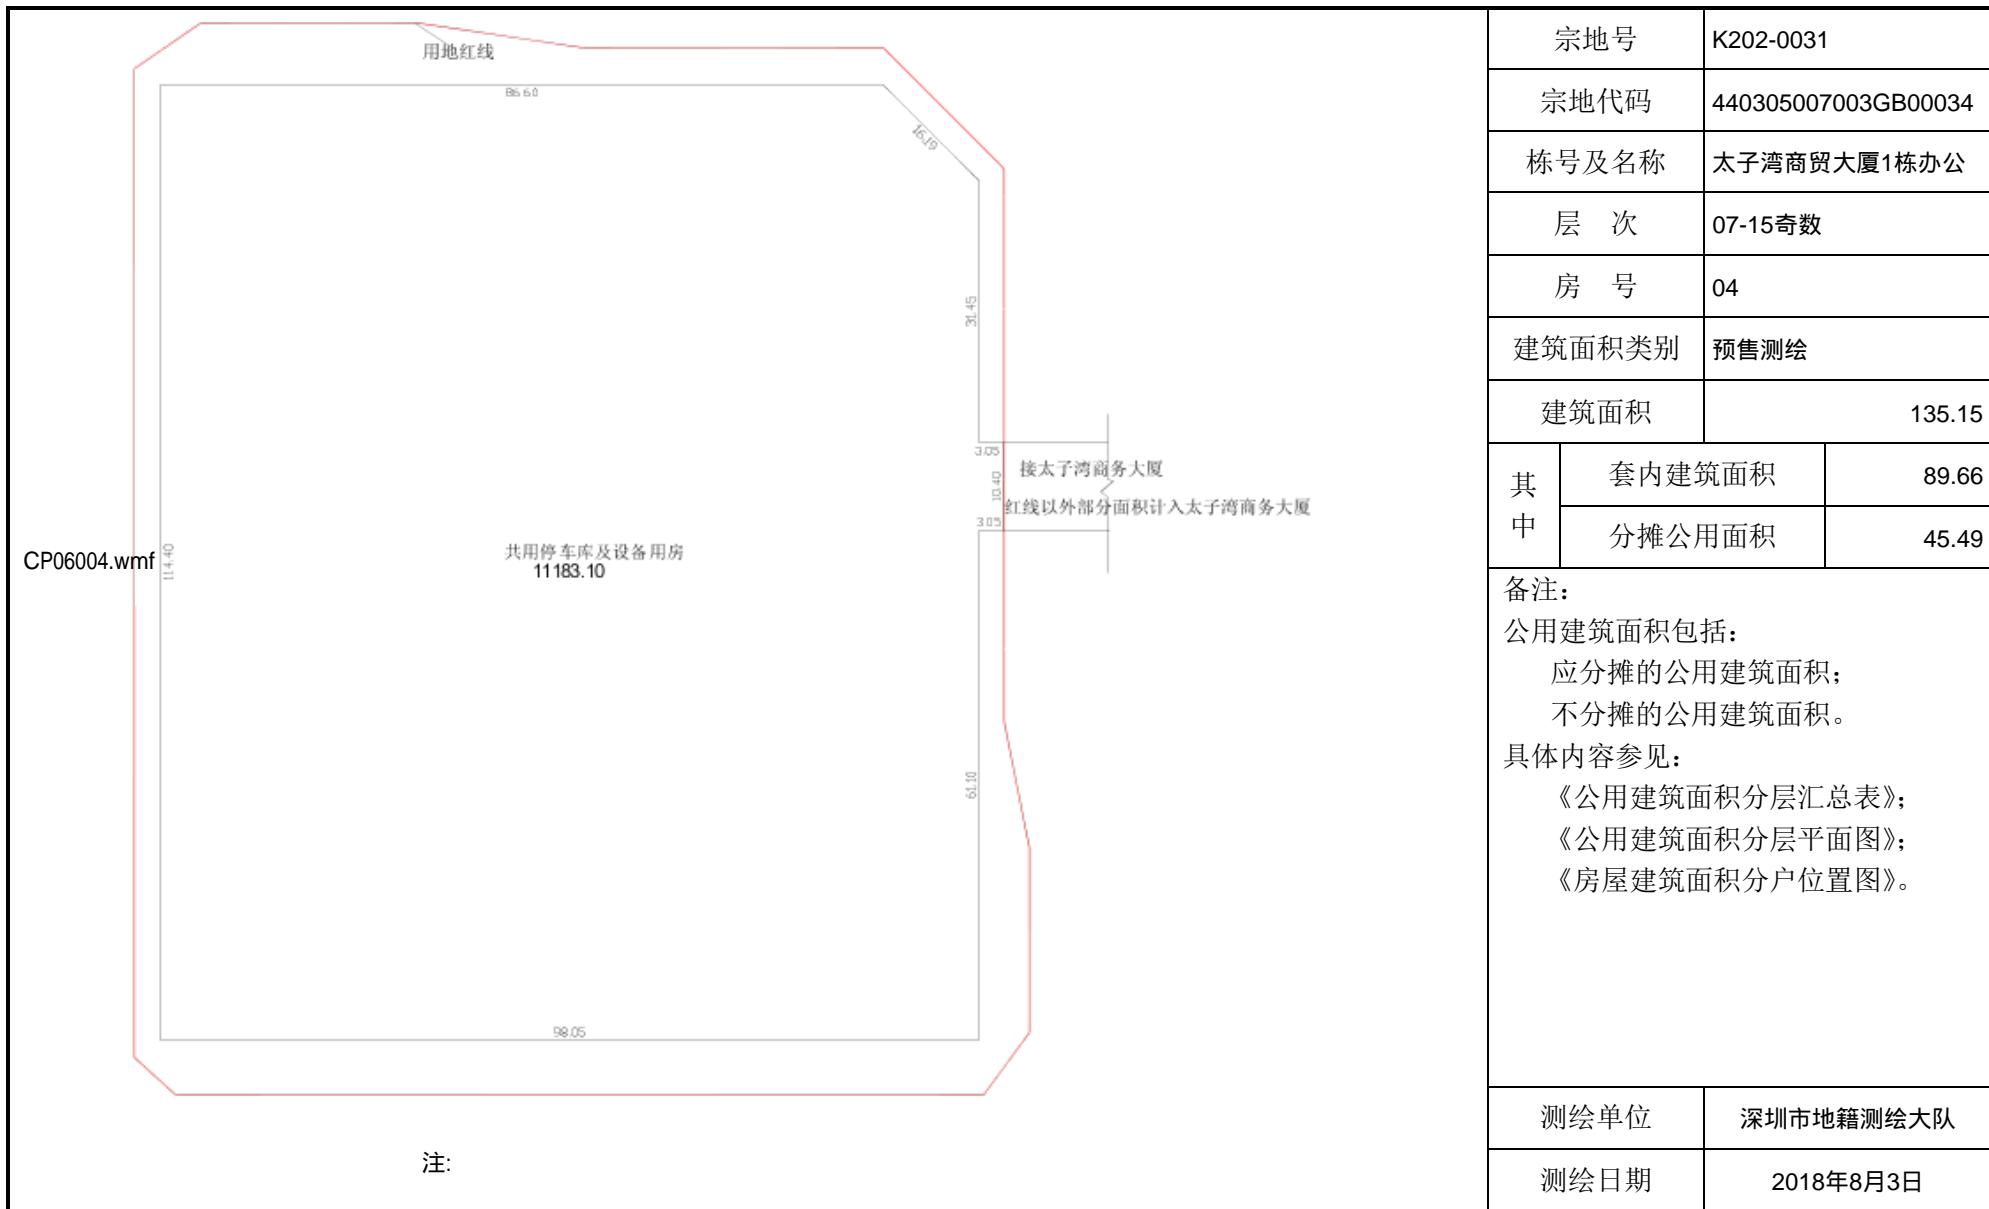


## 房屋建筑面积分户平面图

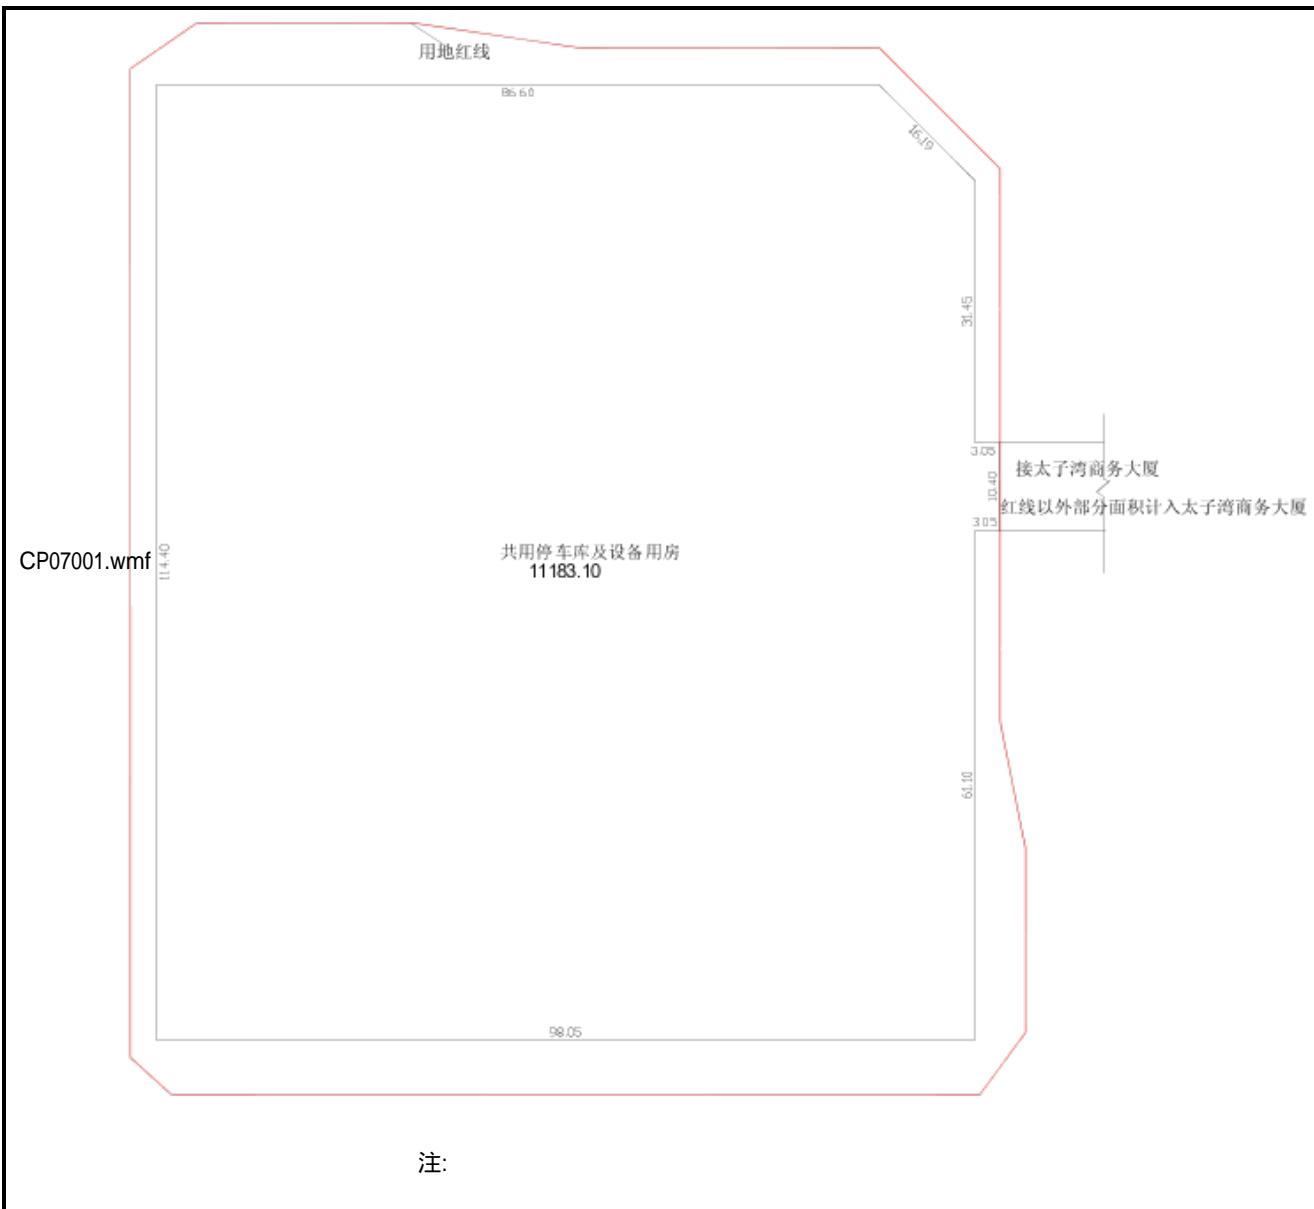


宗地号	K202-0031	
宗地代码	440305007003GB00034	
栋号及名称	太子湾商贸大厦1栋办公	
层 次	16	
房 号	01	
建筑面积类别	预售测绘	
建筑面积	396.99	
其中	套内建筑面积	268.2
	分摊公用面积	128.79
备注：		
公用建筑面积包括：		
应分摊的公用建筑面积；		
不分摊的公用建筑面积。		
具体内容参见：		
《公用建筑面积分层汇总表》；		
《公用建筑面积分层平面图》；		
《房屋建筑面分户位置图》。		
测绘单位	深圳市地籍测绘大队	
测绘日期	2018年8月3日	

## 房屋建筑面积分户平面图

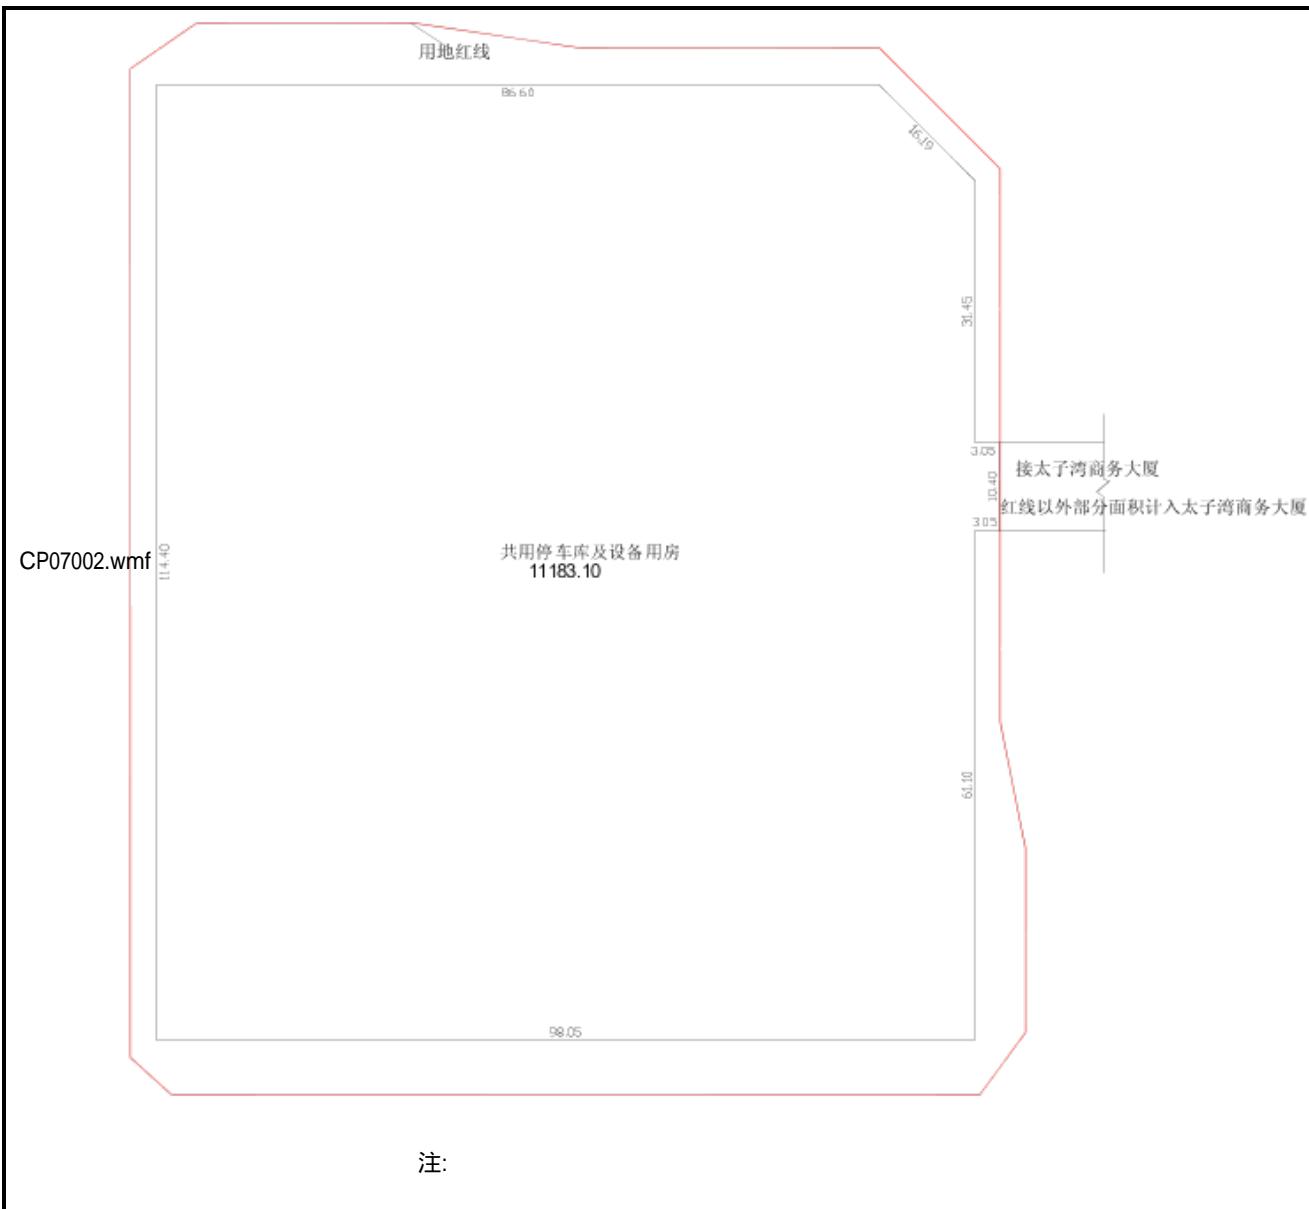


宗地号	K202-0031	
宗地代码	440305007003GB00034	
栋号及名称	太子湾商贸大厦1栋办公	
层 次	16	
房 号	02	
建筑面积类别	预售测绘	
建筑面 积	388.19	
其 中	套内建筑面积	262.25
	分摊公用面积	125.94
备注：		
公用建筑面积包括：		
应分摊的公用建筑面积；		
不分摊的公用建筑面积。		
具体内容参见：		
《公用建筑面积分层汇总表》；		
《公用建筑面积分层平面图》；		
《房屋建筑面积分户位置图》。		

# 房屋建筑面积分户平面图

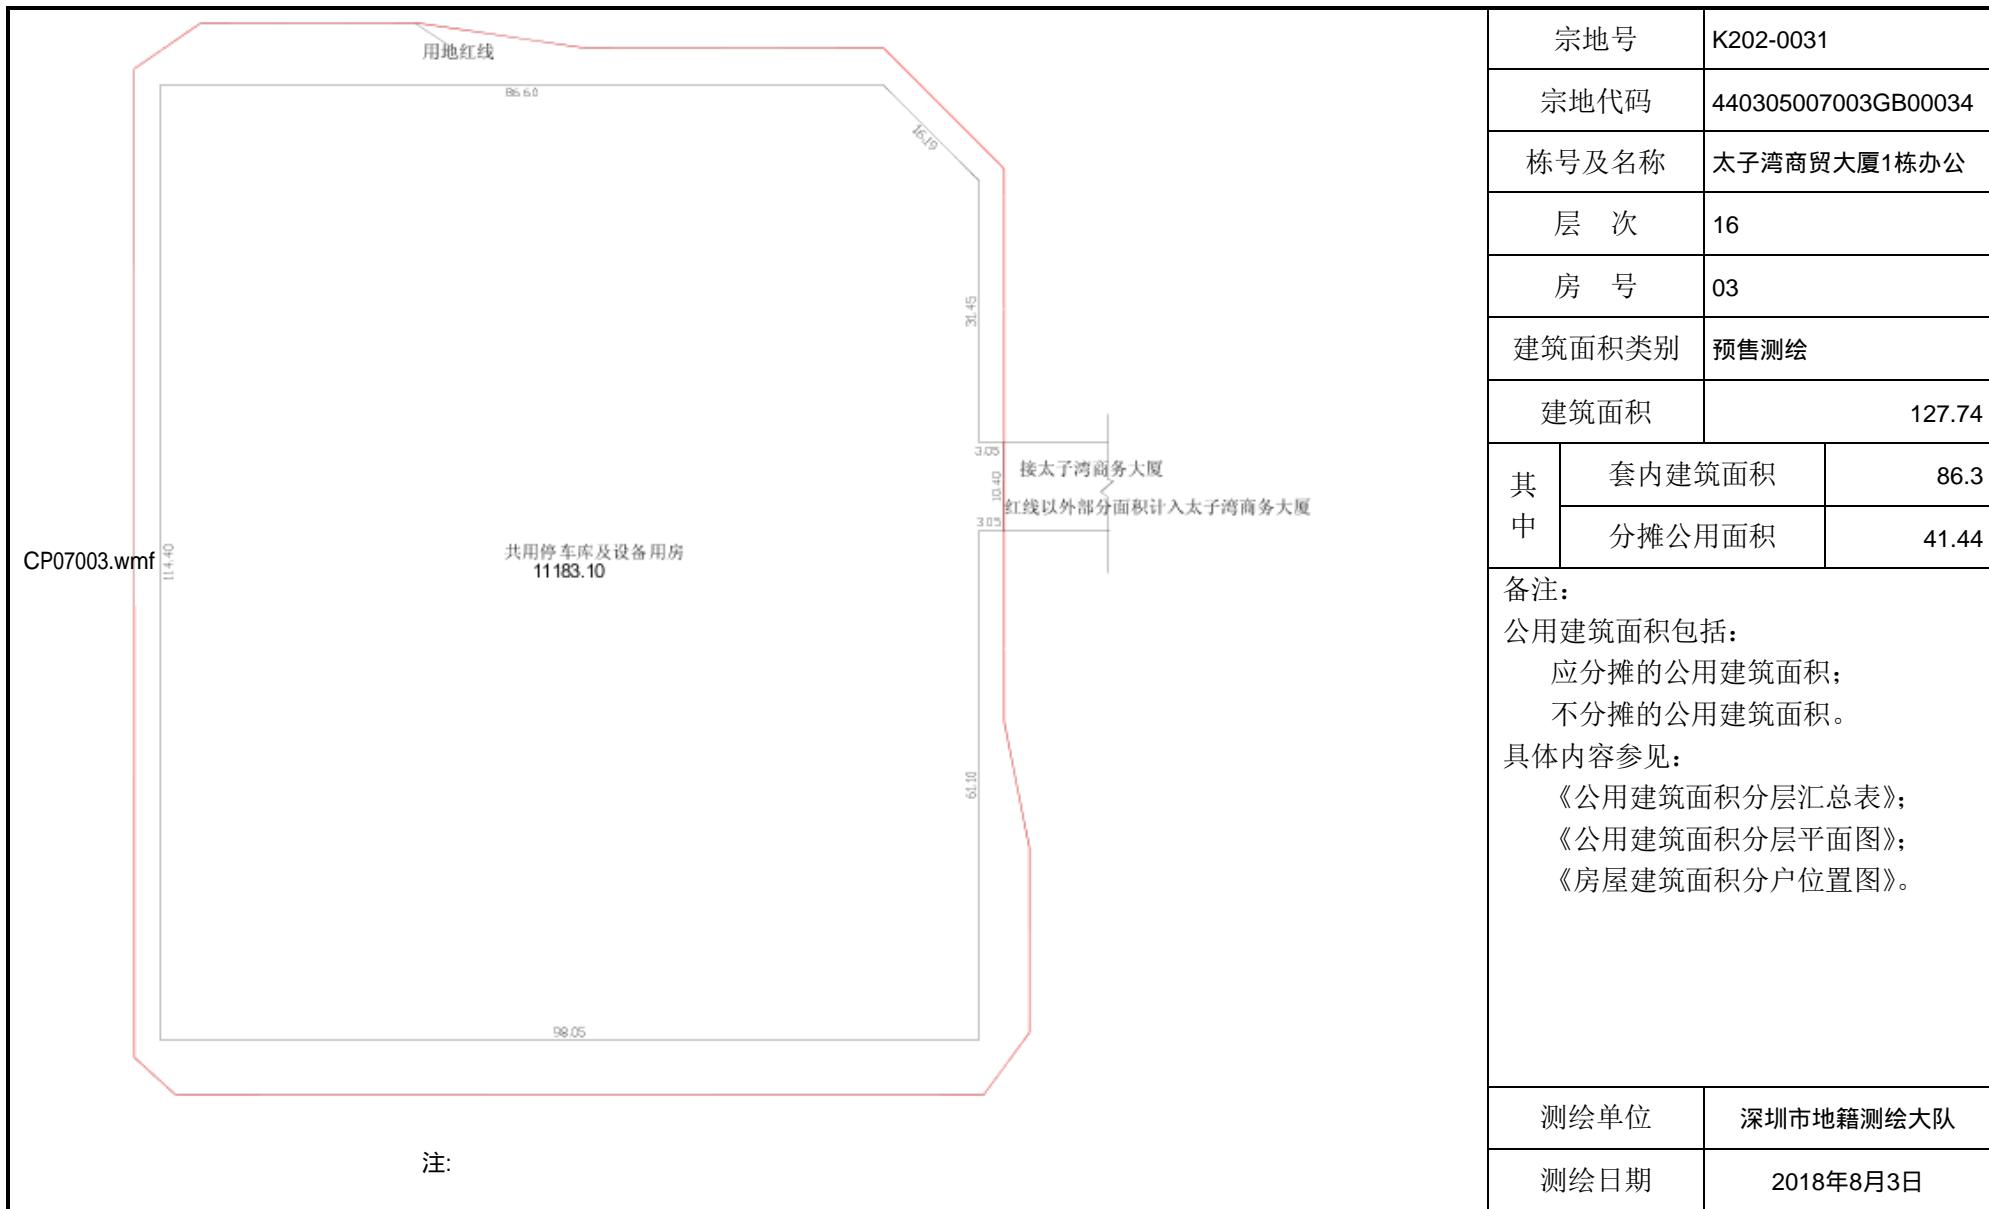

## 房屋建筑面积分户平面图

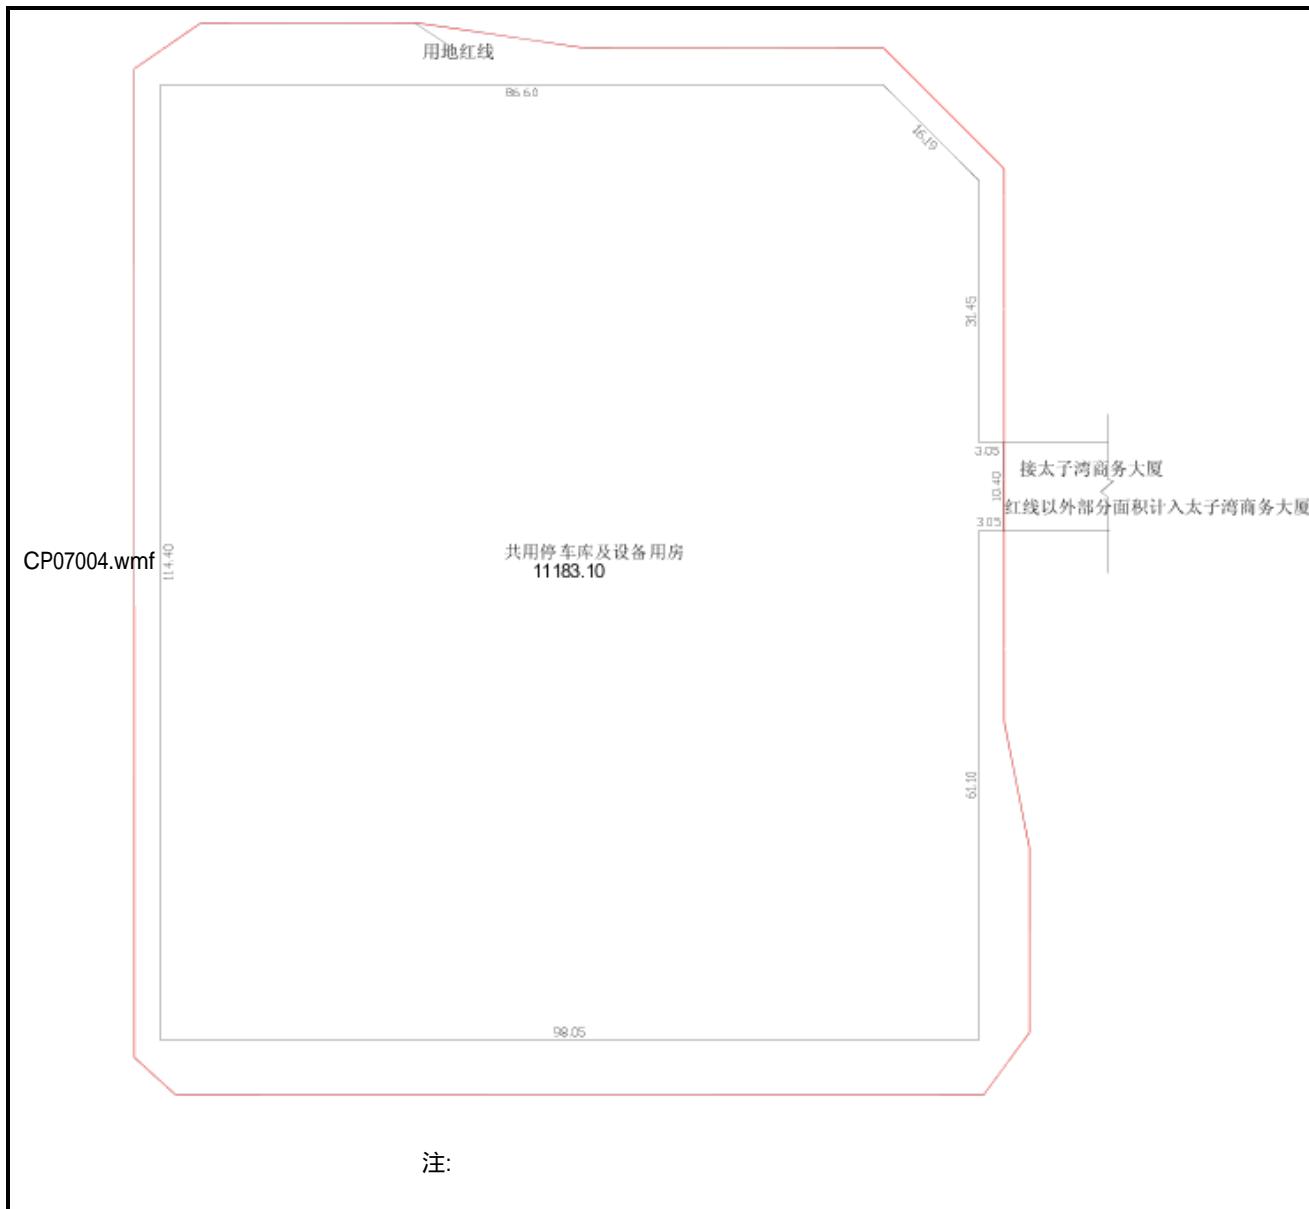

宗地号	K202-0031	
宗地代码	440305007003GB00034	
栋号及名称	太子湾商贸大厦1栋办公	
层 次	16	
房 号	04(复式1层)	
建筑面积类别	预售测绘	
建筑面积	149.79	
其 中	套内建筑面积	101.19
	分摊公用面积	48.6
<b>备注:</b> 公用建筑面积包括: 应分摊的公用建筑面积; 不分摊的公用建筑面积。 <b>具体内容参见:</b> 《公用建筑面积分层汇总表》; 《公用建筑面积分层平面图》; 《房屋建筑面积分户位置图》。		

# 房屋建筑面积分户平面图

